


ARCHITECTURAL PORTFOLIO

EMILY CUBEROS

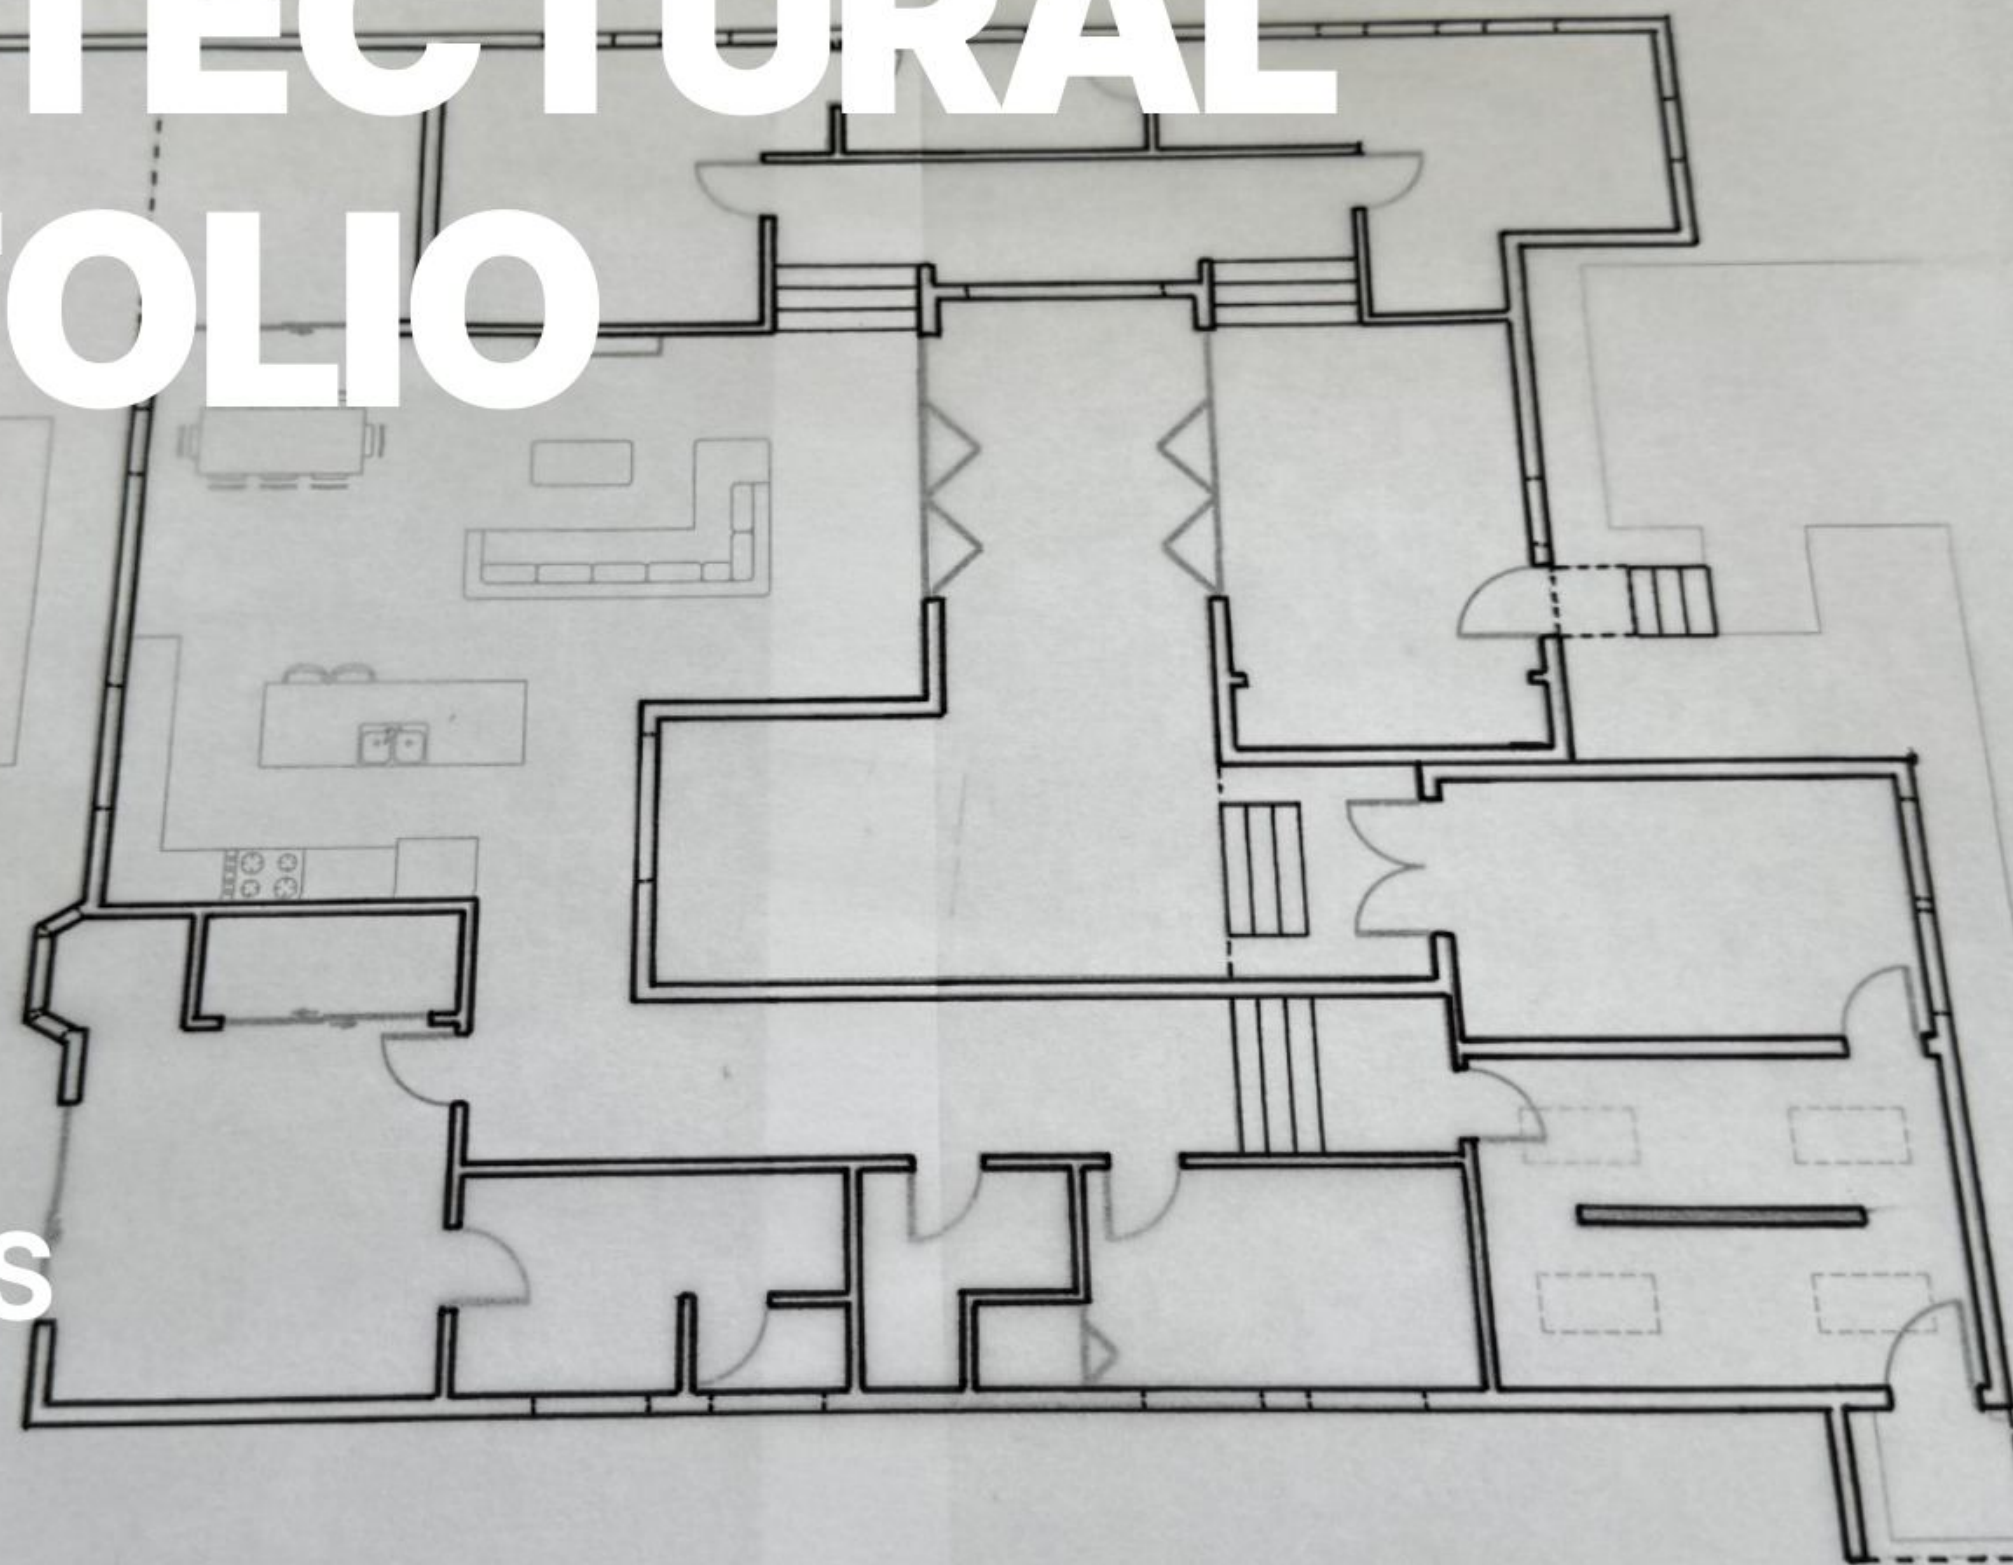


ABOUT ME

I am an Interdisciplinary Studies student at Florida International University with a strong focus in project management and architecture. I have always been drawn to architecture and design and feel that I have a good balance of creativity and purpose-driven structure. My attention to detail and hard-working mindset drives me to successfully execute both short and long-term projects. I have strong organizational skills, and I strive to achieve goals in an efficient and timely manner. One of my main design focuses is a combination of aesthetic appeal and function.

TABLE OF CONTENT

01

RUBELL MUSEUM
COURTYARD ADDITION

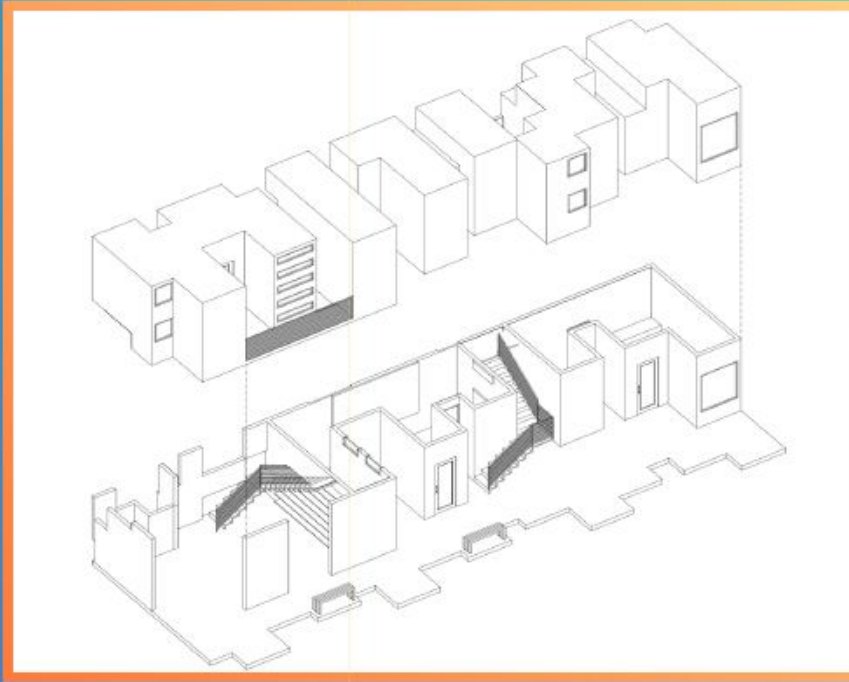


02

LINCOLN ROAD
FOLLY ADDITION




03


ARTIST PATIO
HOUSE

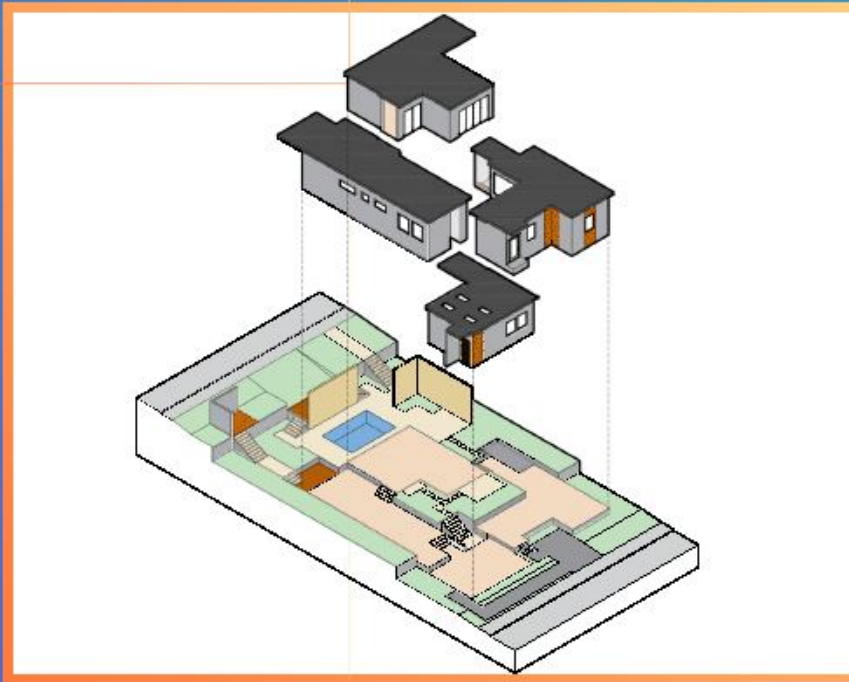

04

FL ROOM AT HISS
STUDIO/RESIDENCE

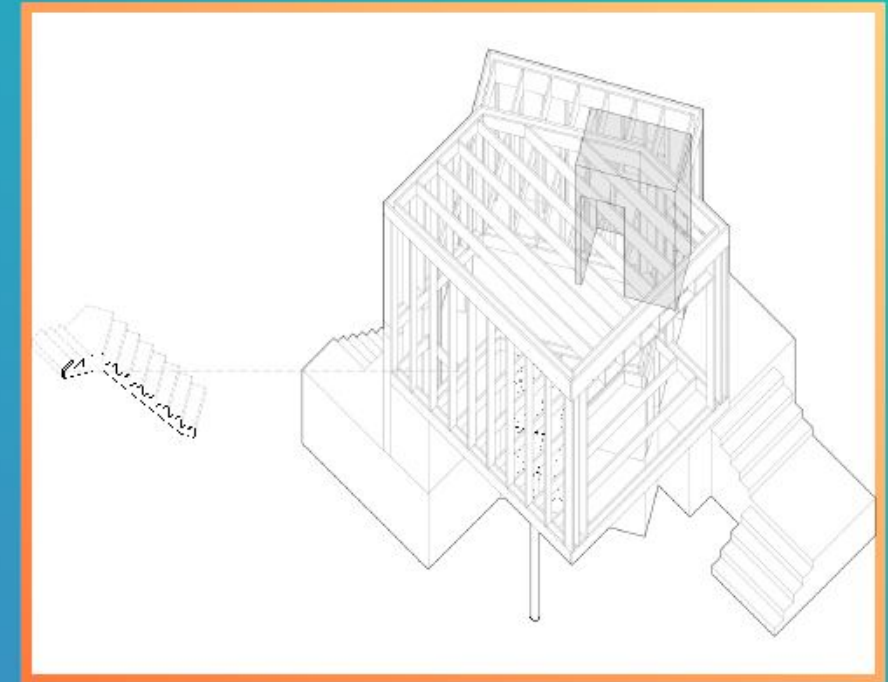

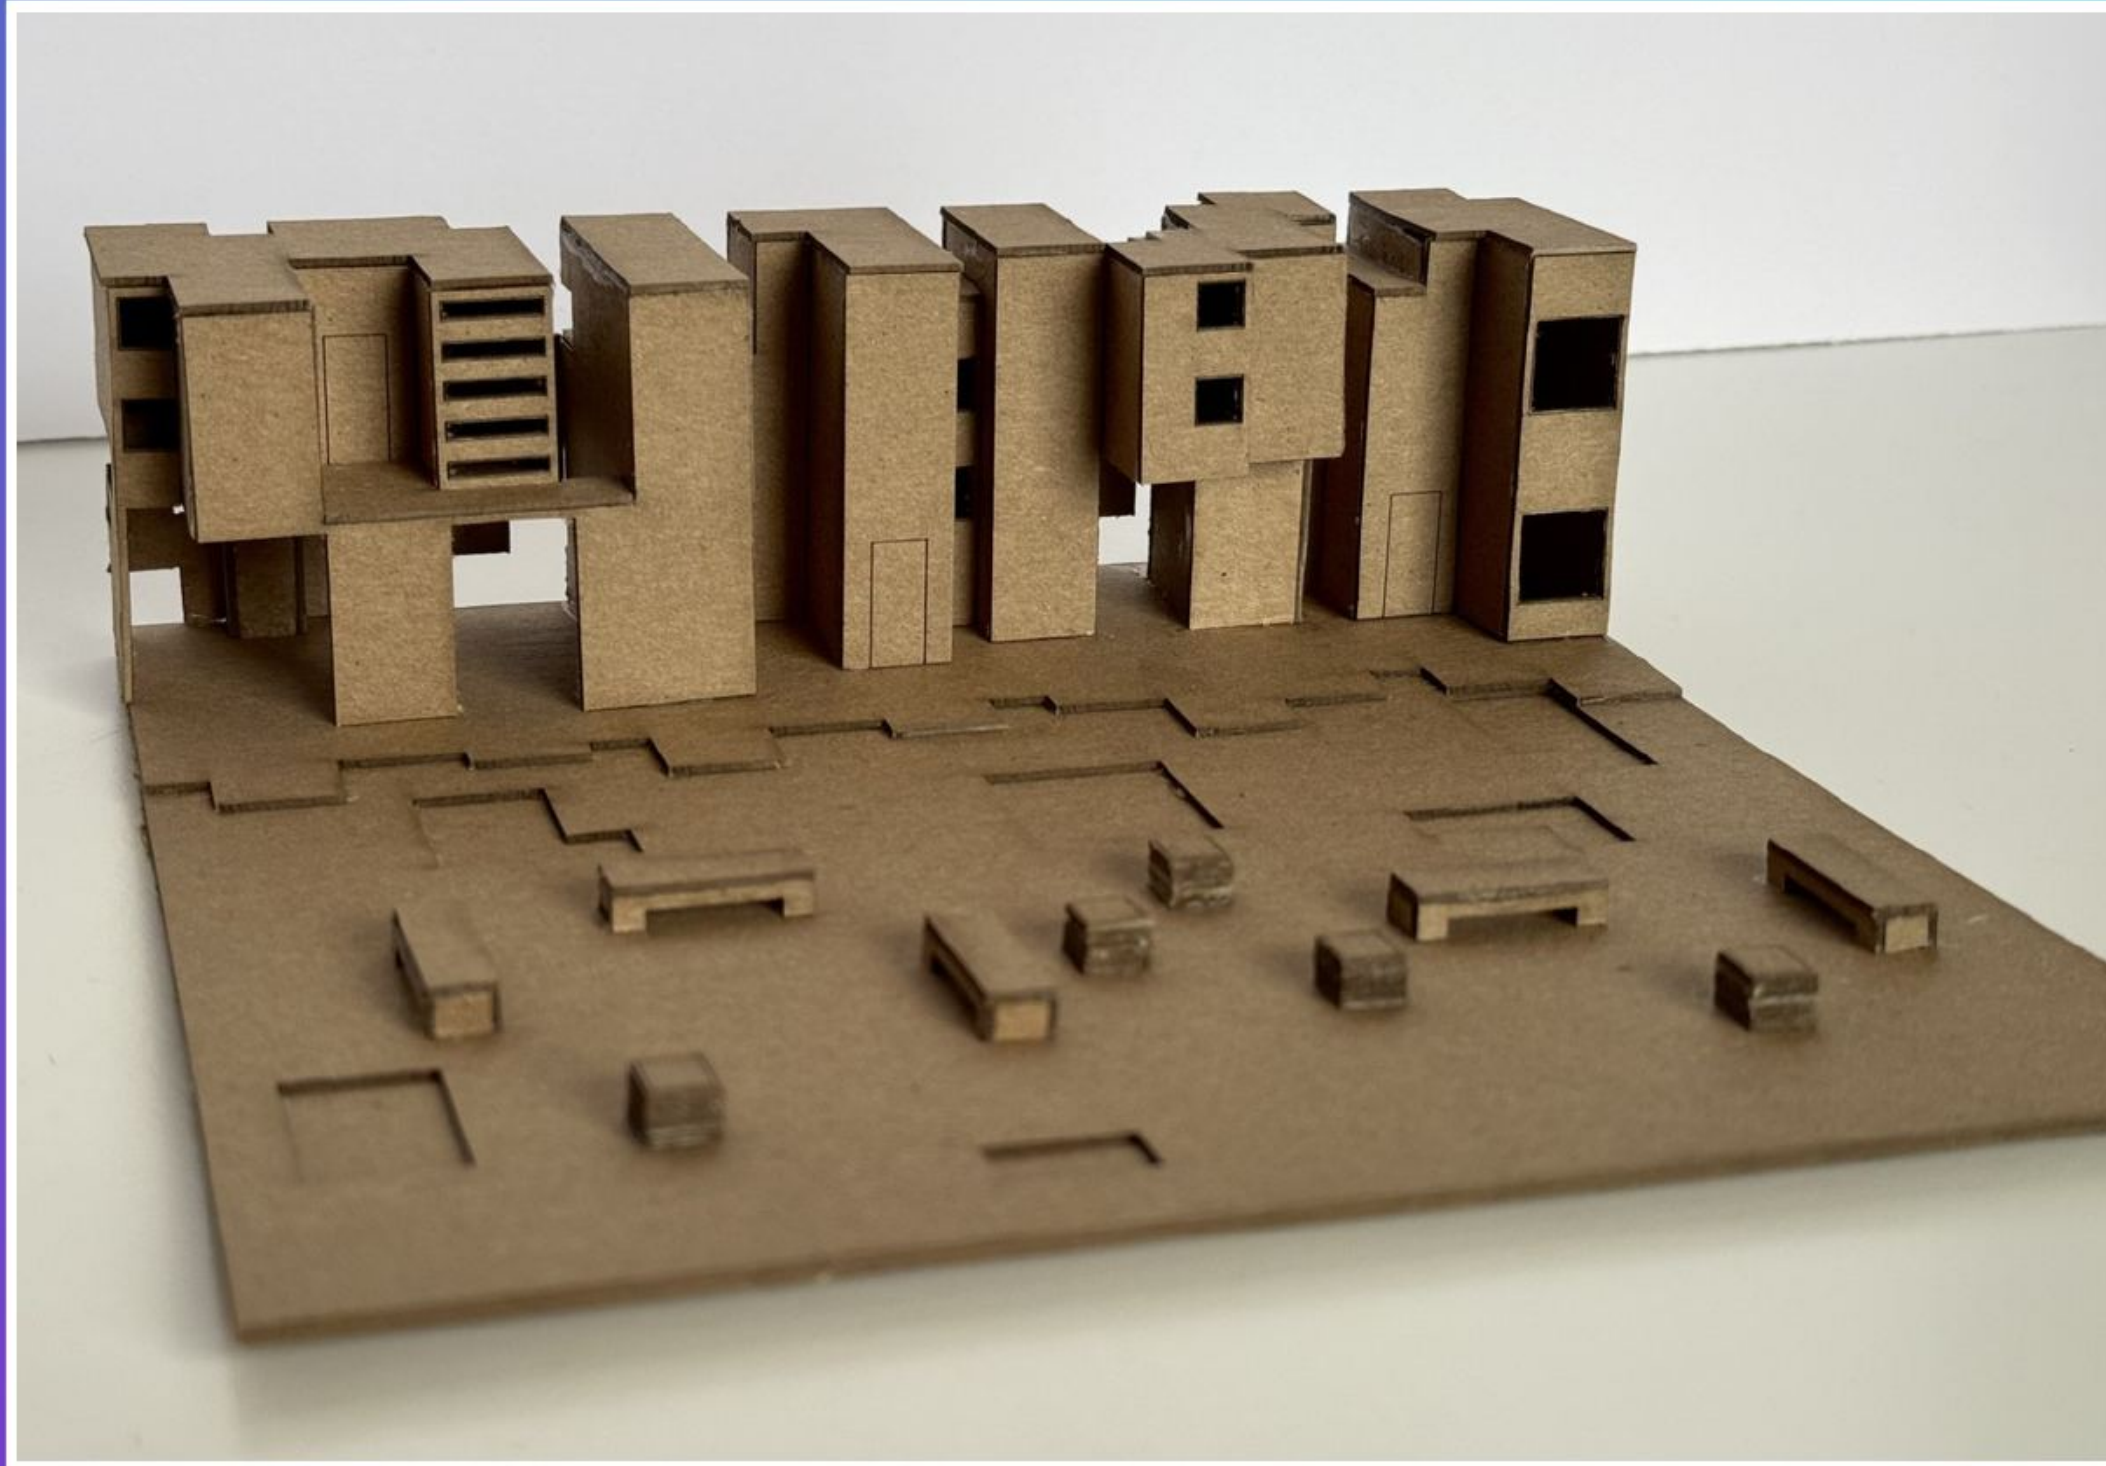


PROJECT - 01



RUBELL MUSEUM COURTYARD ADDITION

The task was to design a building(s) and redesign the courtyard at the Rubell Museum in Miami, Florida. The structure had to sit at the end of the courtyard, next to the street. The design also had to be modeled after the themes in a different specific building. In my case, that building was the Royal Collections Gallery in Madrid. Within the building(s) there had to be an art gallery, a cafe and a library.

SITE PLAN

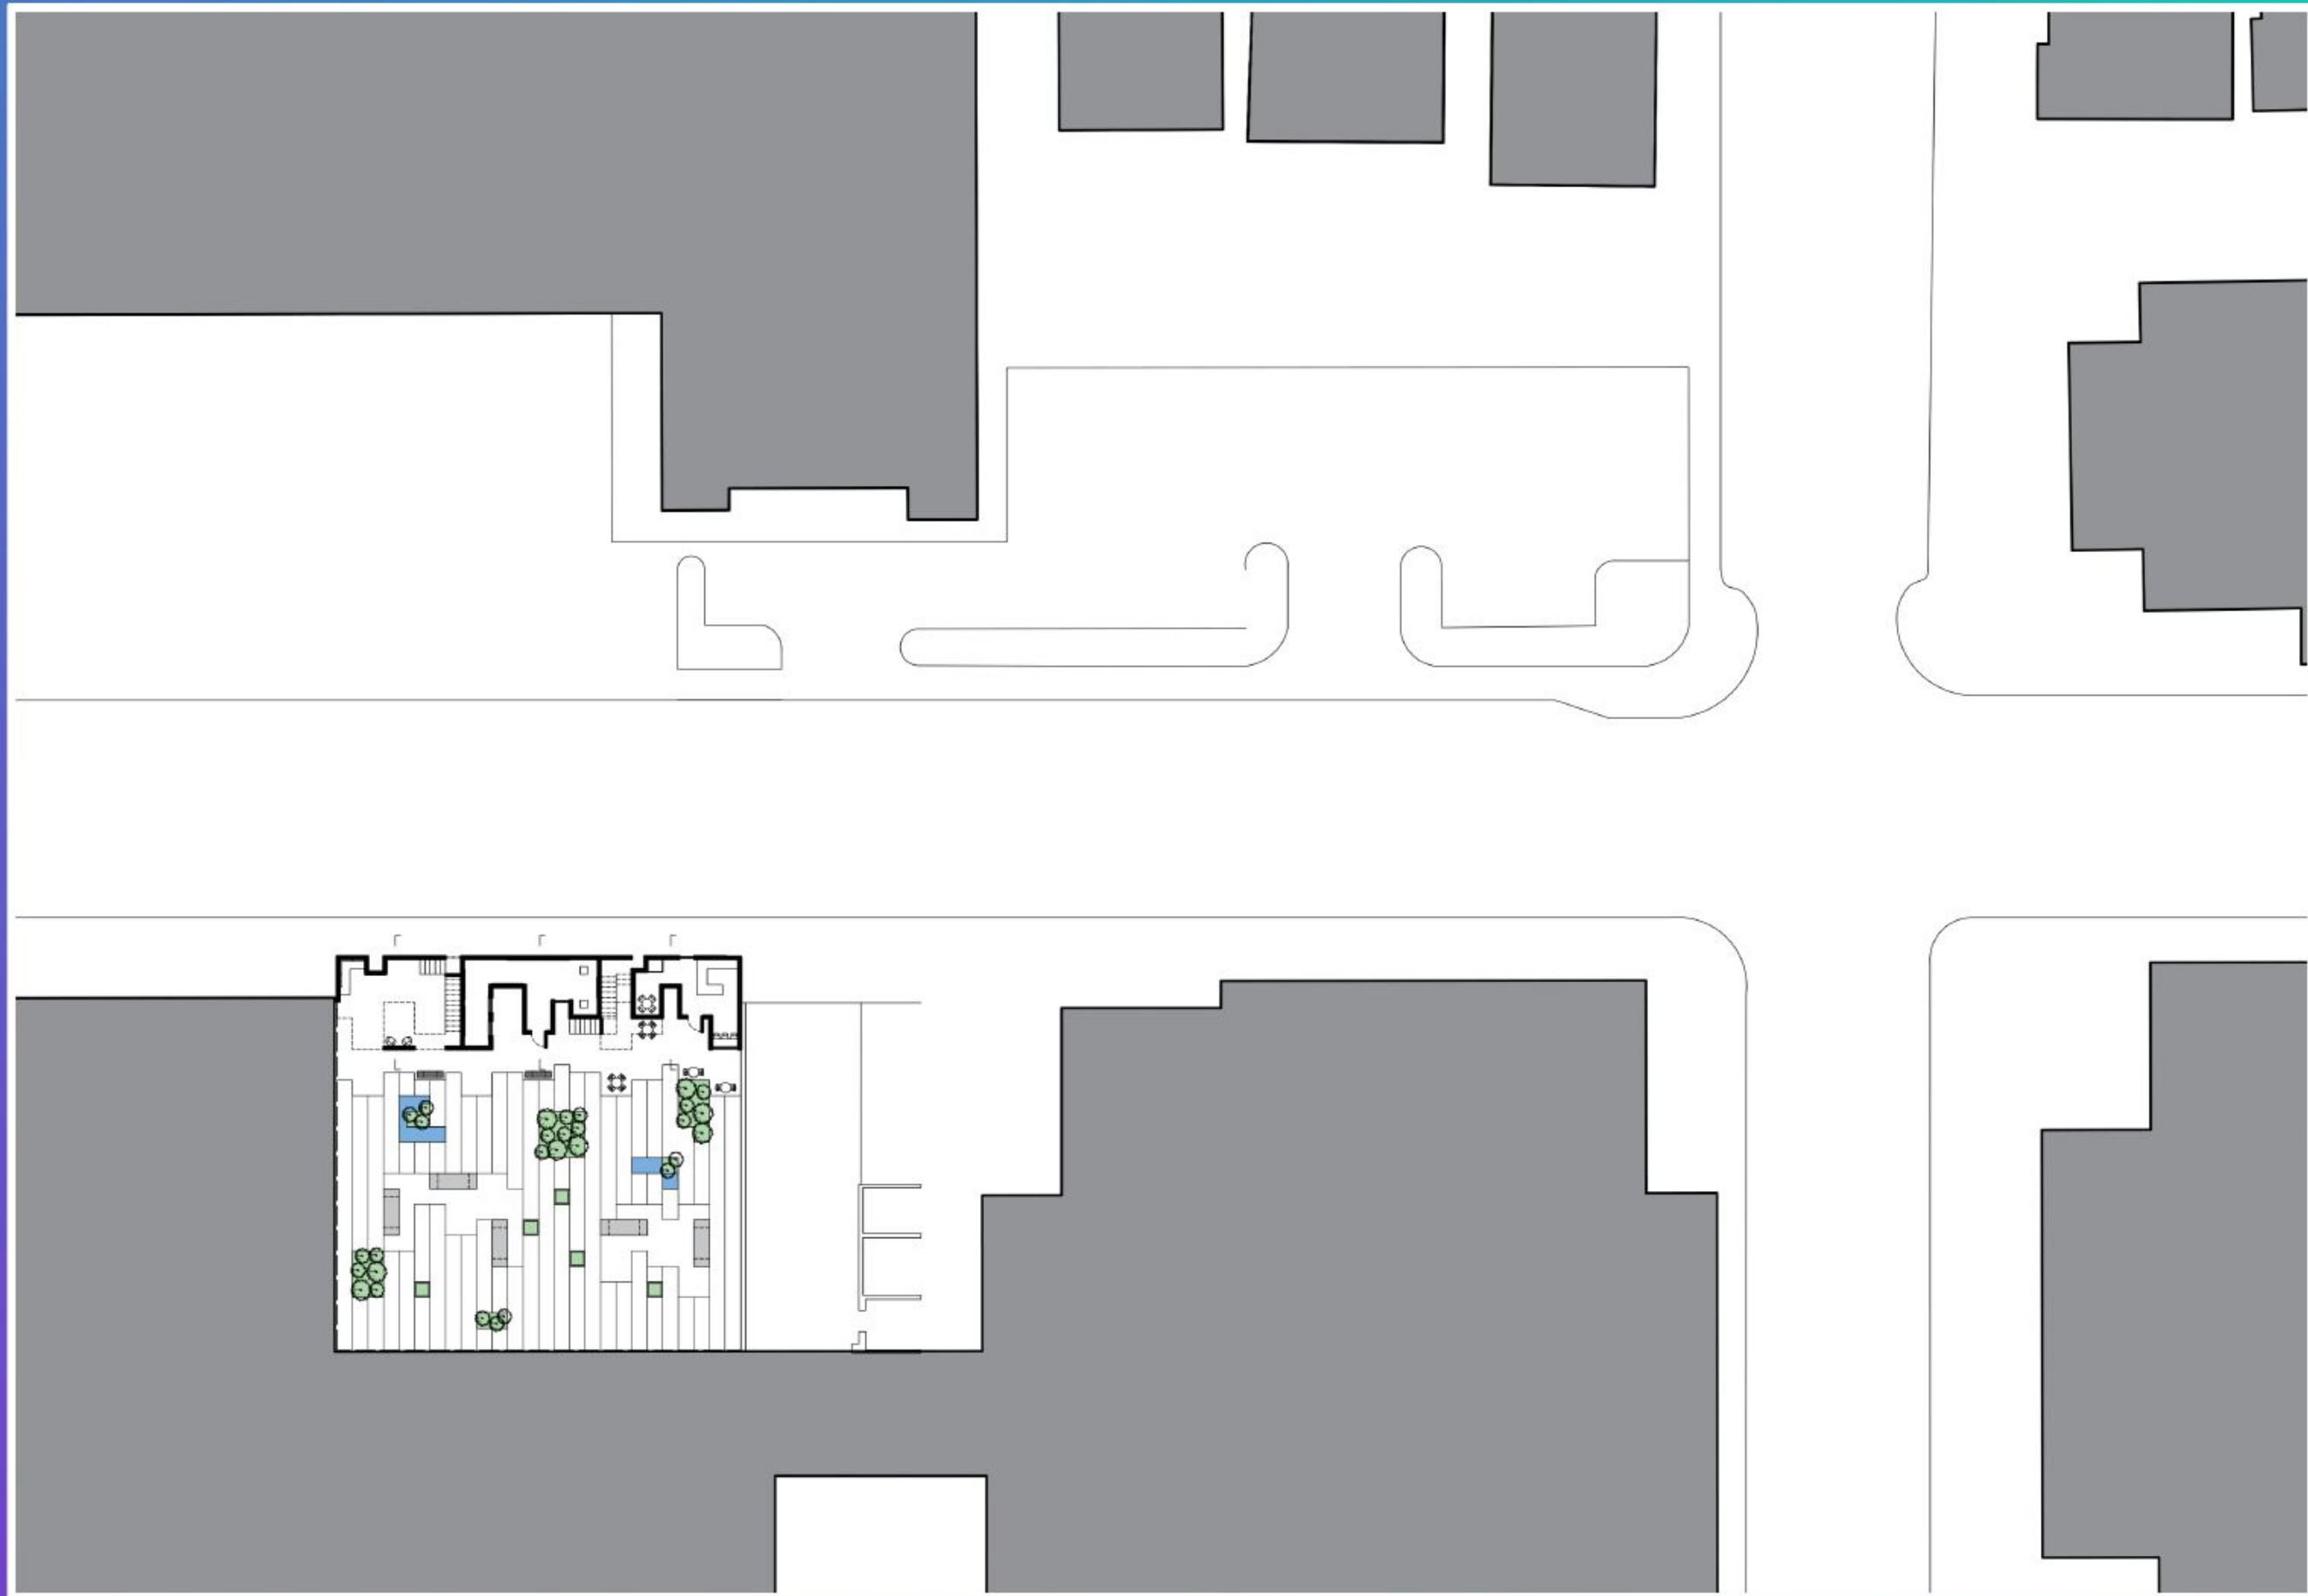

SITE SECTIONS

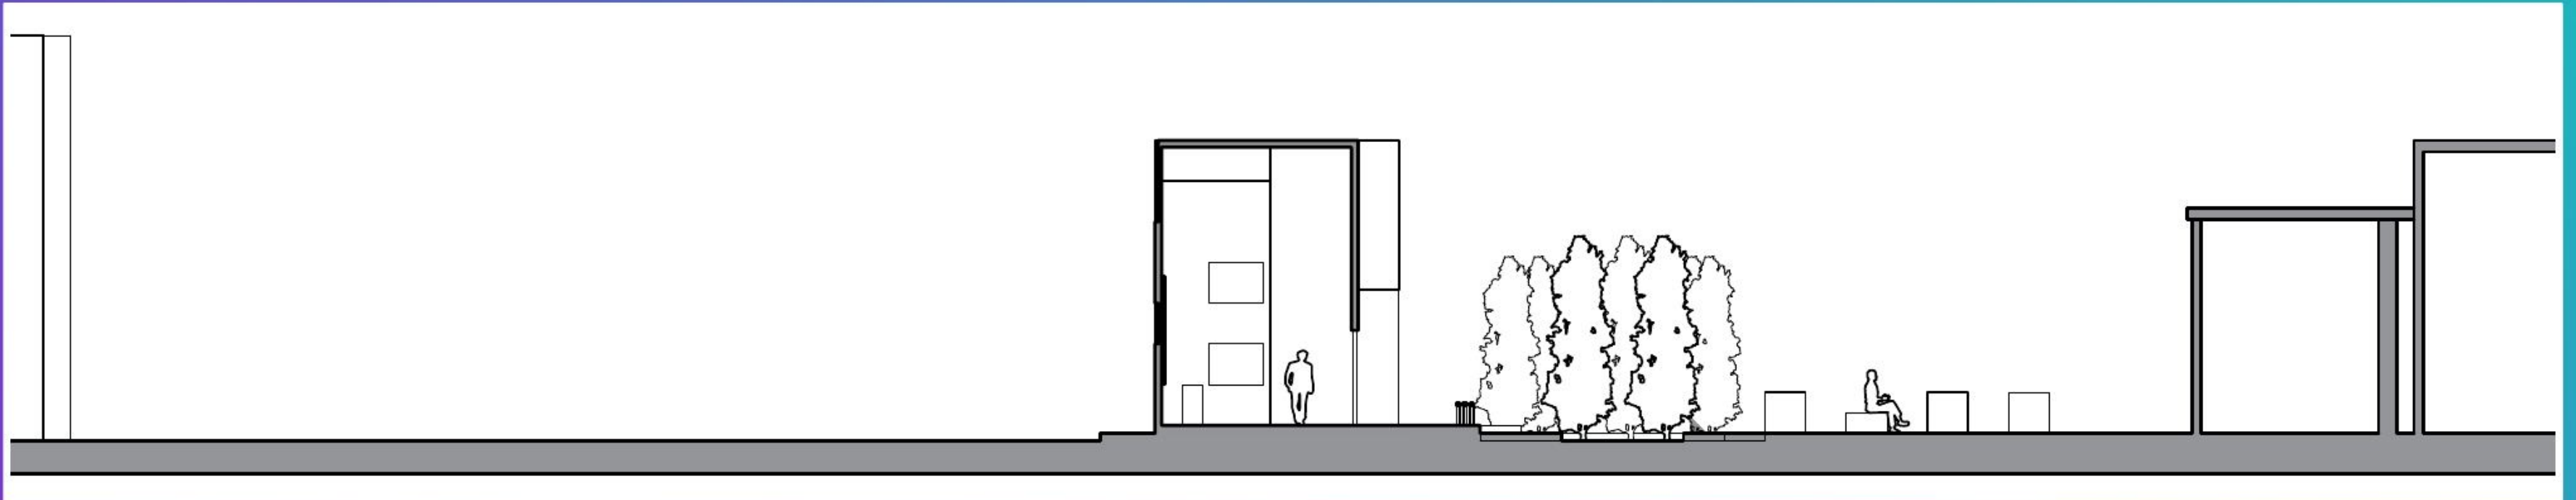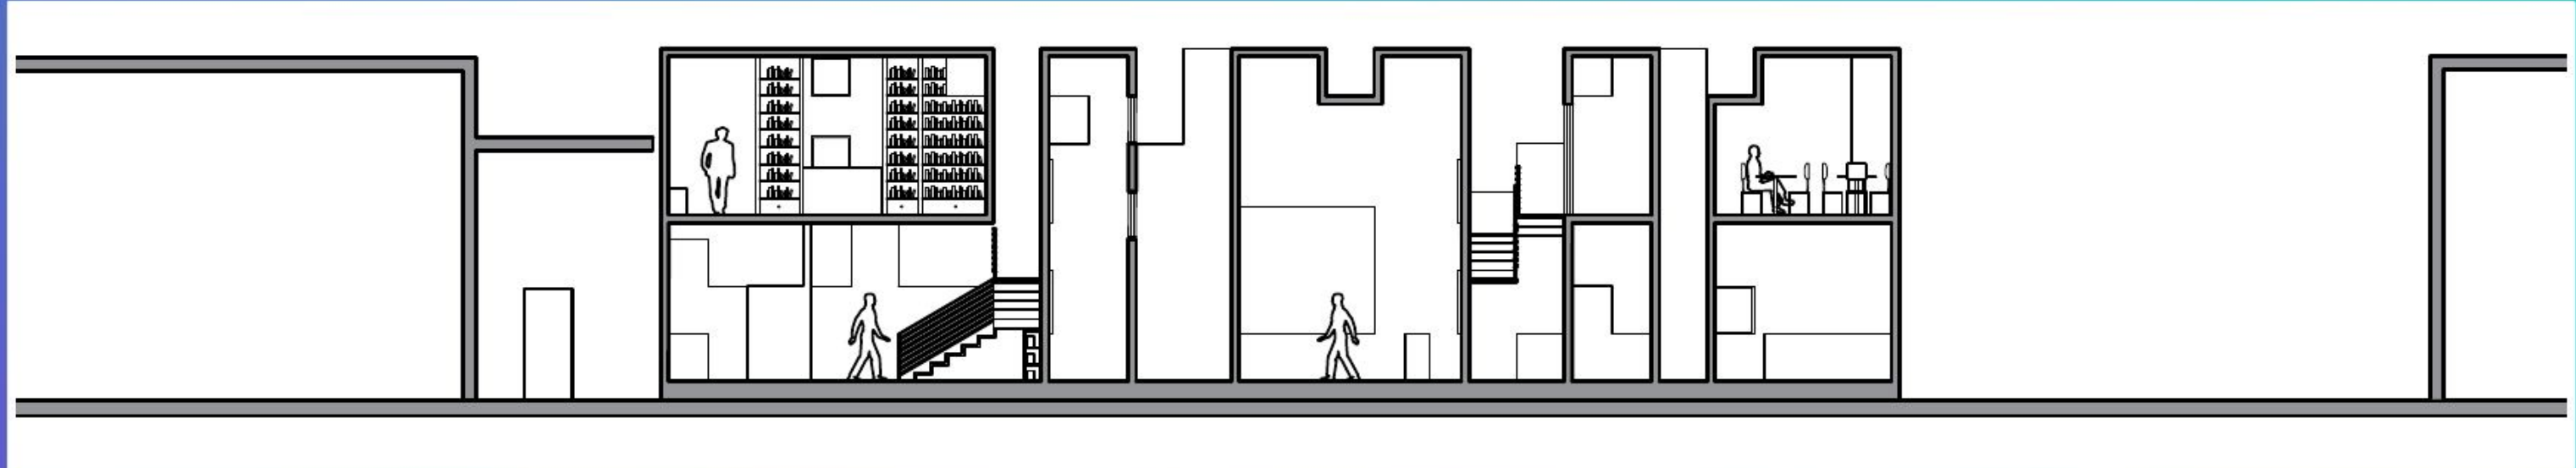

RUBELL MUSEUM NEW EDGE BUILDING

EMILY CUBEROS

CONCEPT TEXT

The concept behind my design of the new building was to take inspiration from the Royal Collections Gallery, without making it look all that similar to it. The main design characteristics from the Royal Collections Gallery are the double layer of columns, the geometry, the “chopped” fluidity, and the varying heights of each floor. I incorporated each of these concepts into my design. Using a plan of the double layer of columns, I created a grid that served as the guide for the shape of everything. I created an interesting shape for the buildings by weaving my way through the grid. This is one area where I was also able to tie in the geometry of the Royal Collections Gallery.


Just like the Royal Collections Gallery, my design has no curves, only straight lines and perfect corners. This concept is not just seen in plan view, but also in elevation. The general shape of the building, as well as the more intricate designs incorporated into it all follow the same language when it comes to geometry. I was able to do many different combinations of shapes that kept the idea of straight and crisp lines and angles. With the geometry, I was also able to highlight another main design characteristic of the Royal Collections Gallery. This being its “chopped” fluidity.

What I mean by “chopped” fluidity is seen really well in the Royal Collections Gallery’s elevation. Though it all appears continuous, there are constant breaks in the building (between the columns), that force the outer-most surfaces of the building to unalign with each other. I was able to incorporate this into my design by carving spaces out of my building. Some I simply carved a few inches into the wall, while others I completely dug into the building. I found this to be a unique way to introduce that aspect of the Royal Collections Gallery into my design. With these carvings, I was also able to incorporate the idea of the varying heights shown in the building as well.

The Royal Collections Gallery has several floors that vary in height. This can clearly be seen in the facade of the building. I chose to incorporate this in two ways. The first way was in relation to the carvings. Not all of the carvings are the same size. Some carvings are double the size of others, while others merge into one another. This was an interesting way to incorporate this idea into my design. The second way I incorporated it was simply by making the middle building (the gallery) double the height (on the inside) as the others. I also made the first building on the left (the bookstore) just one floor, but starting on the second floor. The final building (the cafe), has two floors. Each of the buildings has a different relationship when it comes to floors and heights.

The space below the bookstore (left building) is meant to be a space to simply sit down, unwind, or read a book. The second floor also has some spaces inside the store to sit and read. The middle building is the gallery. It is meant to house many paintings of varying sizes, as well as a couple sculptures. The building on the right is the cafe. The idea was that you could order on the ground floor, and either sit there, outside, or on the second floor where there is additional seating to enjoy your coffee and/or pastry.


I wanted the design of the courtyard to be simple but to still tie in to everything. I was able to create an interesting design where it appears that everything in the courtyard is getting even more pixelated, as it gets further from the building, almost as if it were being pulled out of it. This kept the idea of the grid and tied in some other key spaces, such as additional seating, some greenery, and some small ponds as well. My design of both the building and the courtyard was an interesting take on all of the main design concepts of the Royal Collections Gallery, creating a geometric, “carved out” building with an open and spacious courtyard, all on a simple double layered column grid.

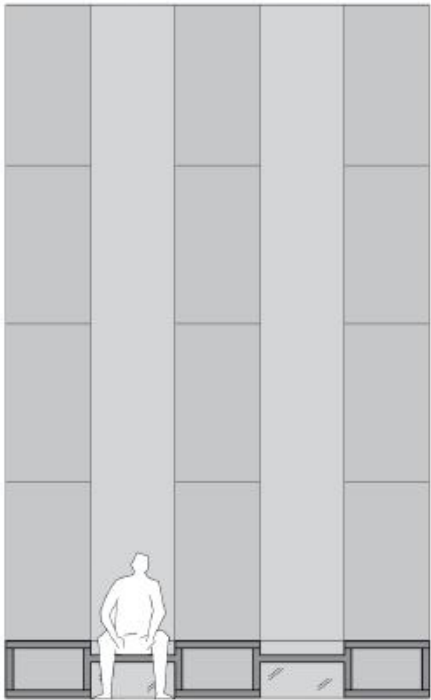


BENCH



REFERENCE PHOTO + SECTION TRANSFORMATION DRAWINGS
(3 PROGRAMS / EXERCISE 02)

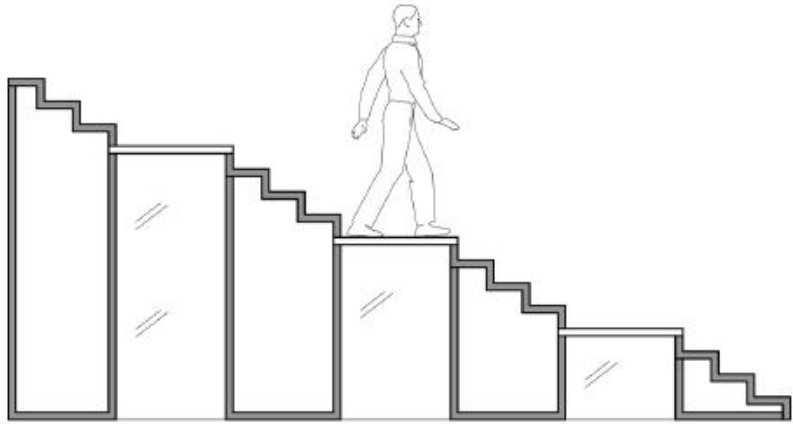


STAIR

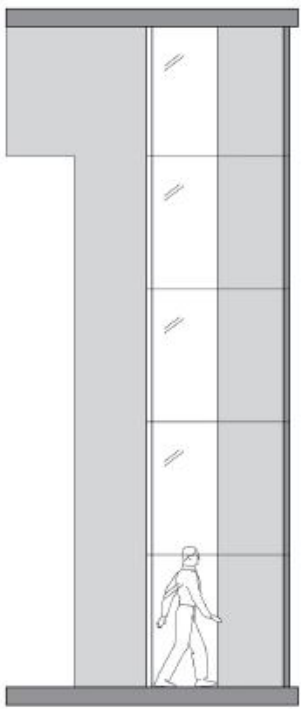

HIDDEN ROOM


SITE ELEVATION (FROM STREET)

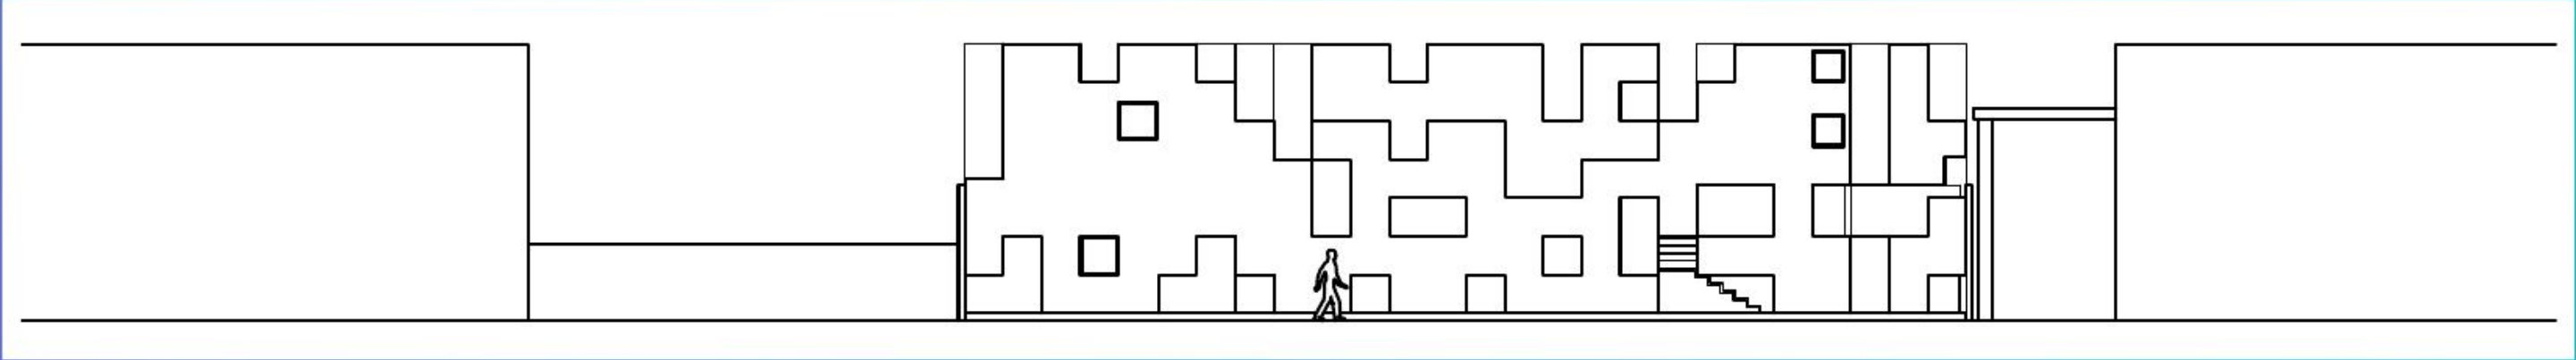

INTERIOR COURTYARD ELEVATION (FROM COURTYARD)




SITE AXON

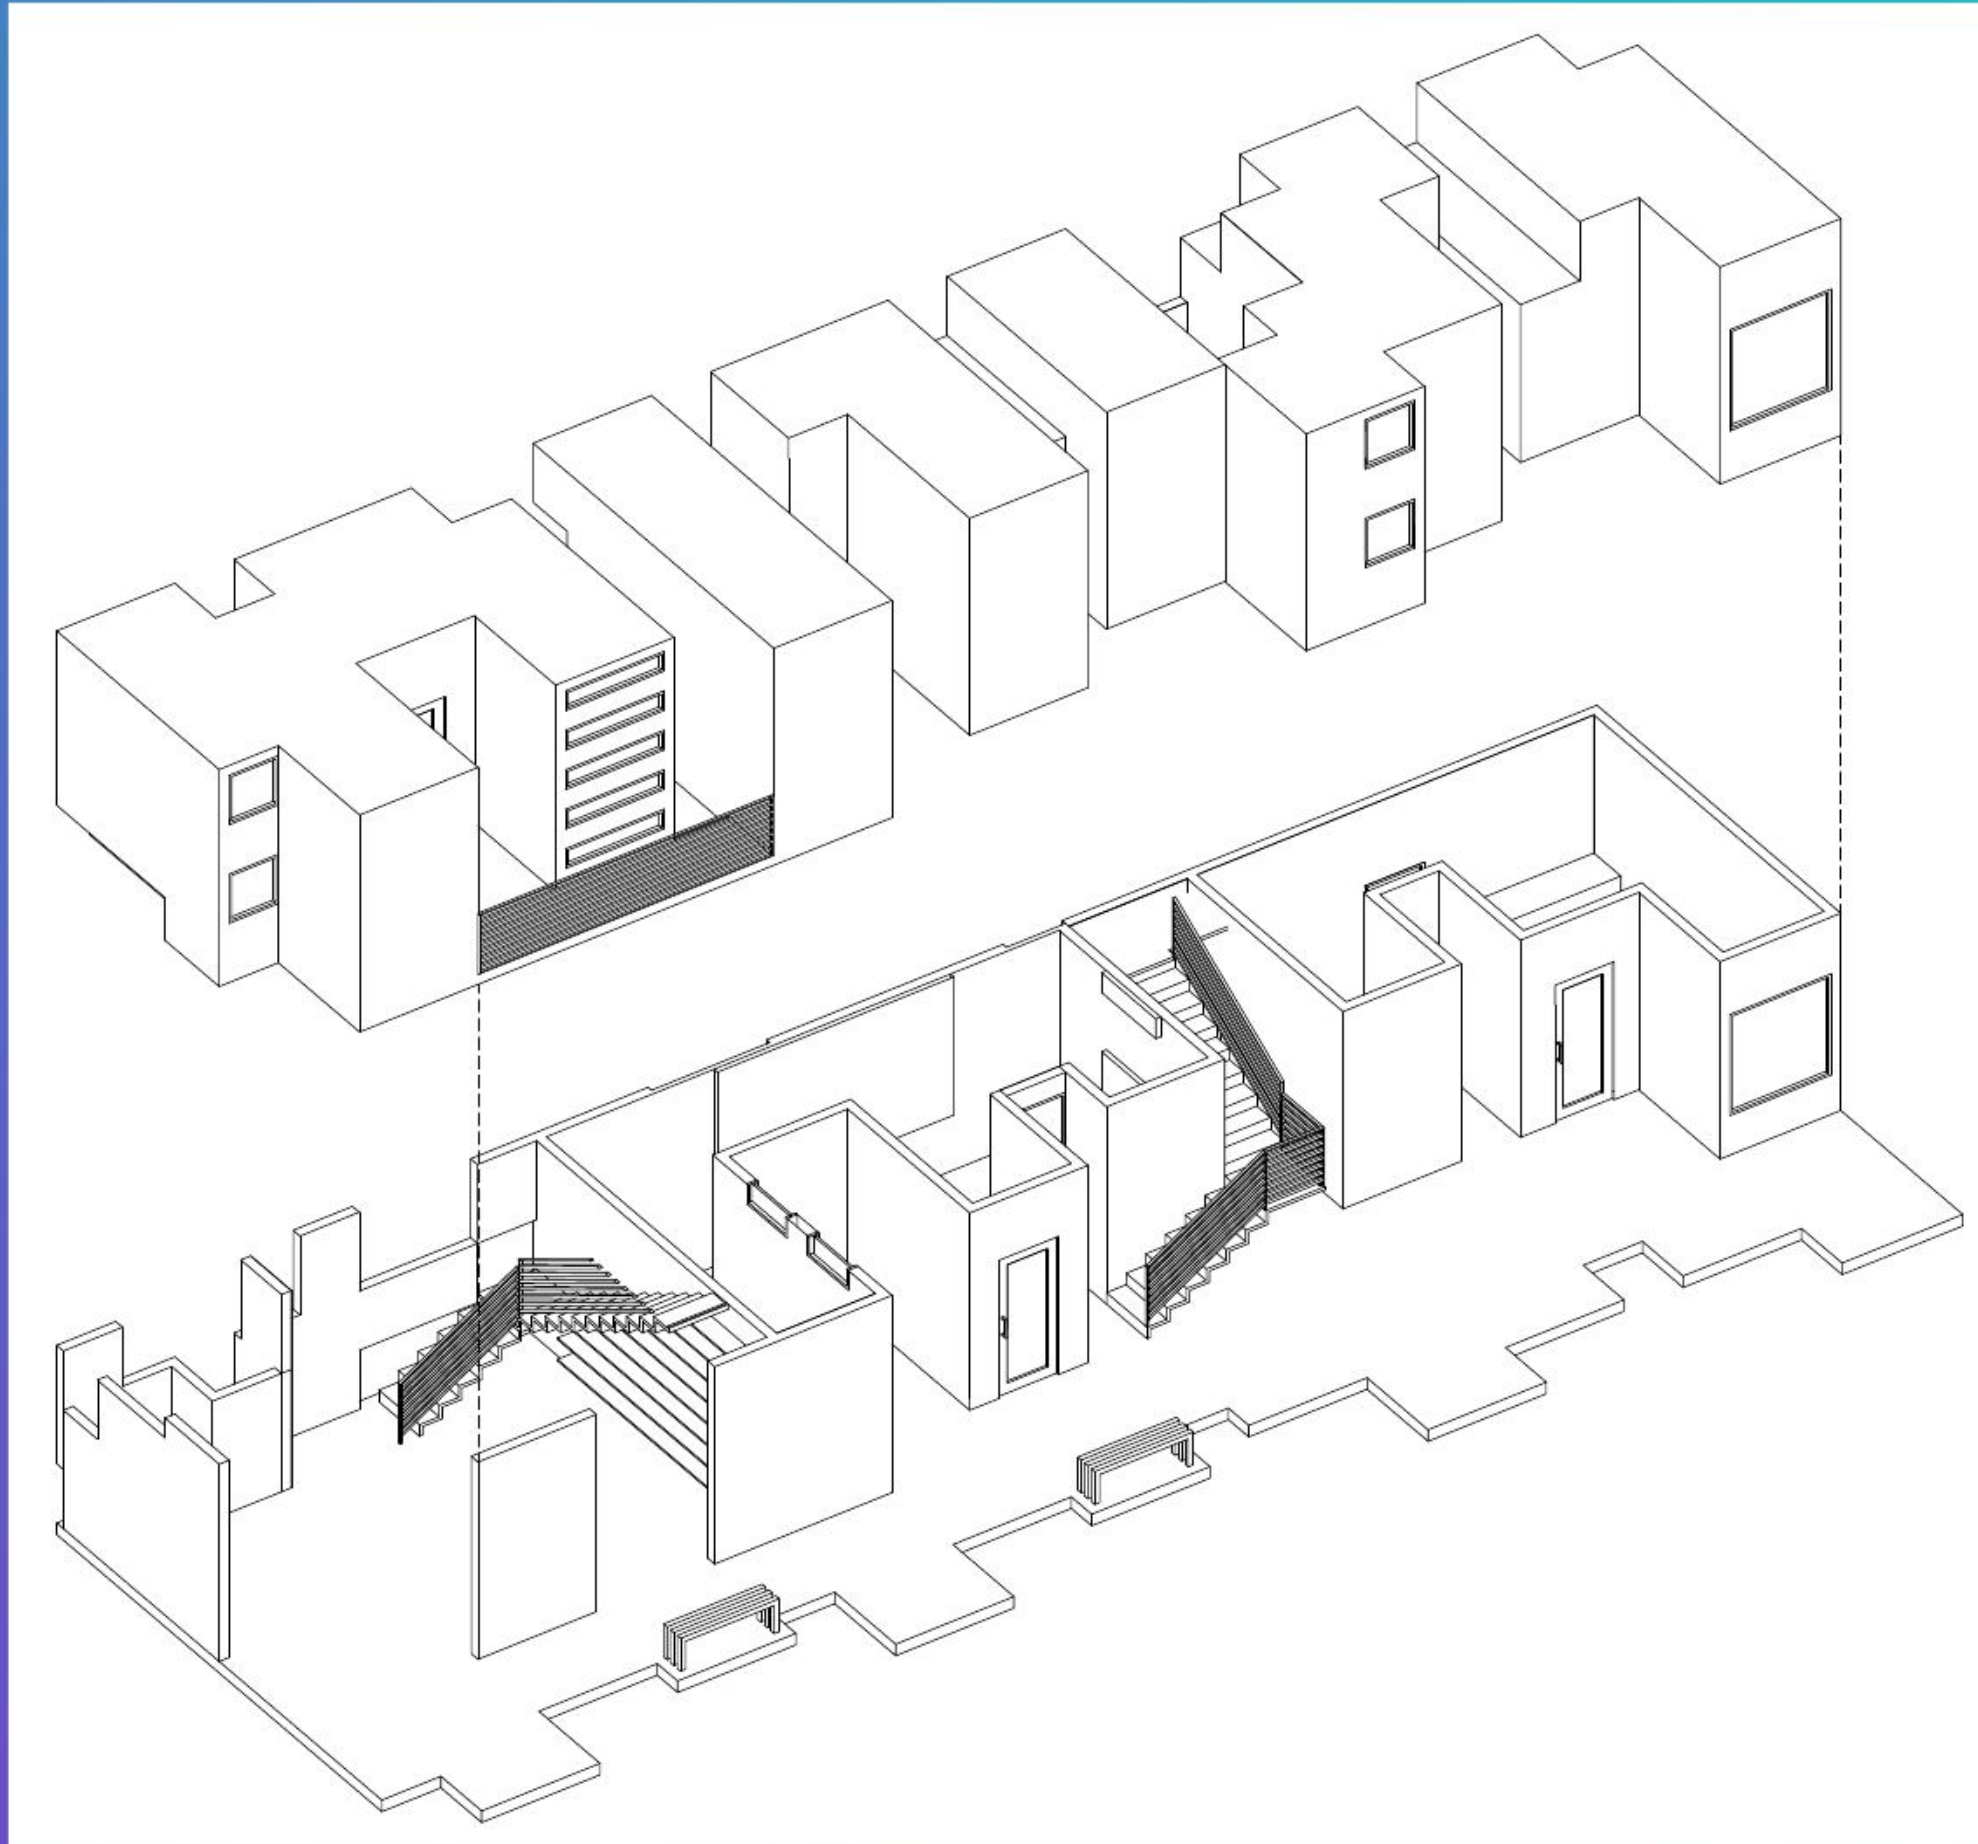



GROUND FLOOR PLAN/ COURTYARD PLAN



SECOND FLOOR PLAN

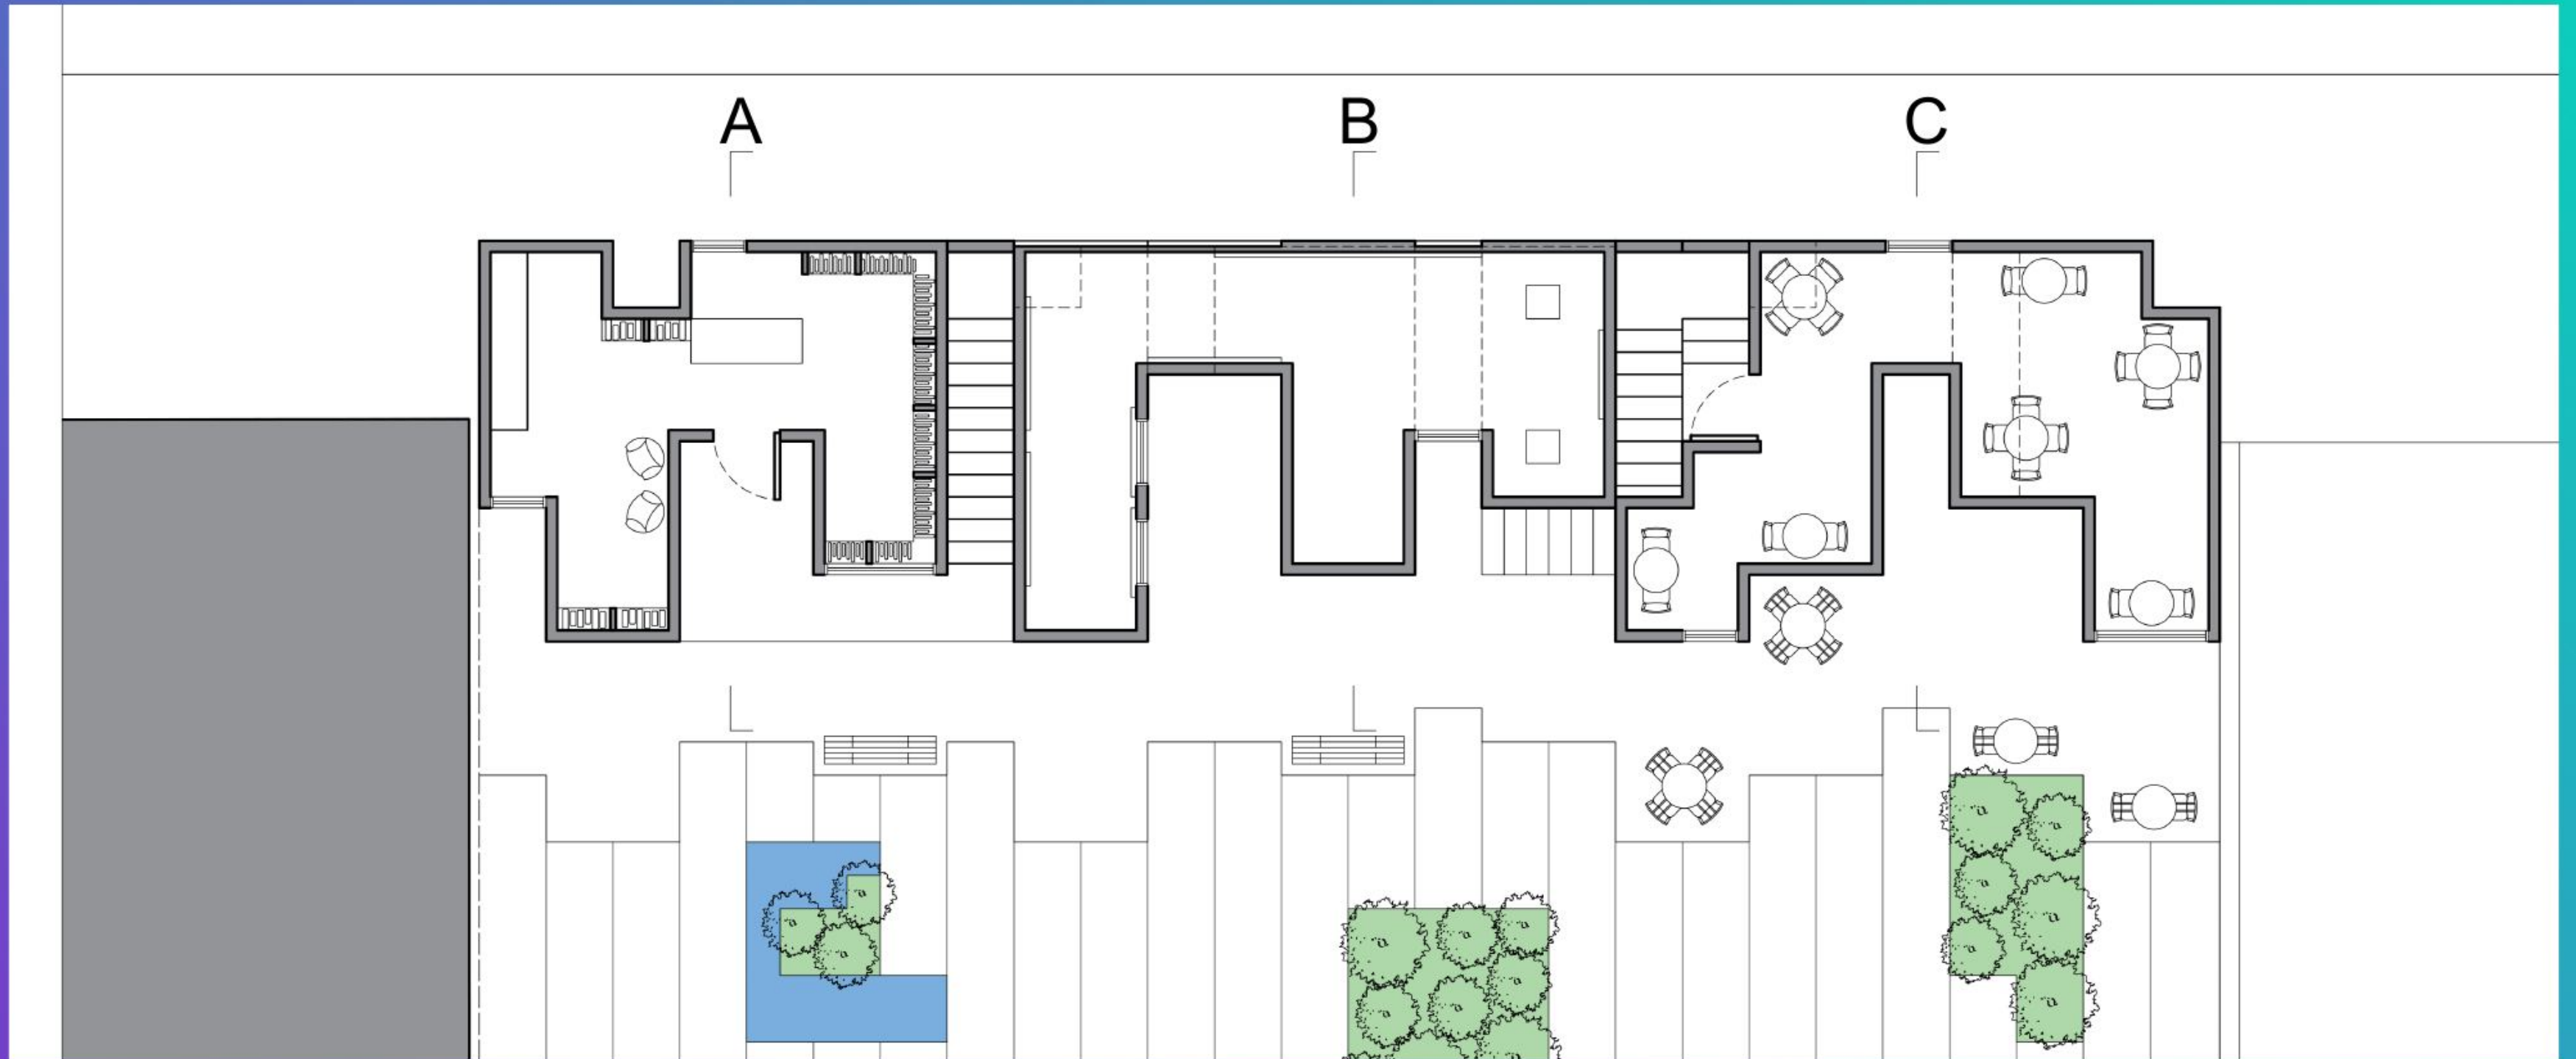


DETAILED CROSS SECTION A

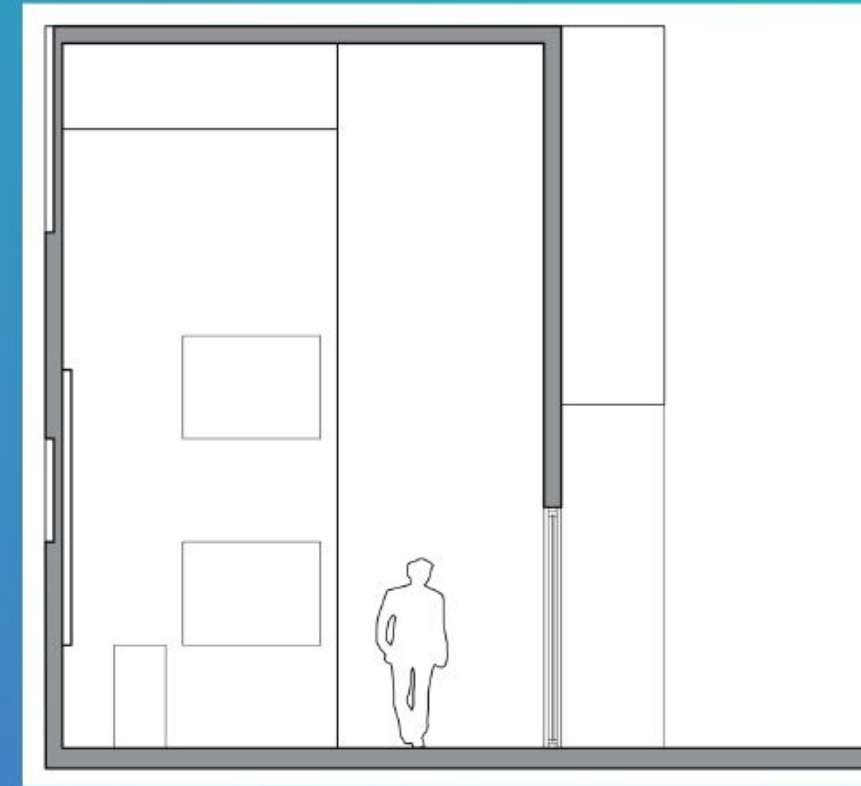
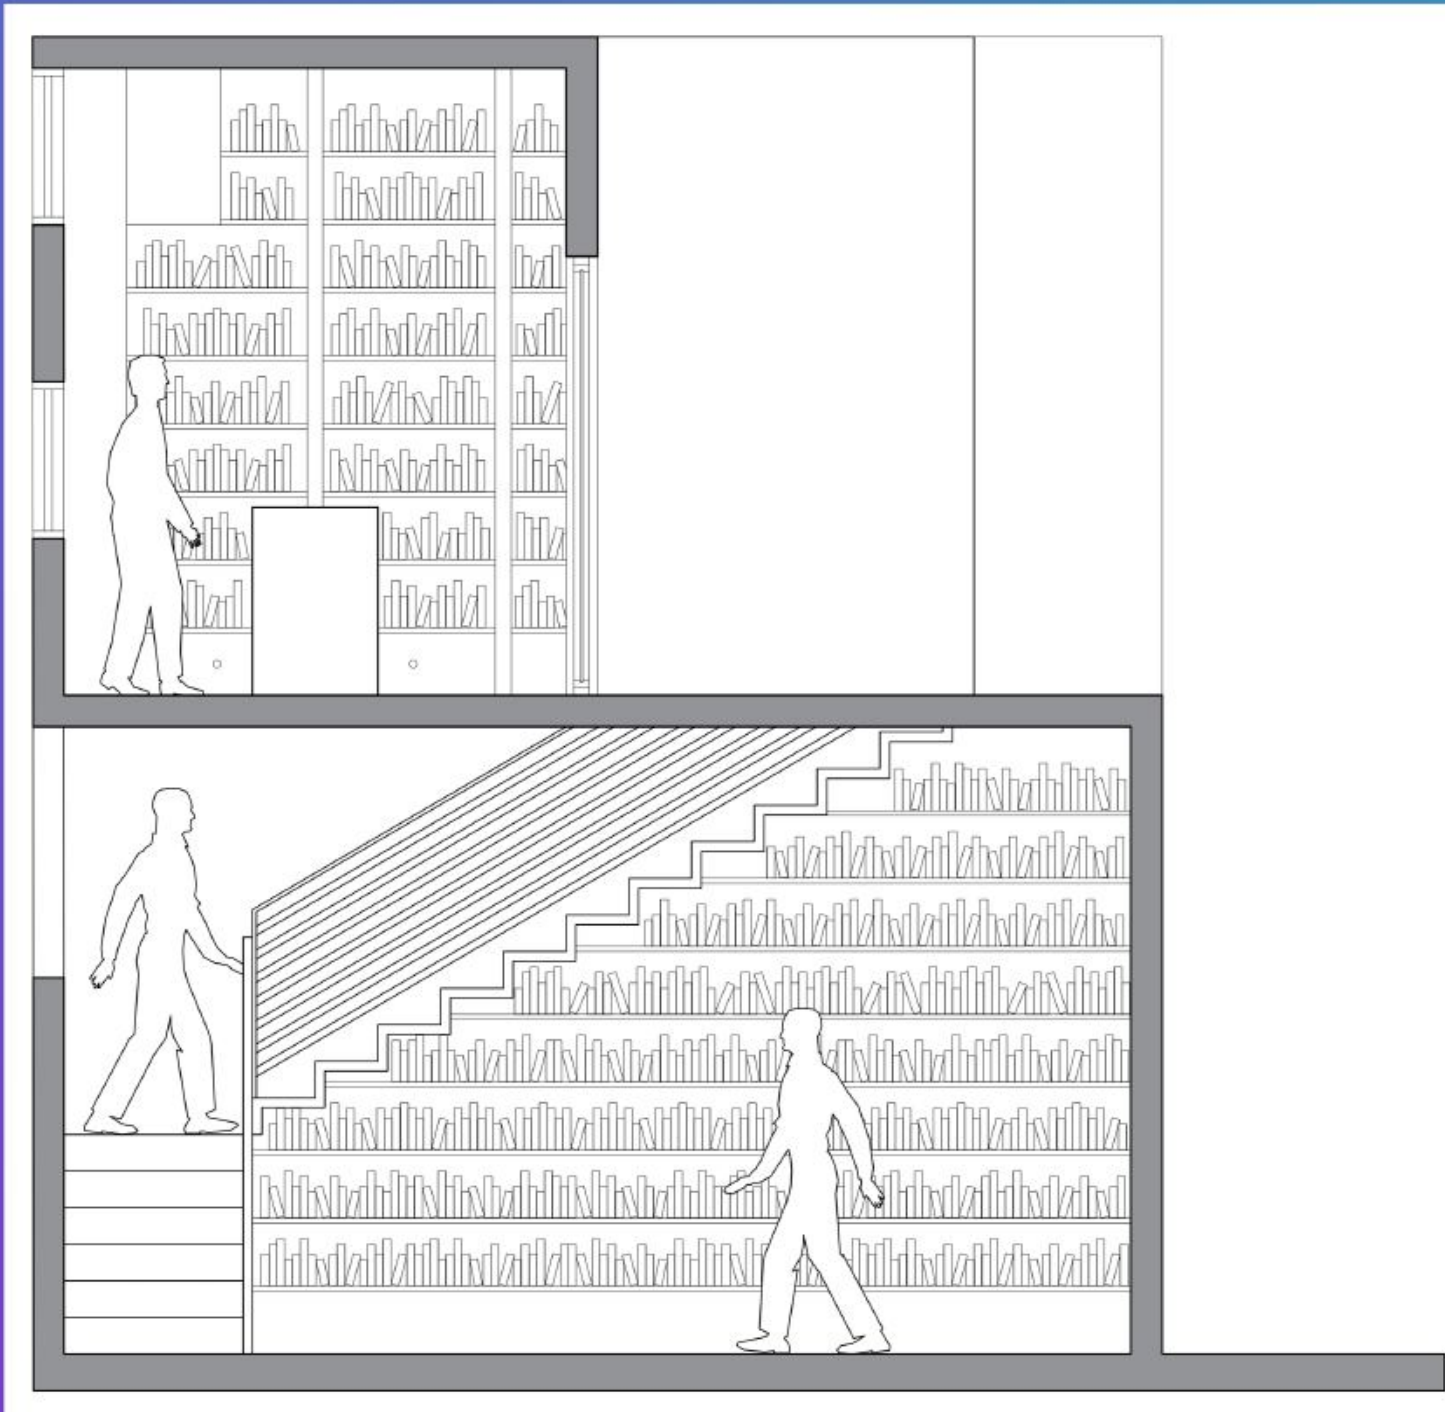


DETAILED CROSS SECTION B


DETAILED CROSS SECTION C

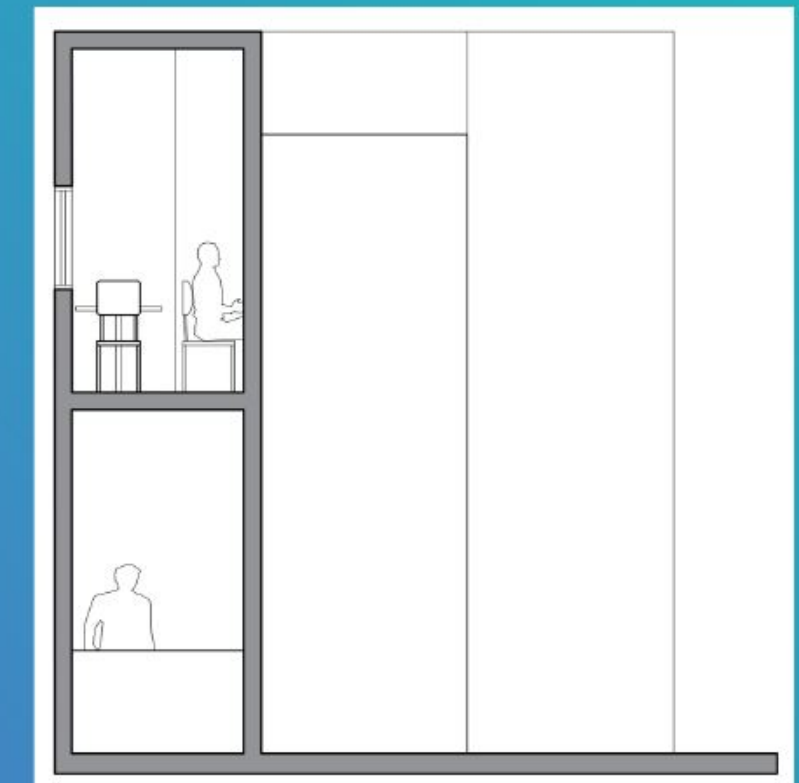

RENDERING EXTERIOR (FROM INSIDE COURTYARD)

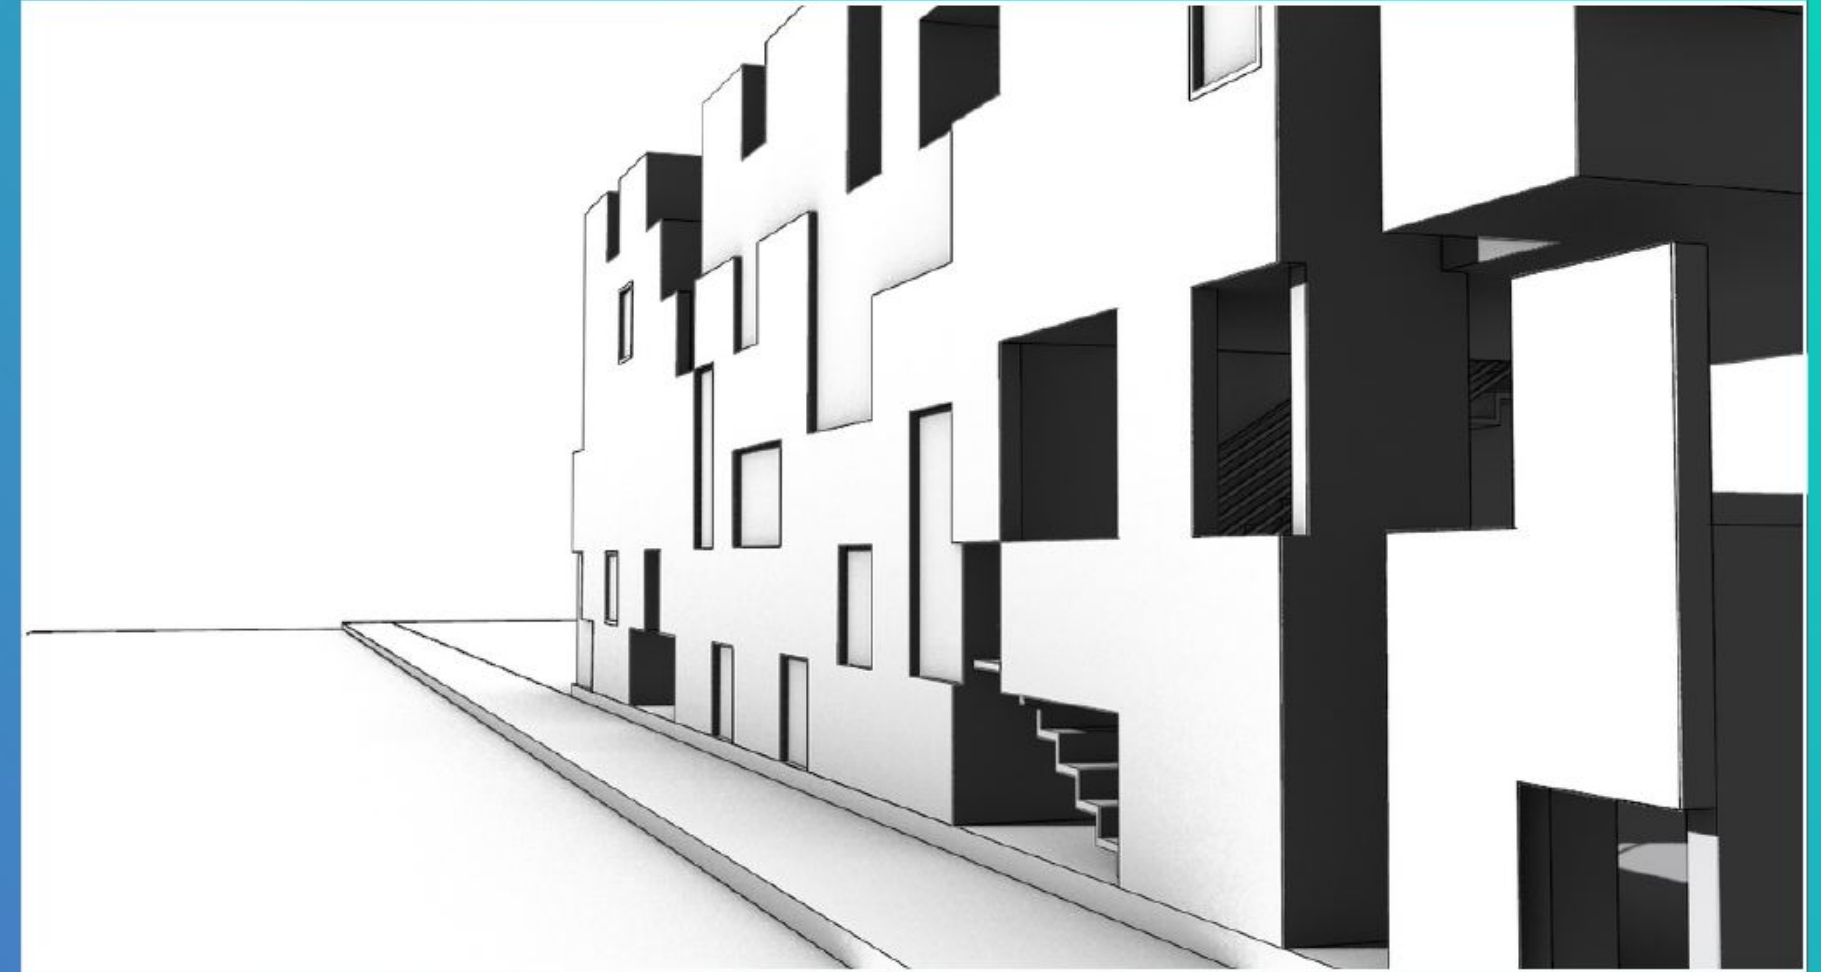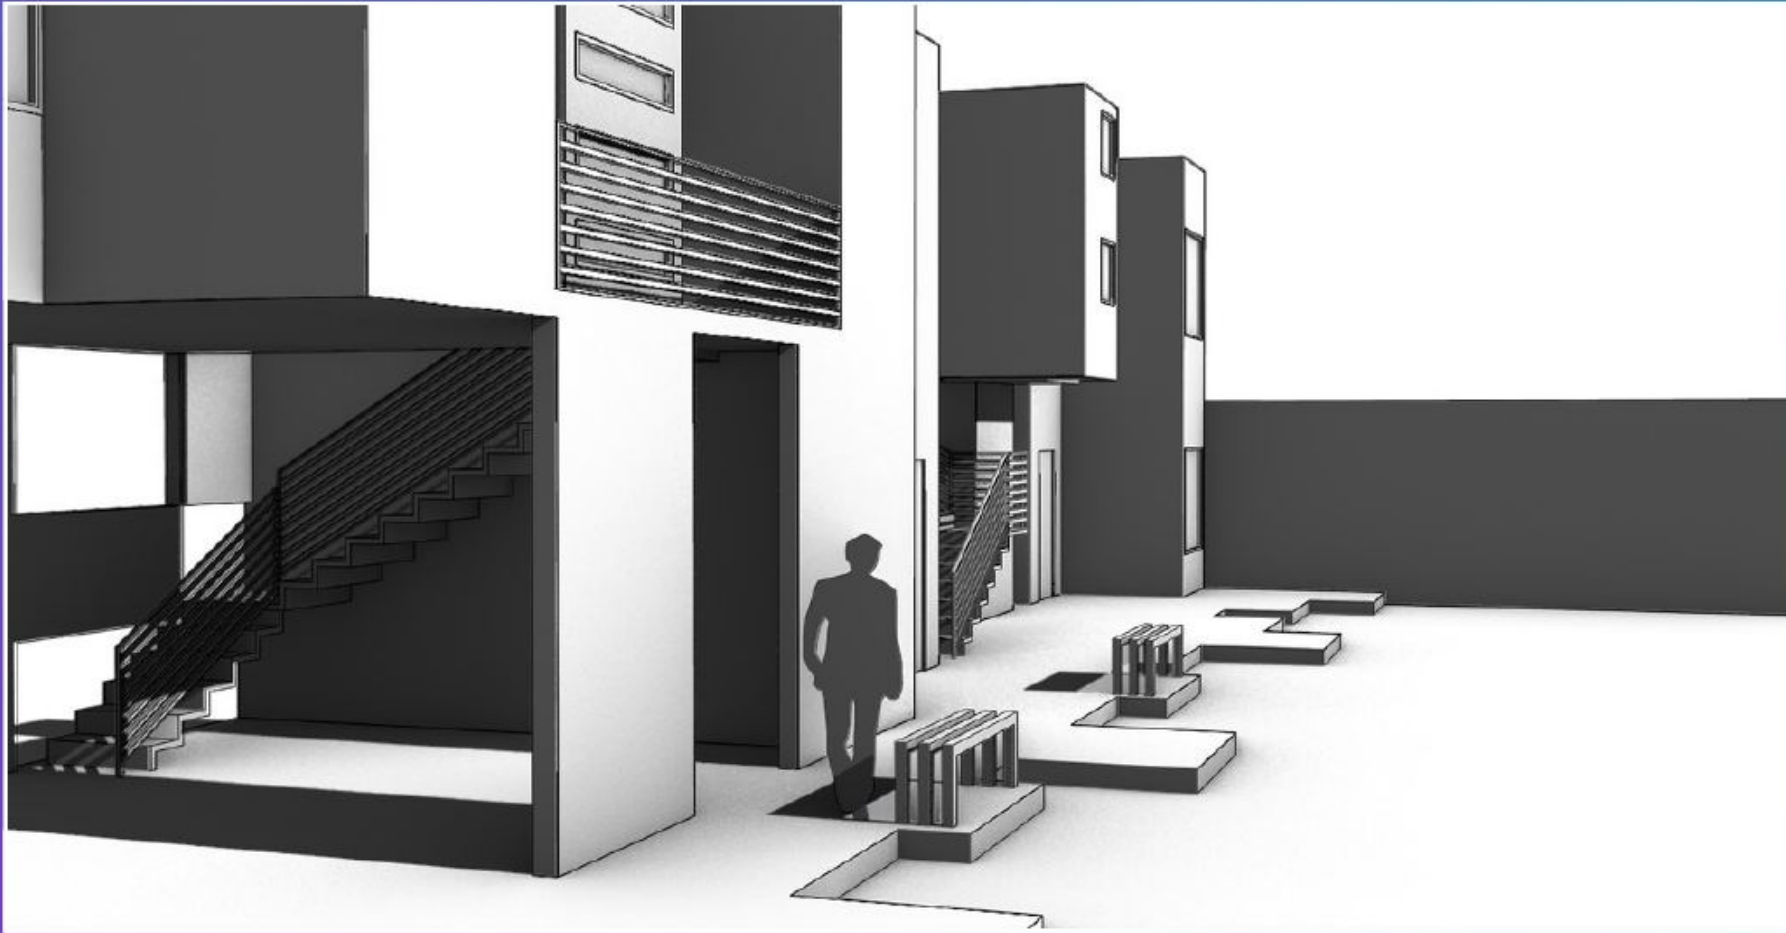


RENDERING EXTERIOR (FROM STREET)

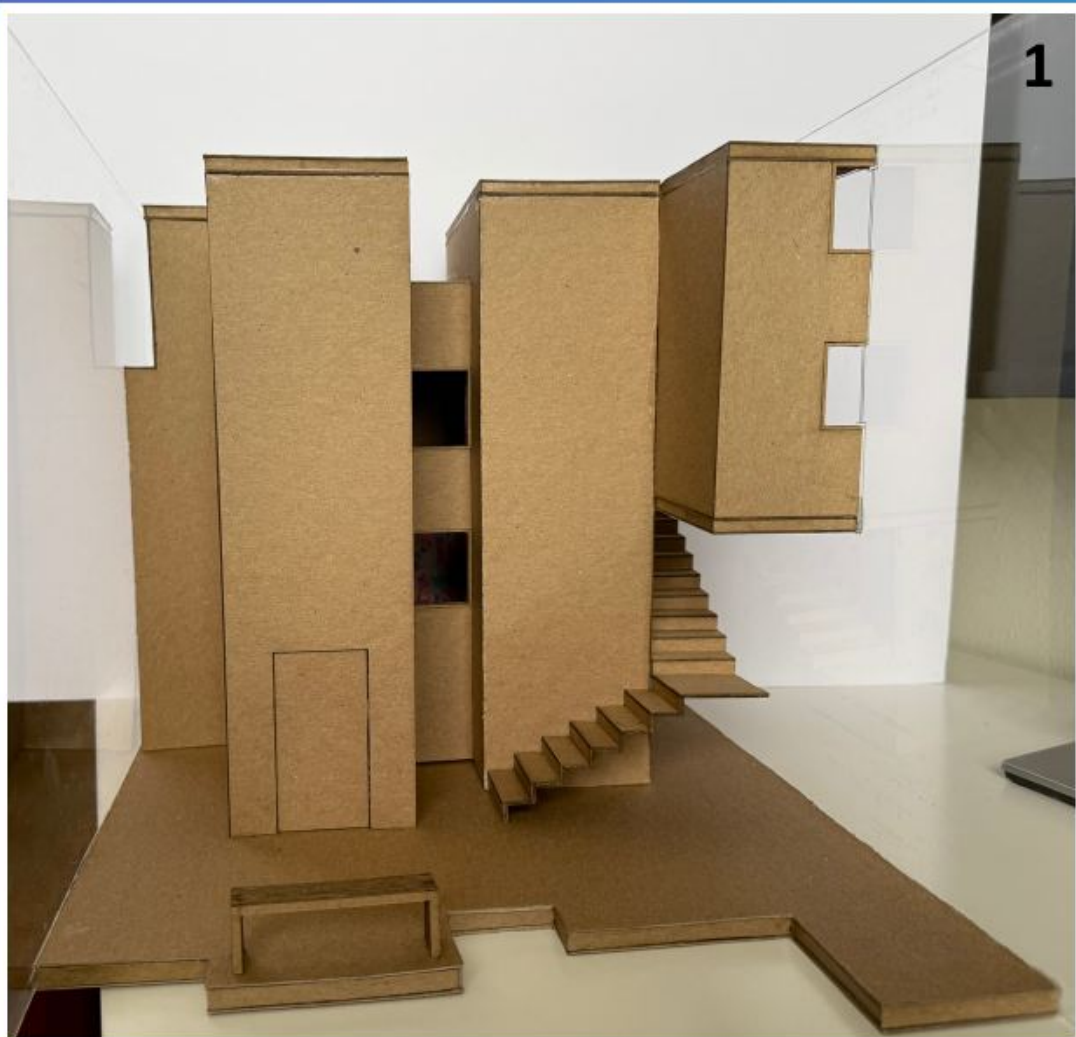


1

SECTION MODEL & SITE MODEL

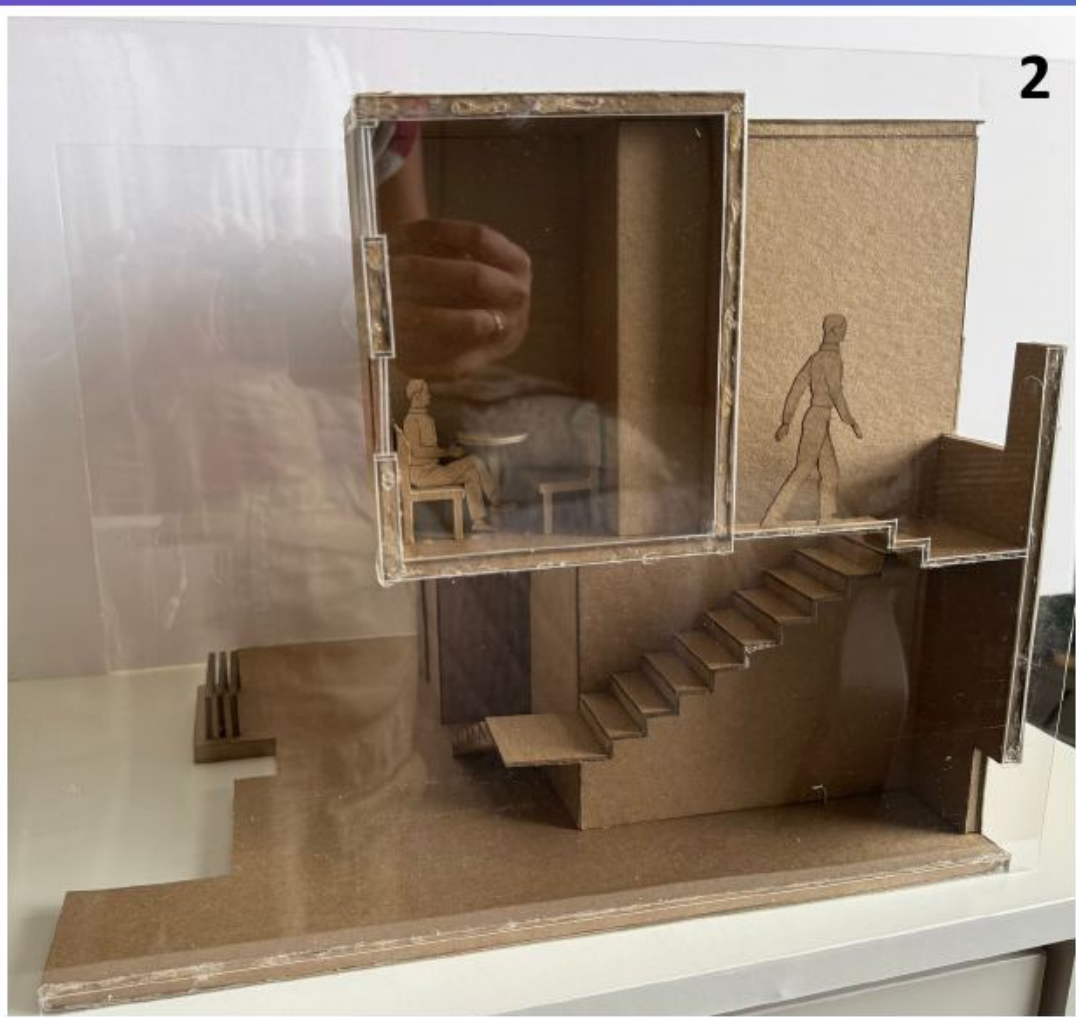


2

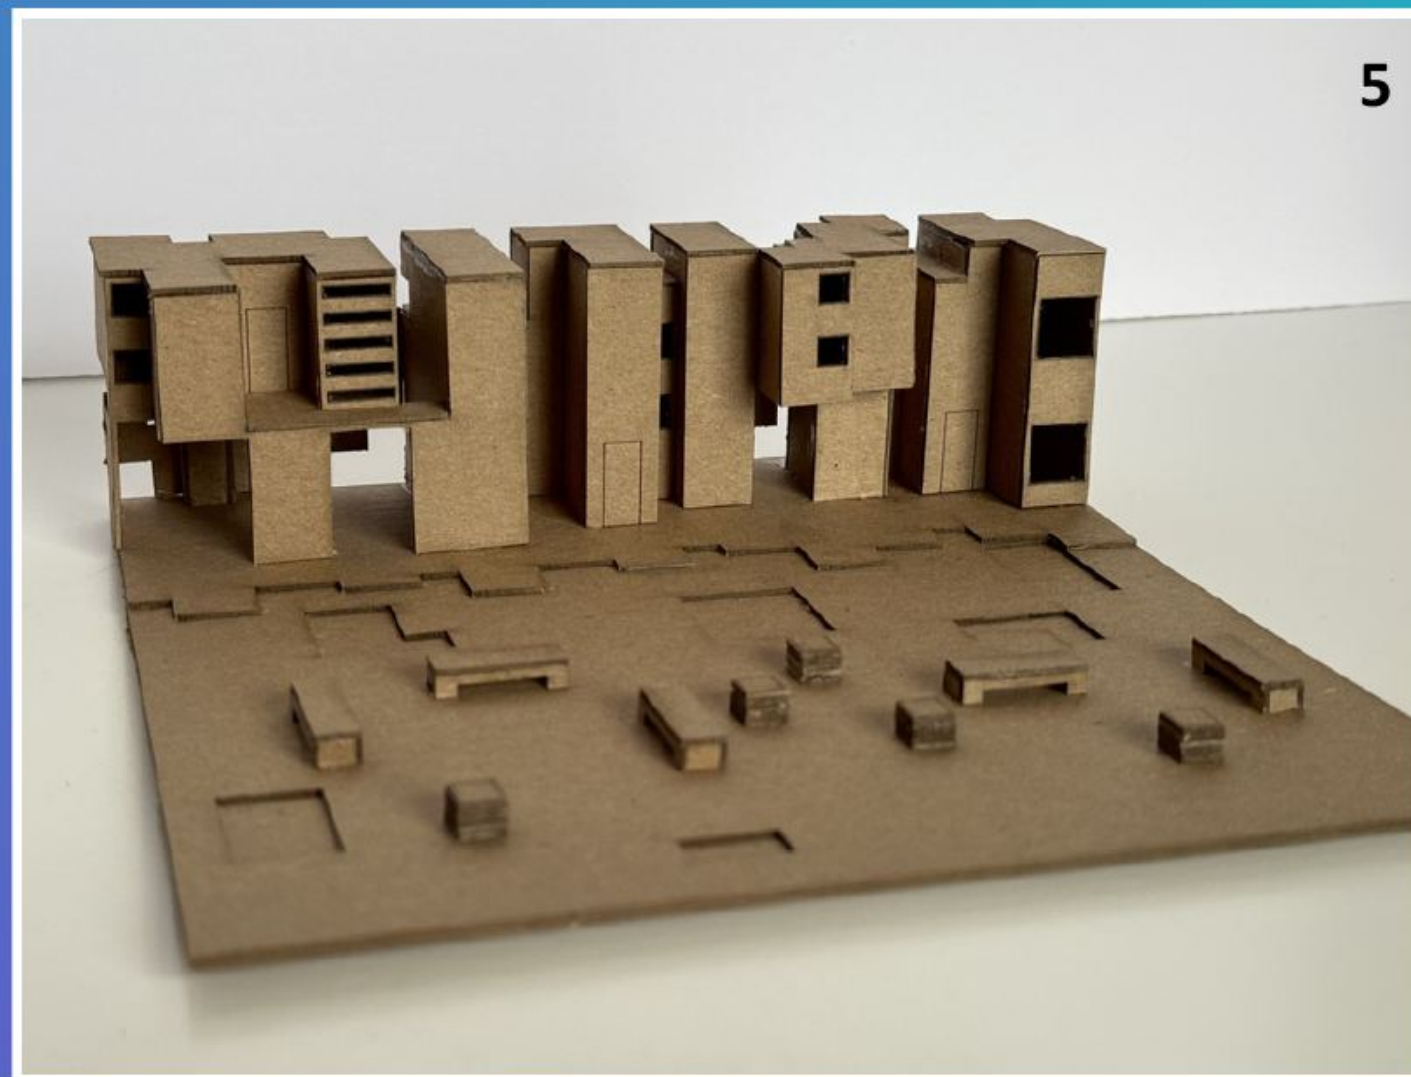


5

MODEL IN IMAGES #1-4: SECTION MODEL
MODEL IN IMAGE #5: SITE MODEL

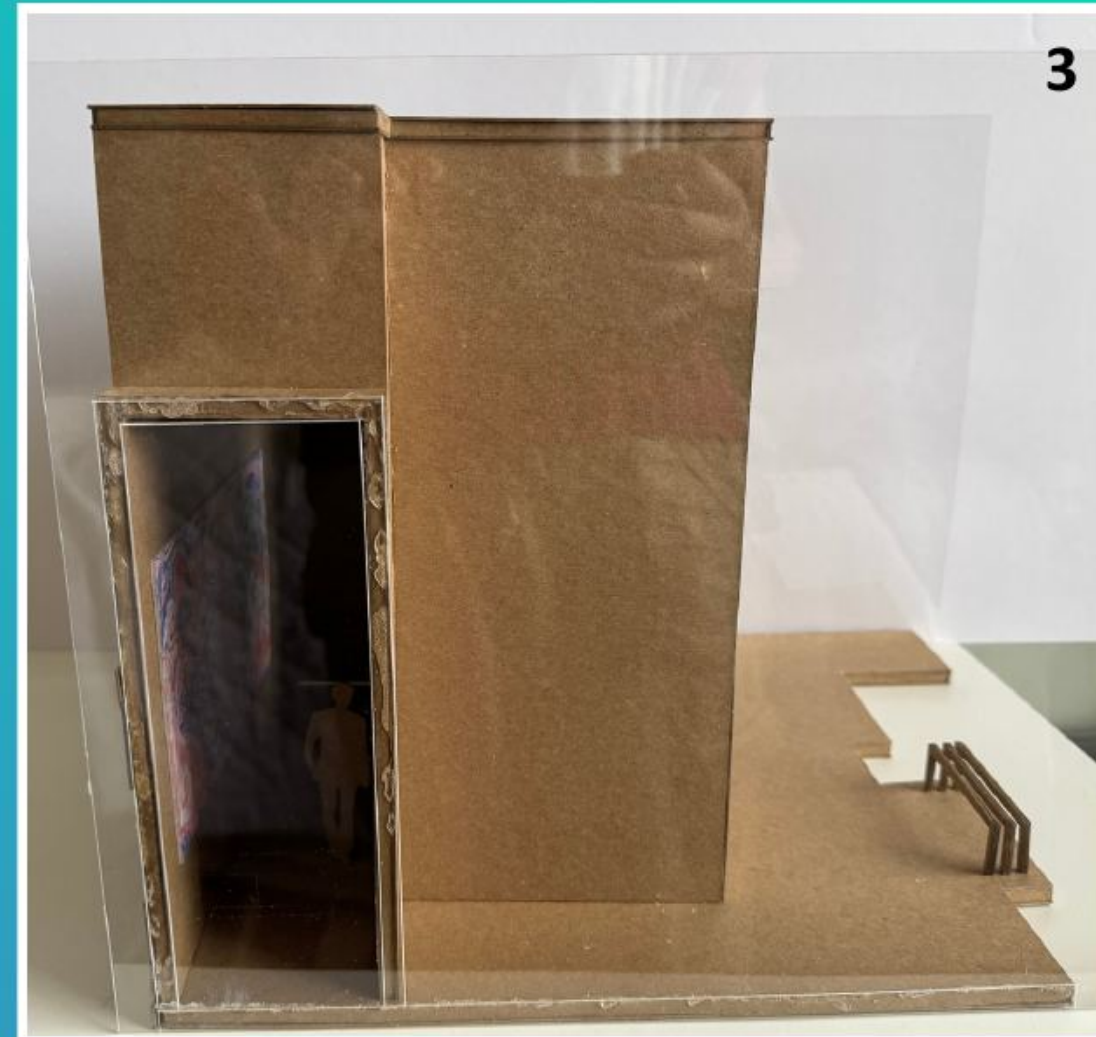

3

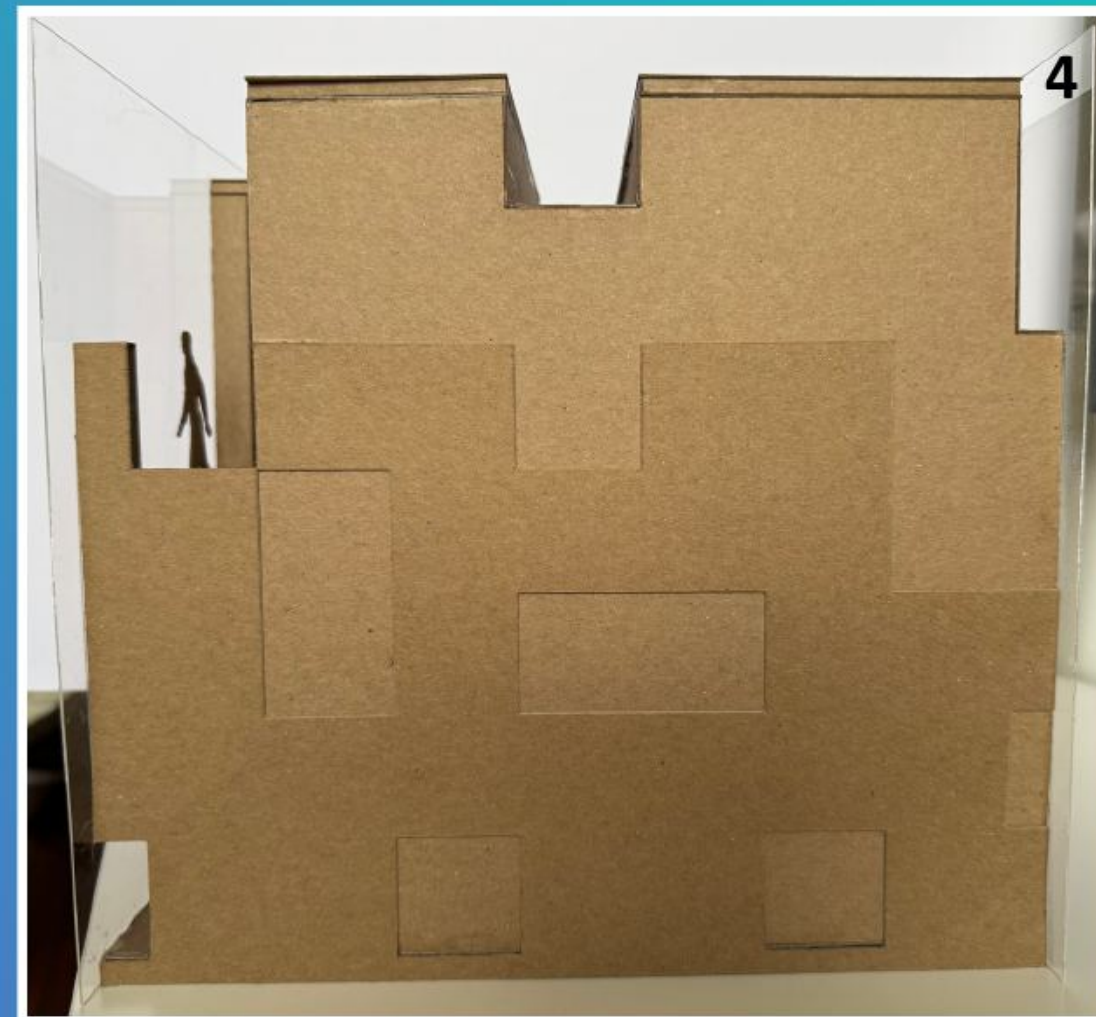

4



PROJECT - 02


LINCOLN ROAD FOLLY ADDITION

The task was to design a small pavilion that would be located at the eastern end of the Lincoln Road pedestrian mall in Miami Beach. Within the pavilion, there needed to be a shaded area with integrated seating, a small place to wash one's feet and integrated planters. The assignment also called for the design of the rest of that section of Lincoln Road, with different elevations throughout. The design also had to reference a previous project where the task was to turn a painting into a 3D object.



SITE PLAN AND SECTION



PAVILION PLAN

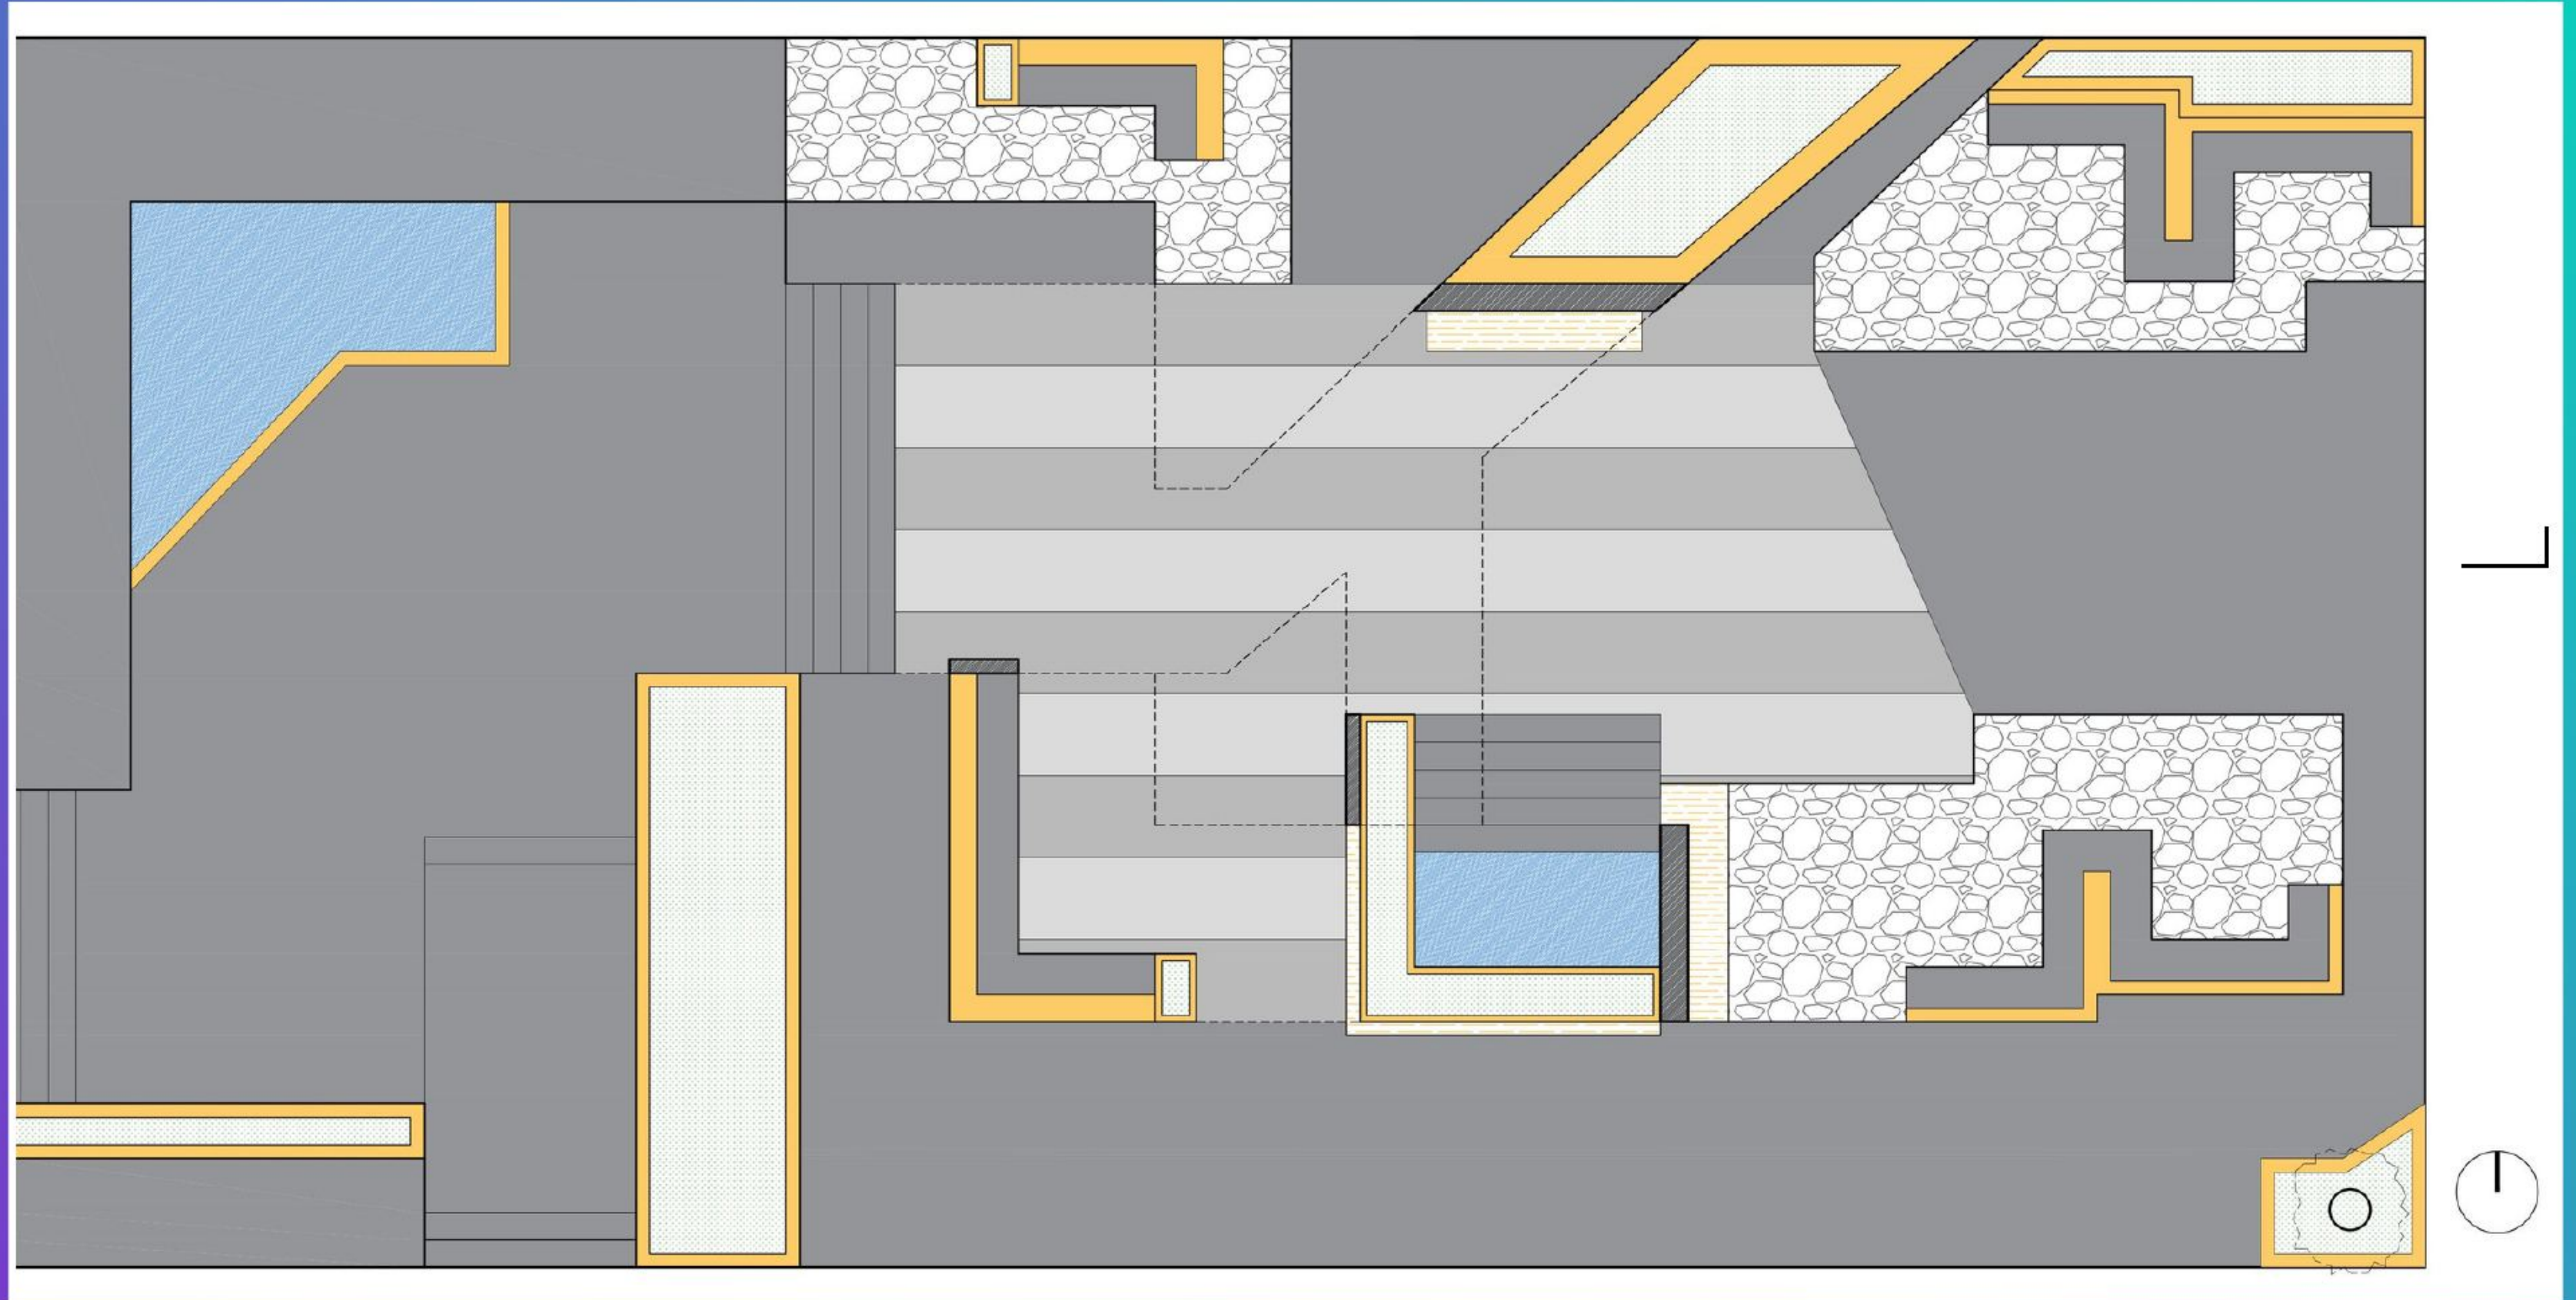

LONGITUDINAL AND TRANSVERSE SECTIONS

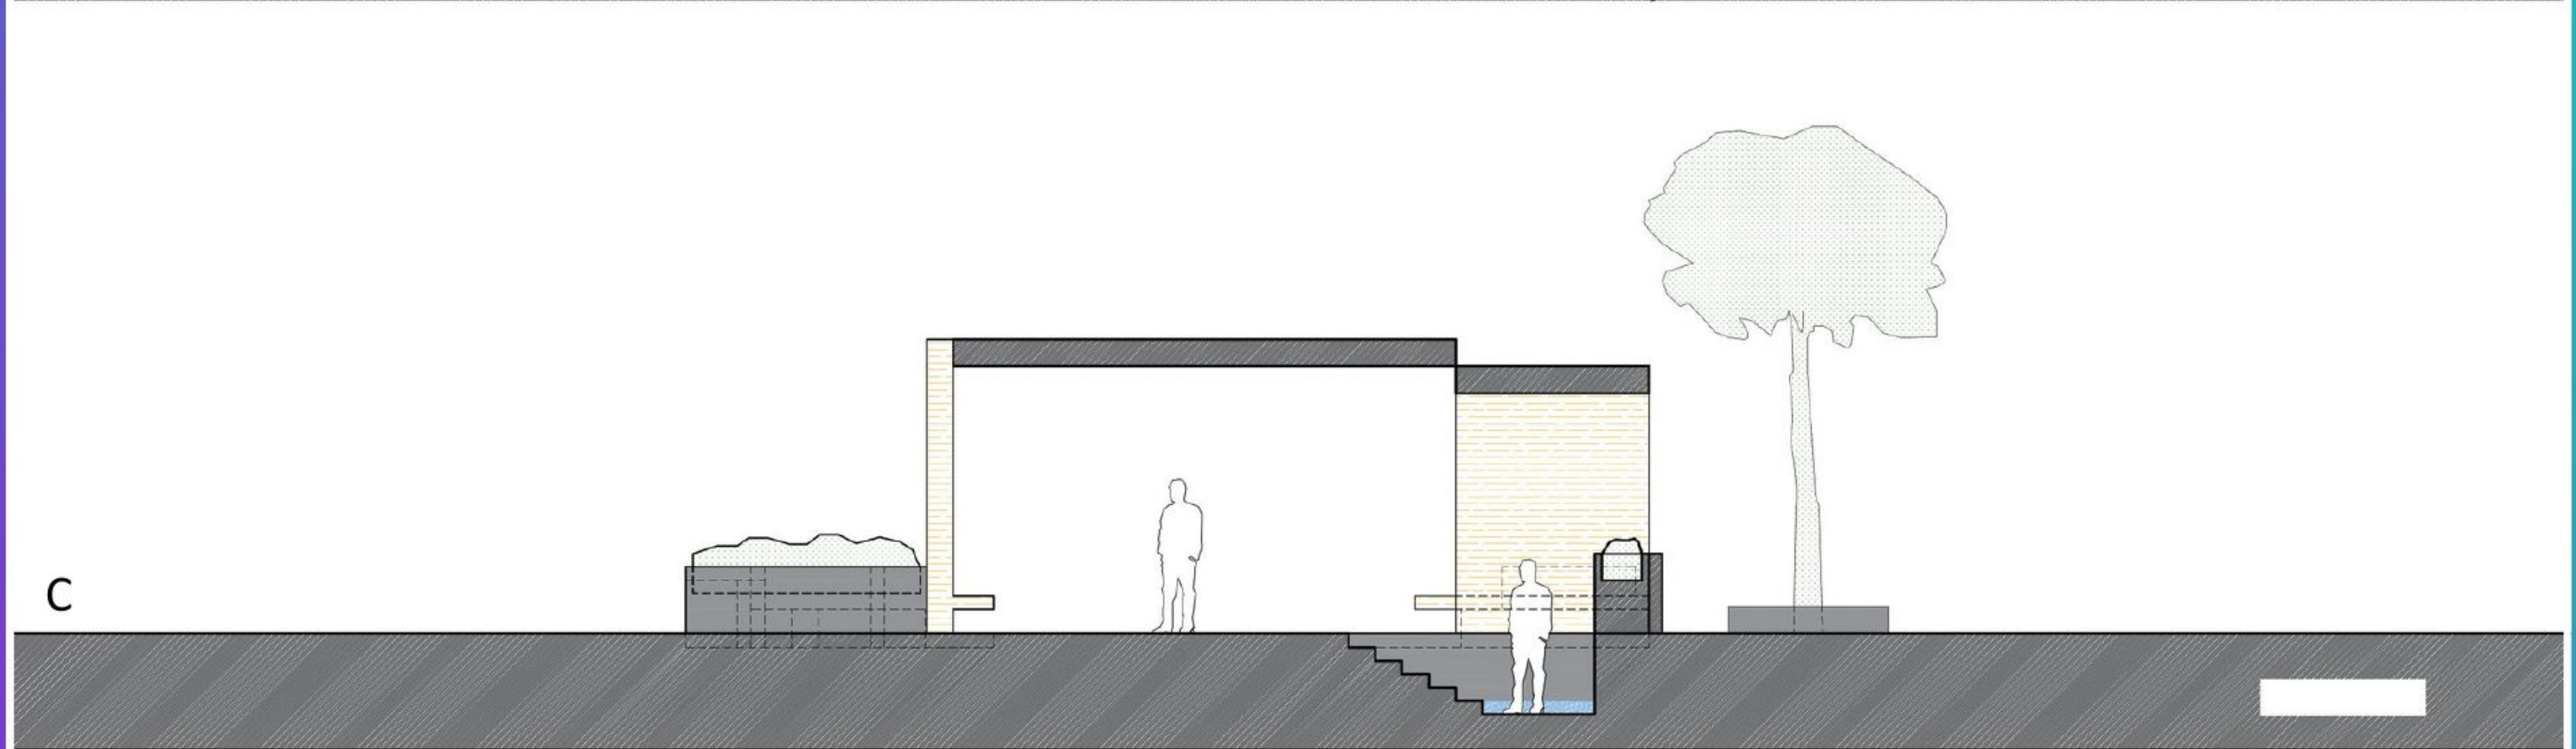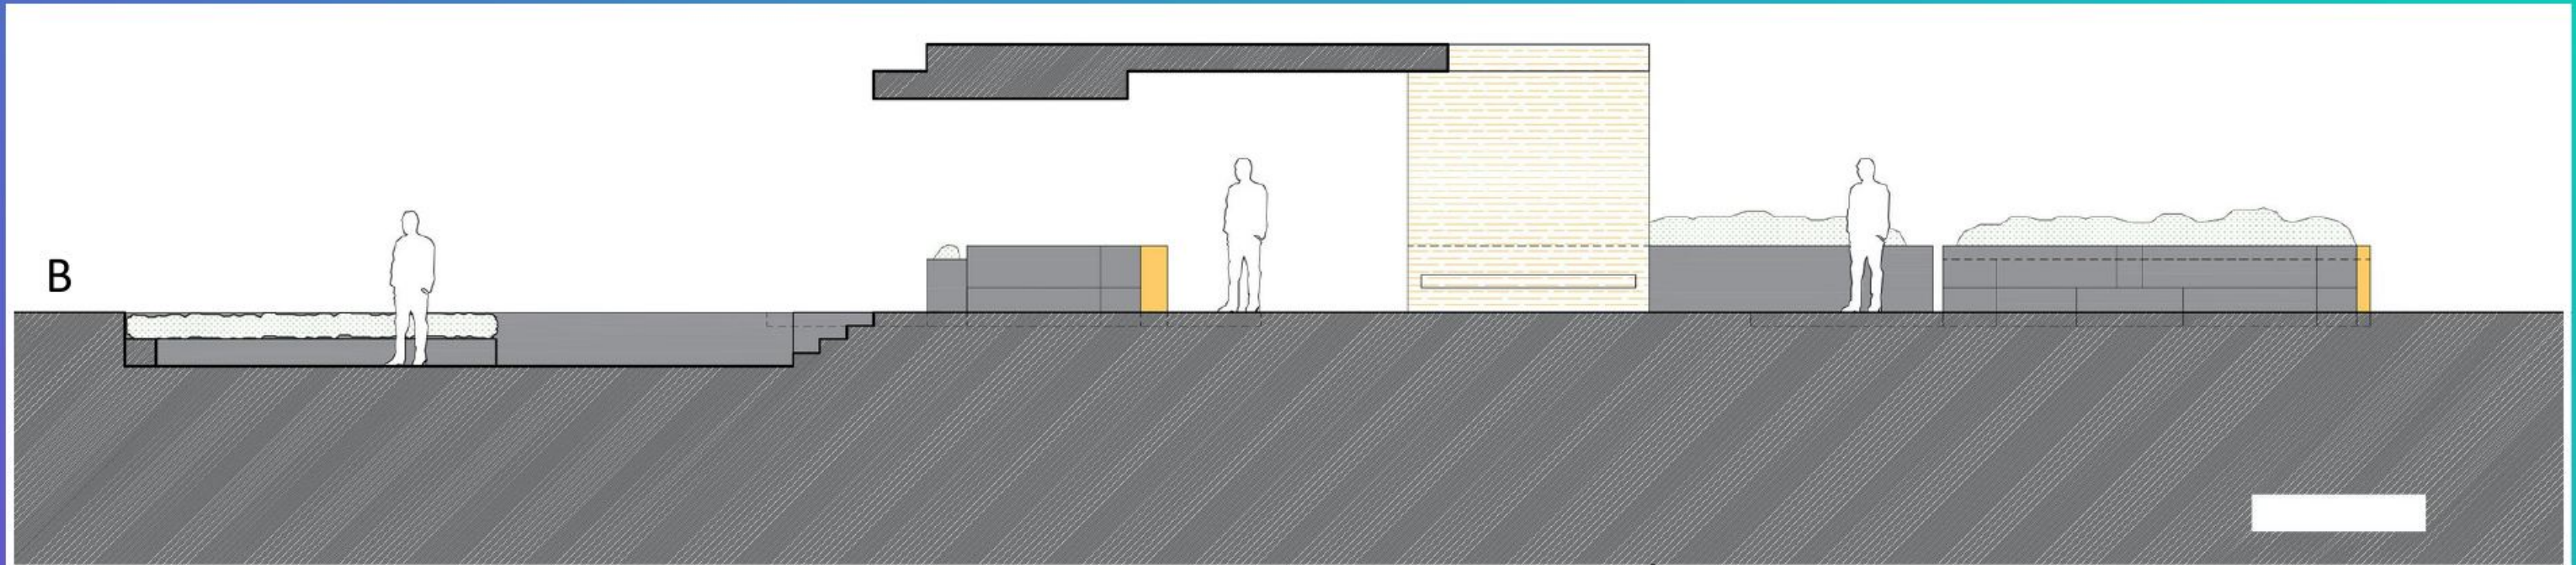


ISOs








MODEL 1 & PROGRESS MODELS

MODEL IN IMAGES #1-3: SITE MODEL
MODEL IN IMAGE #4: PROGRESS MODELS

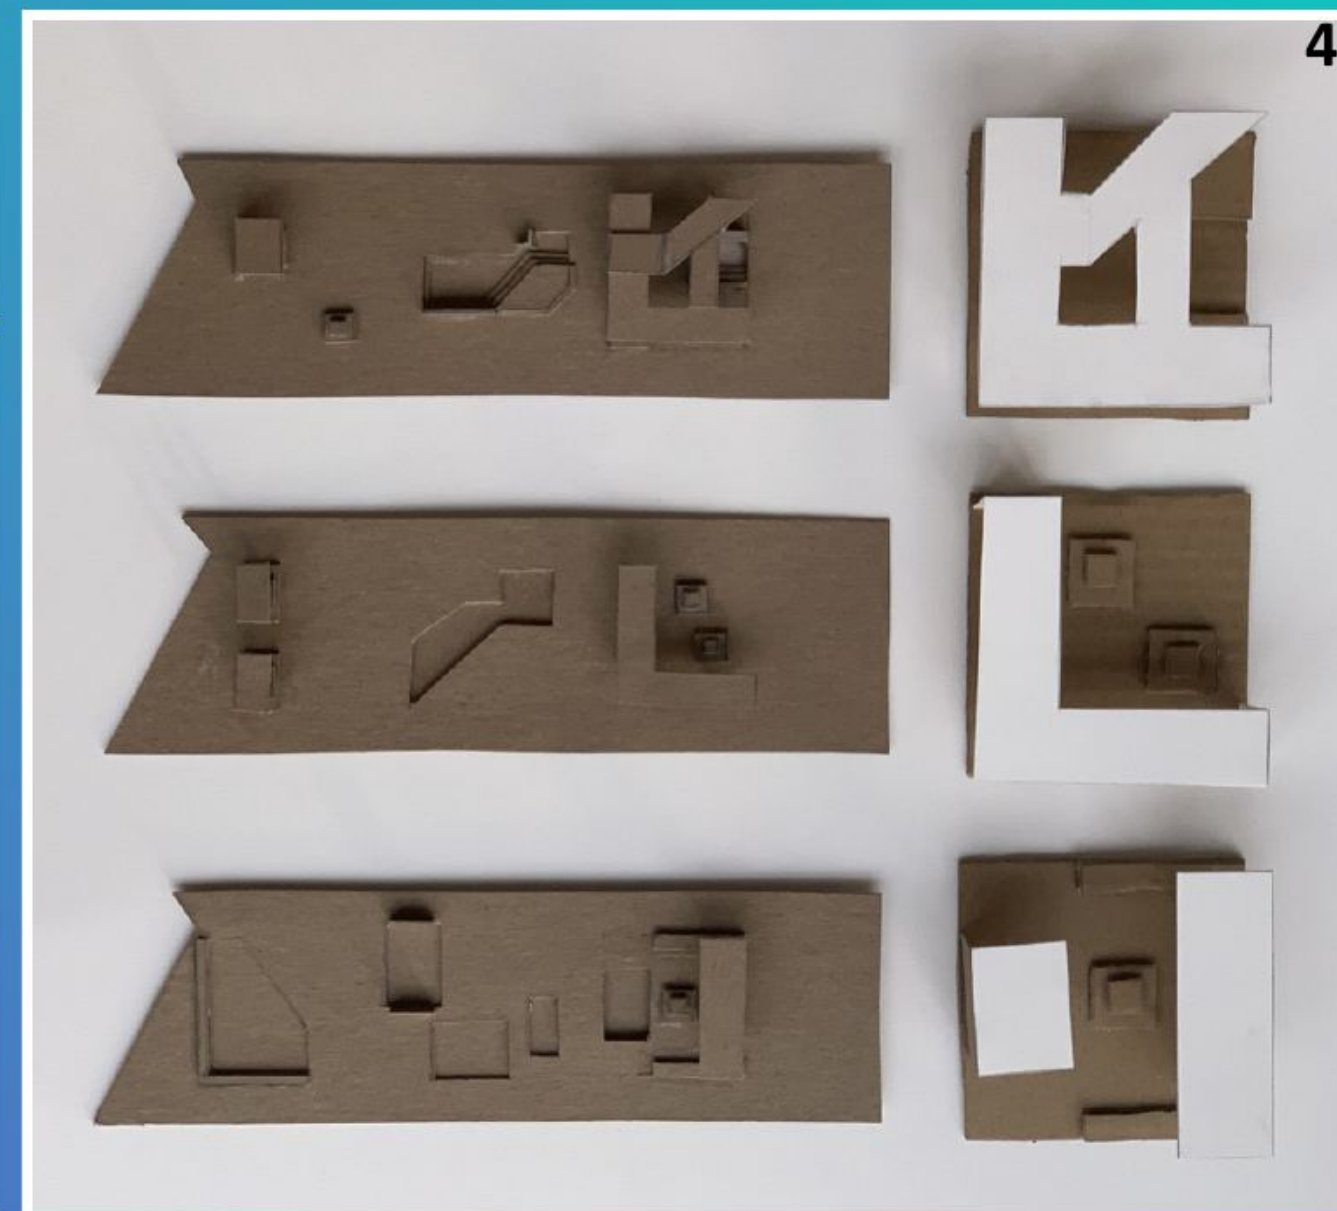

PAVILION MODEL & DESIGN REFERENCE

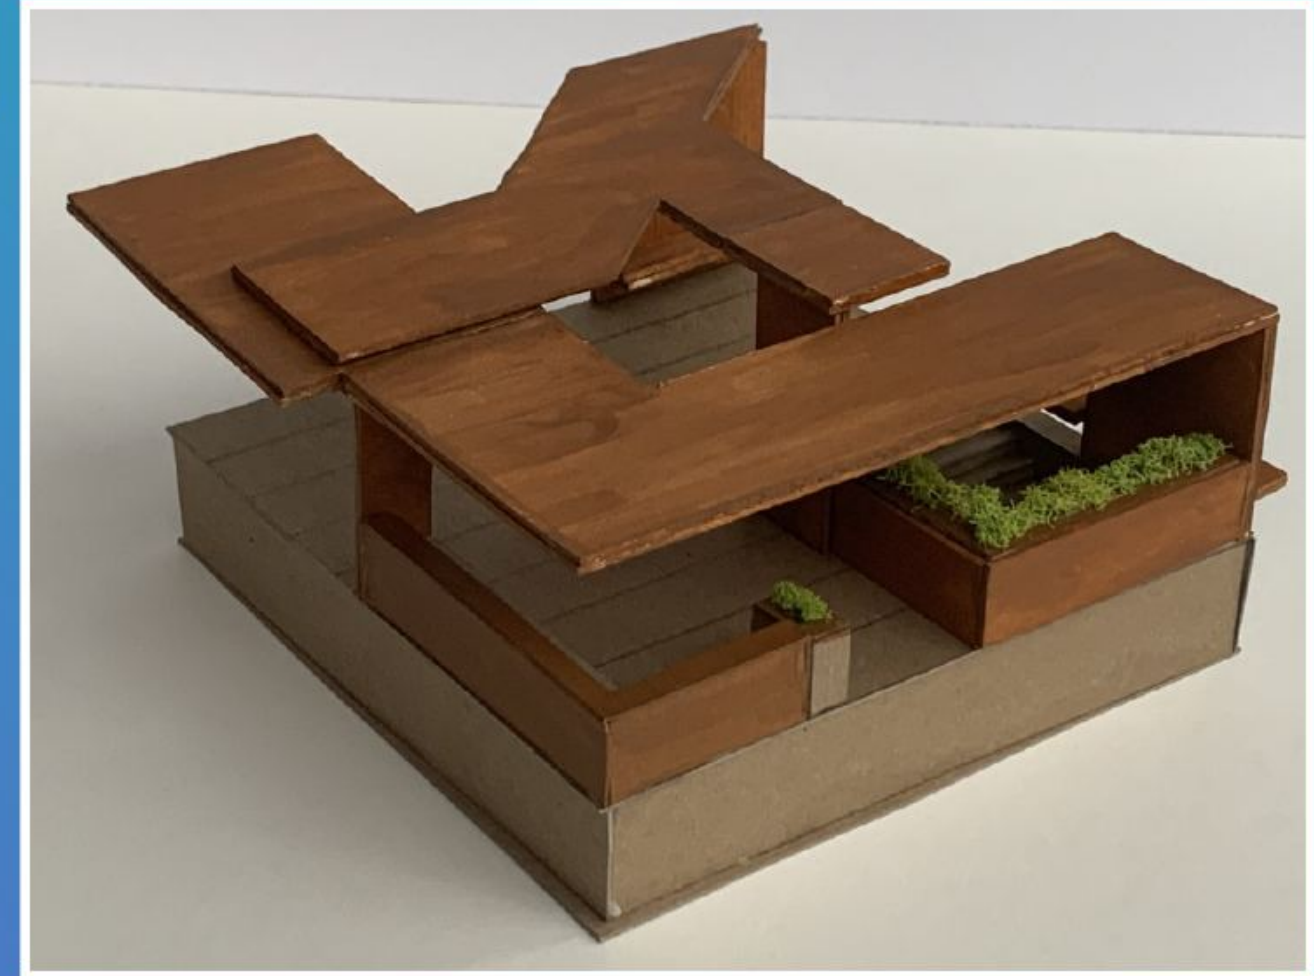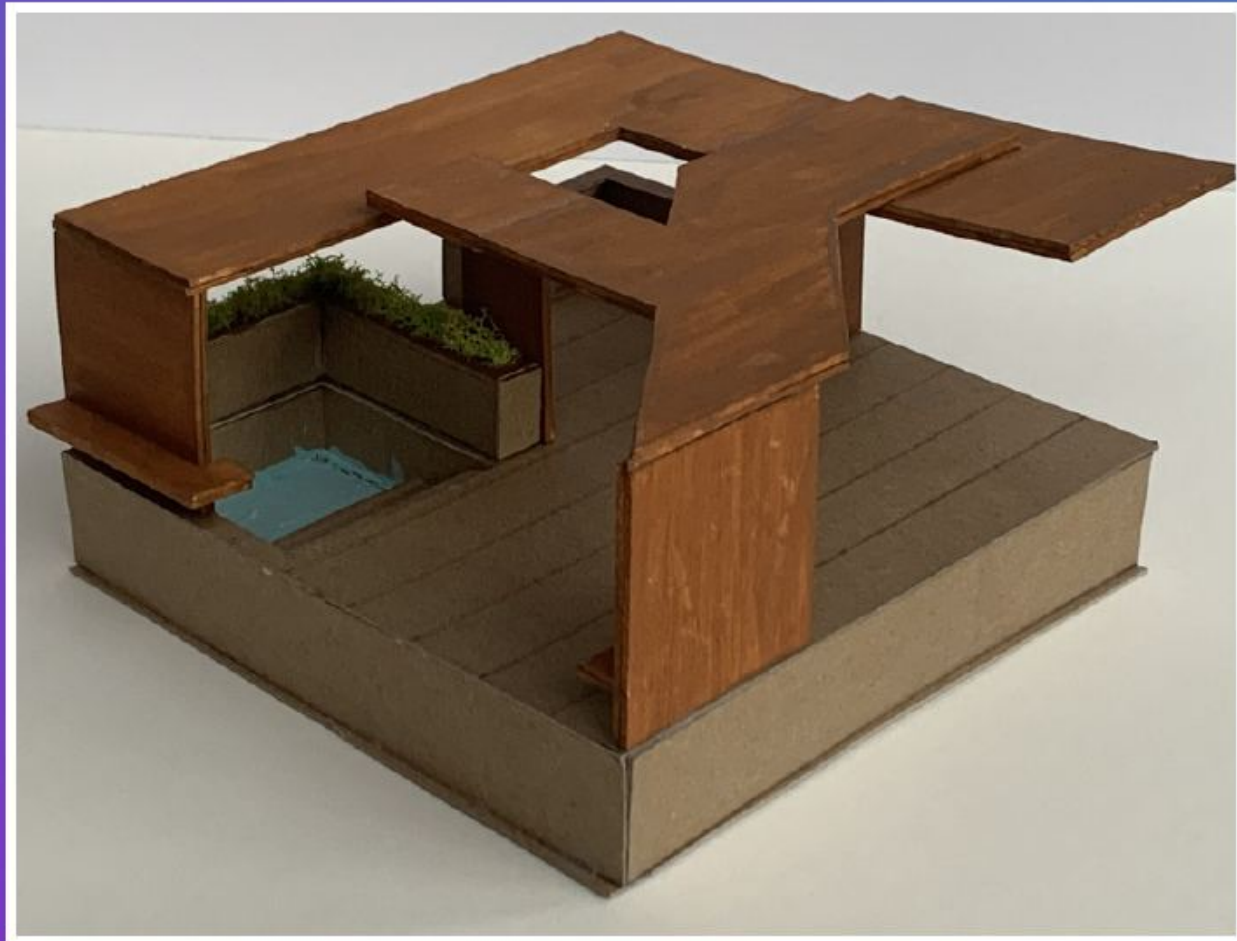

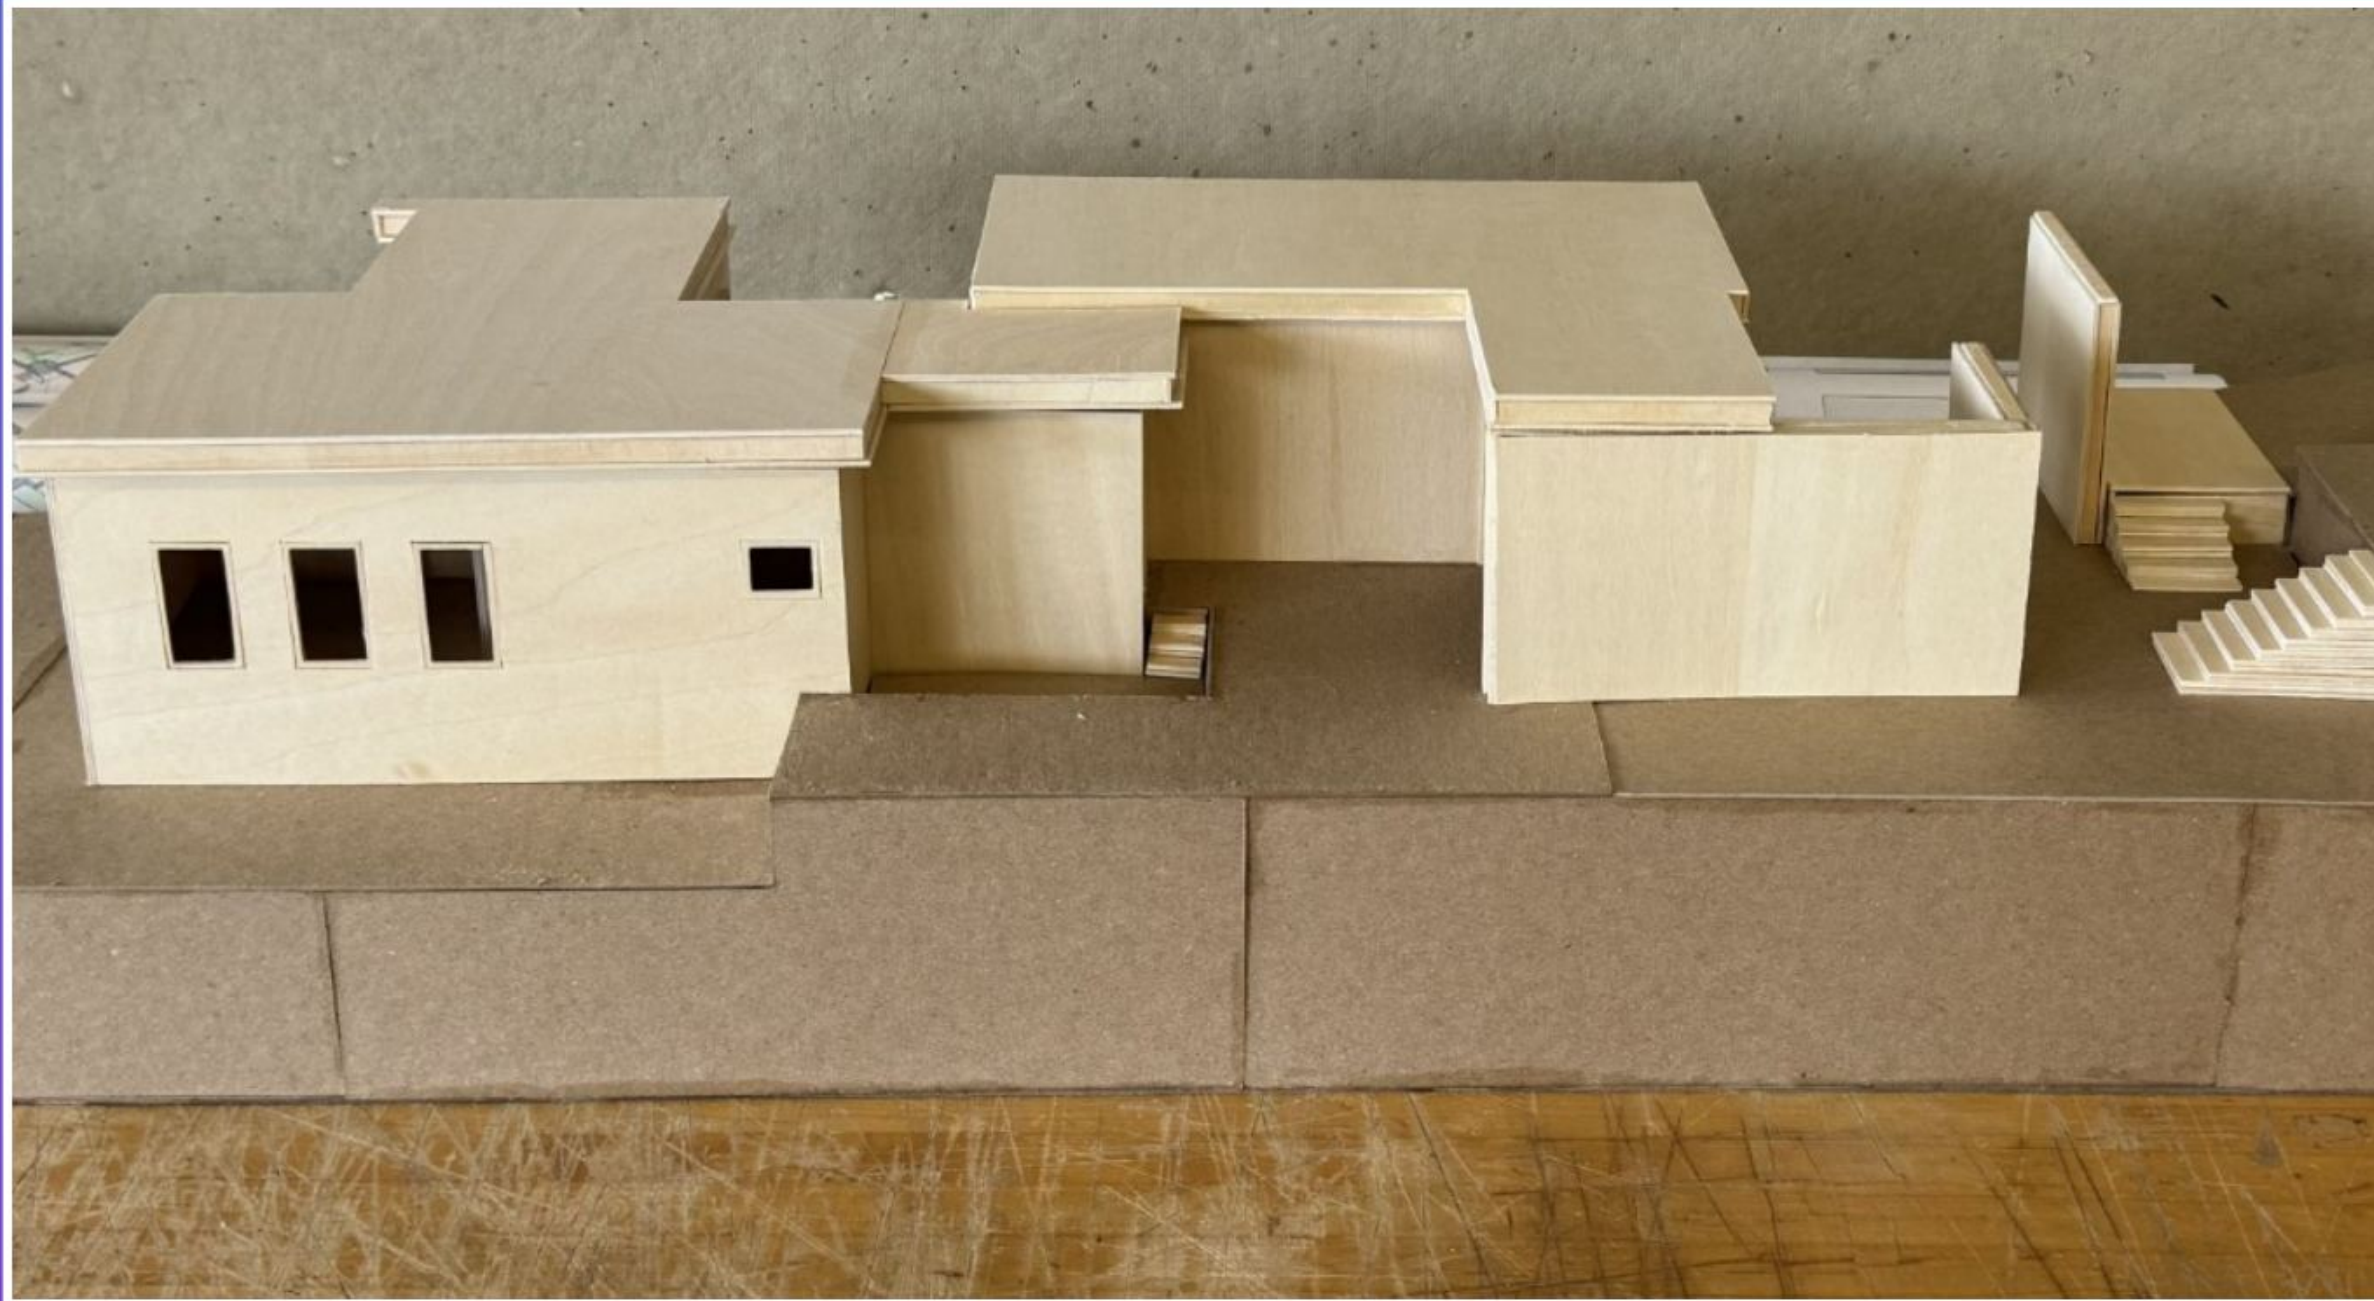

PROJECT - 03

ARTIST PATIO HOUSE

The task was to design a patio house for a specific artist, taking their artistic style into account. My artist was Carmen Herrera. Some restrictions to work with included the maximum enclosed building area being 30% of the lot size and the maximum enclosed area plus covered porches being 50%. The house was to be for two adults and three children, as well as an occasional guest. It also had to include one large and one small garden, a swimming pool, a studio and a gallery for artwork. The location of the site was in Miami, with the lot being at an incline.

SITE BIRD'S EYE VIEW


125' 0"





SITE PLAN



- A - Bedroom
- B - Bathroom
- C - Garden
- D - Gallery
- E - Studio
- F - Deck Area
- G - Foyer

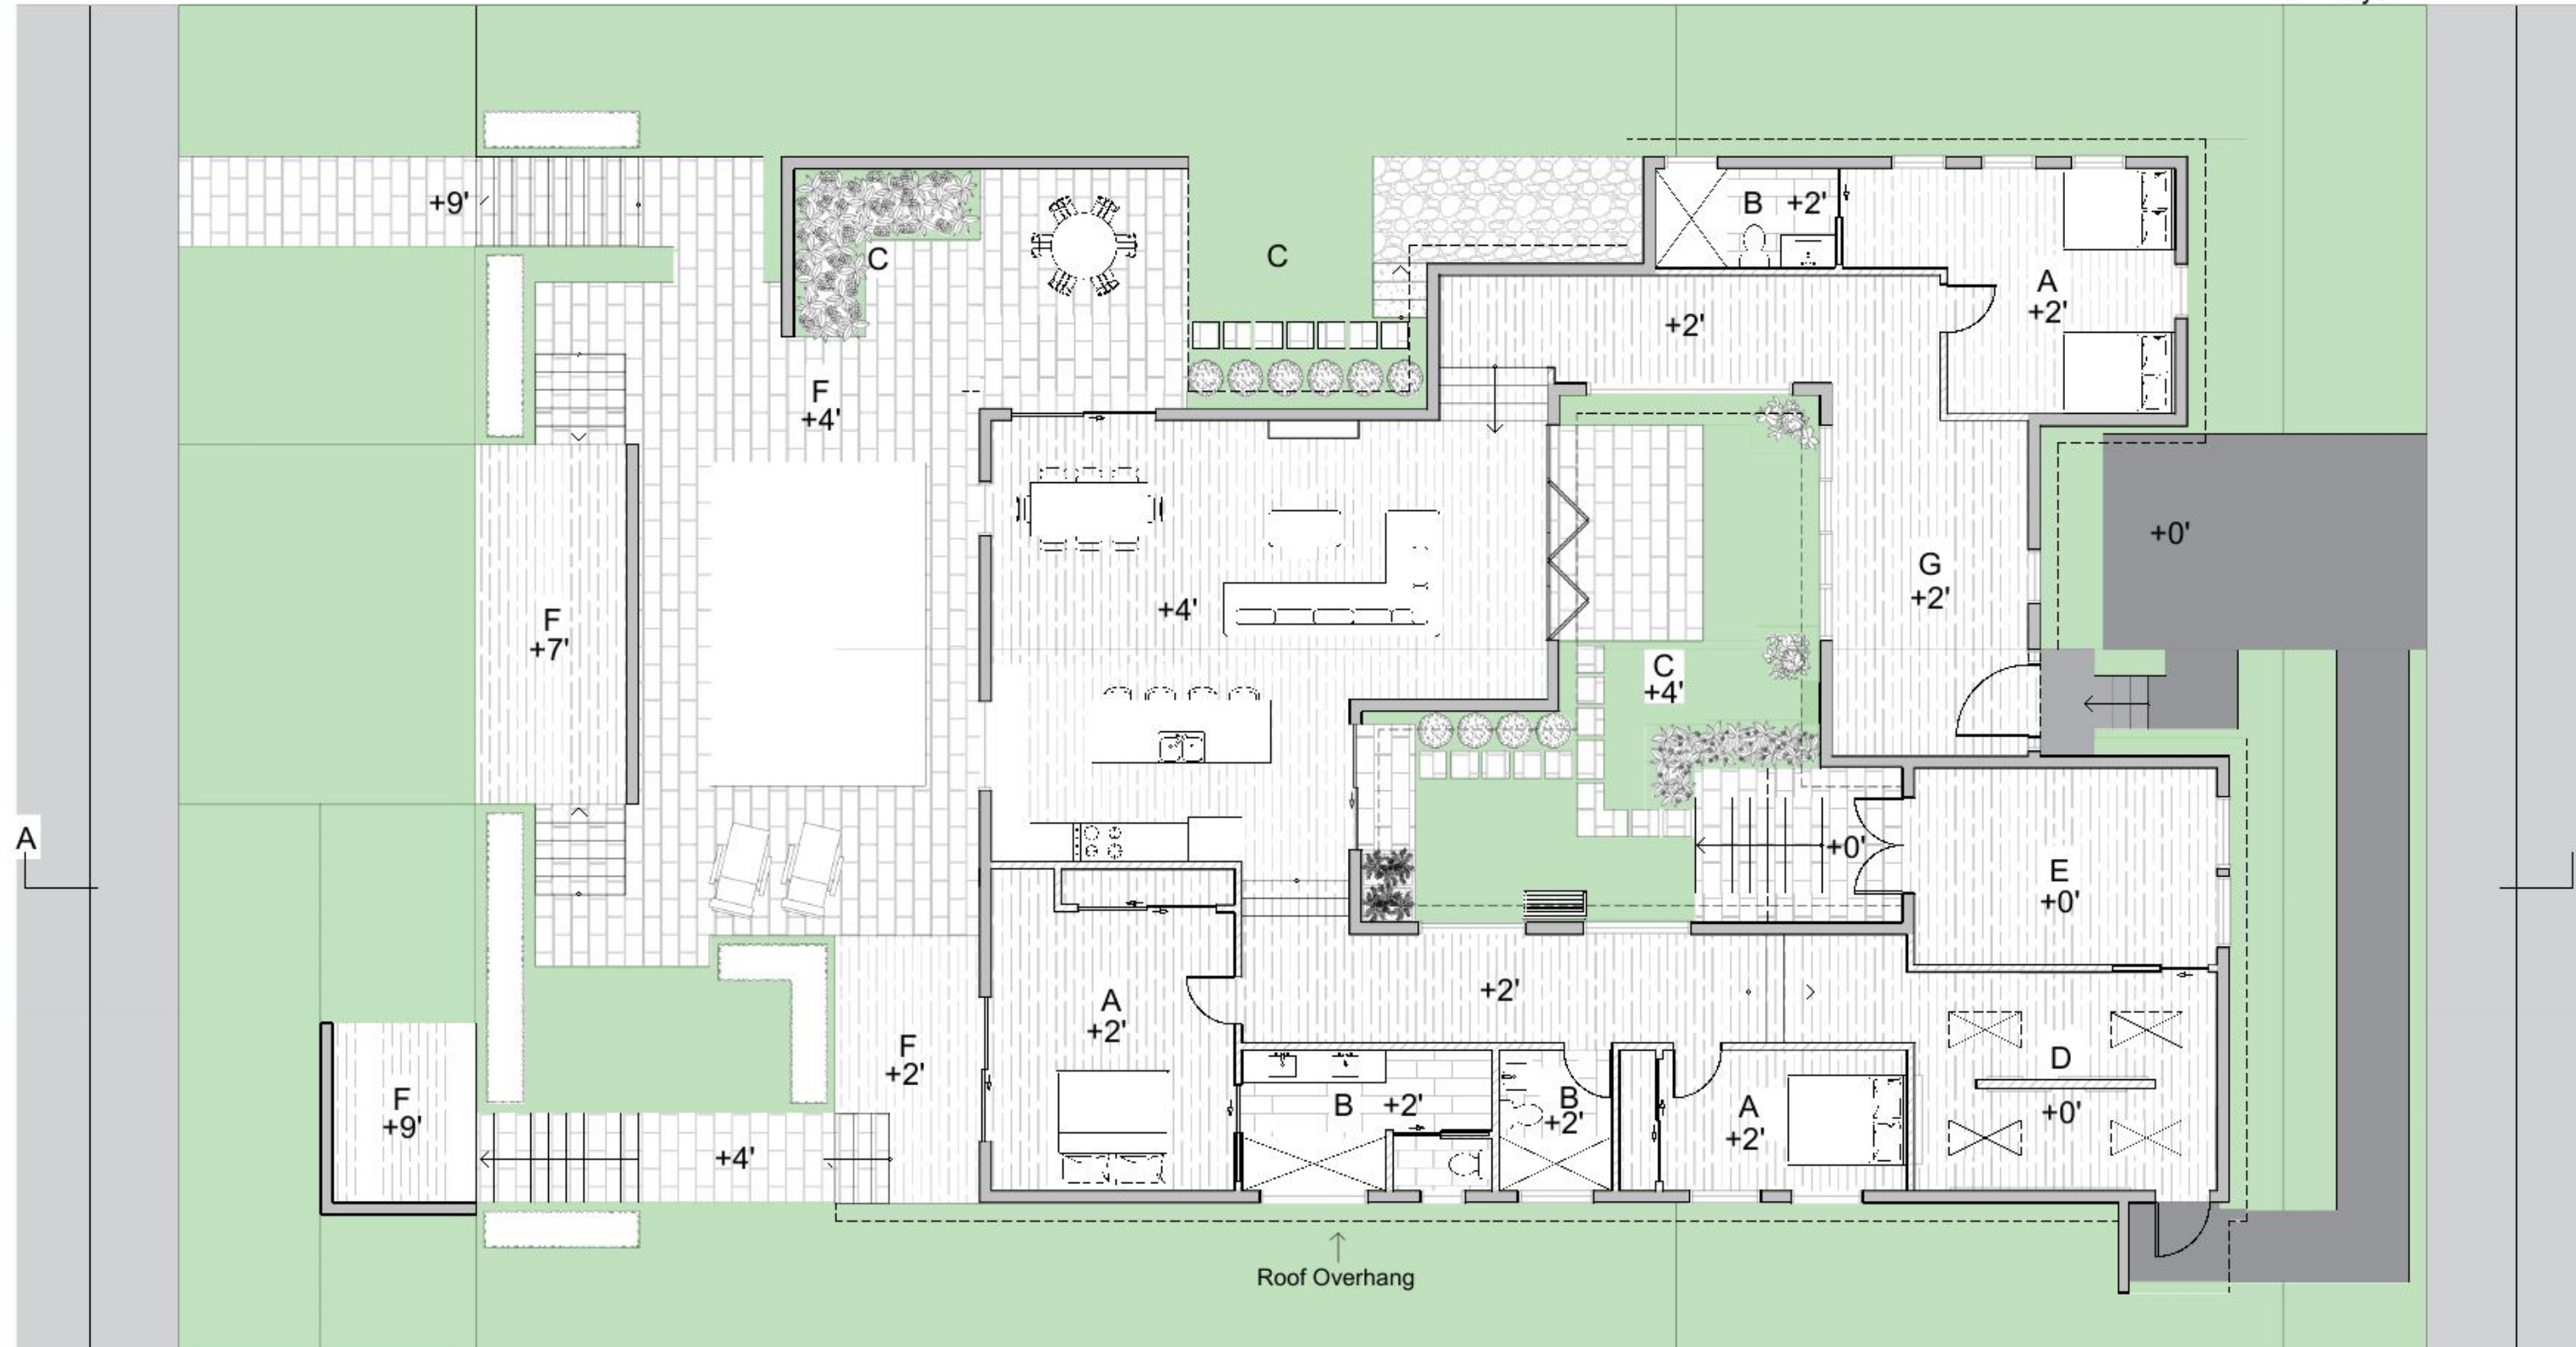

LONGITUDINAL SECTION AND ELEVATION

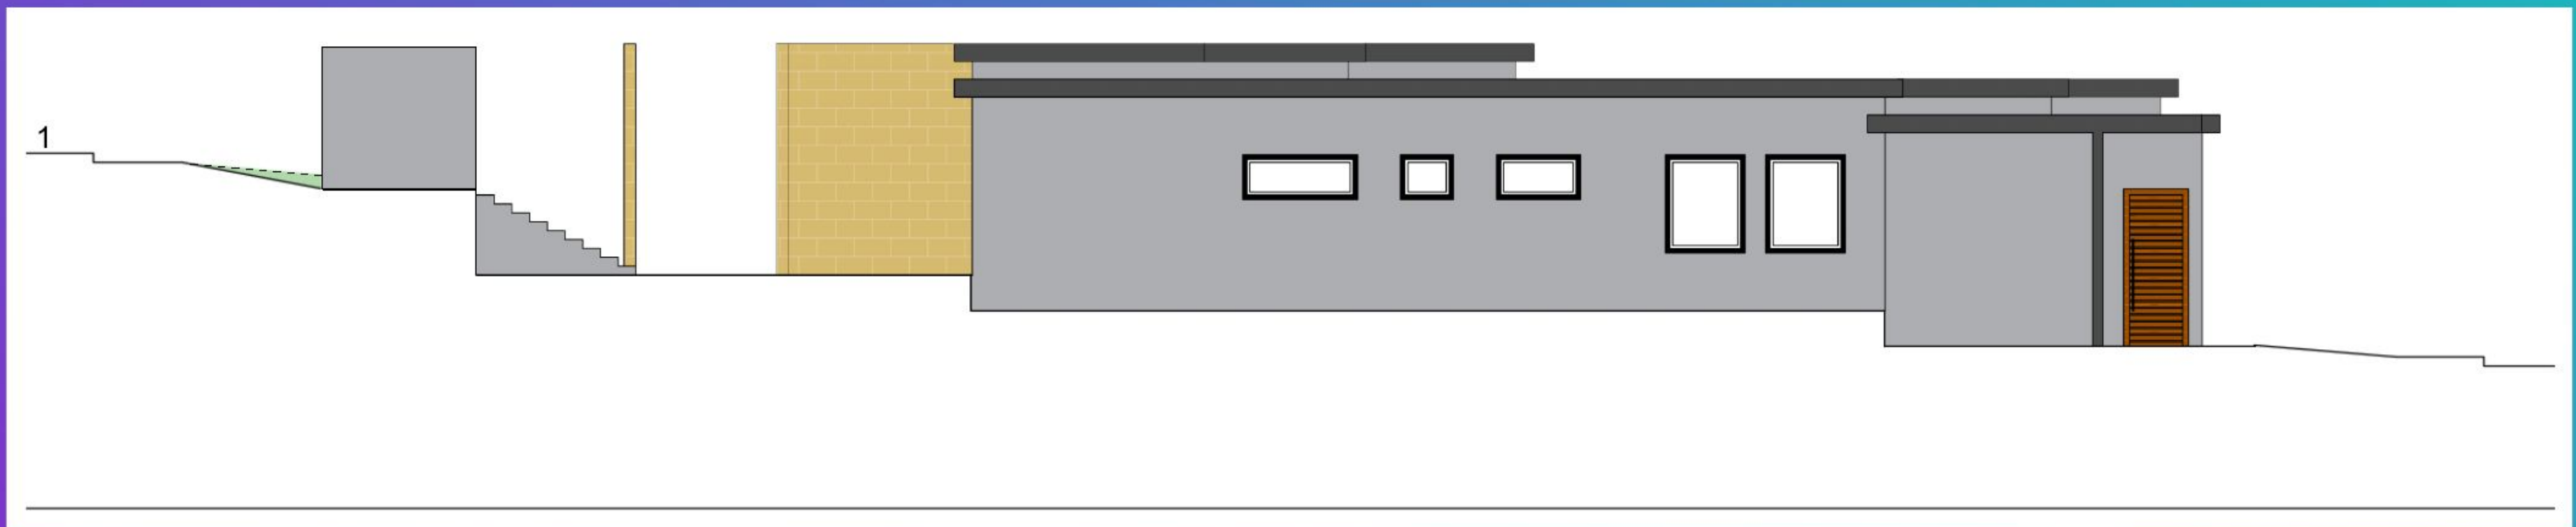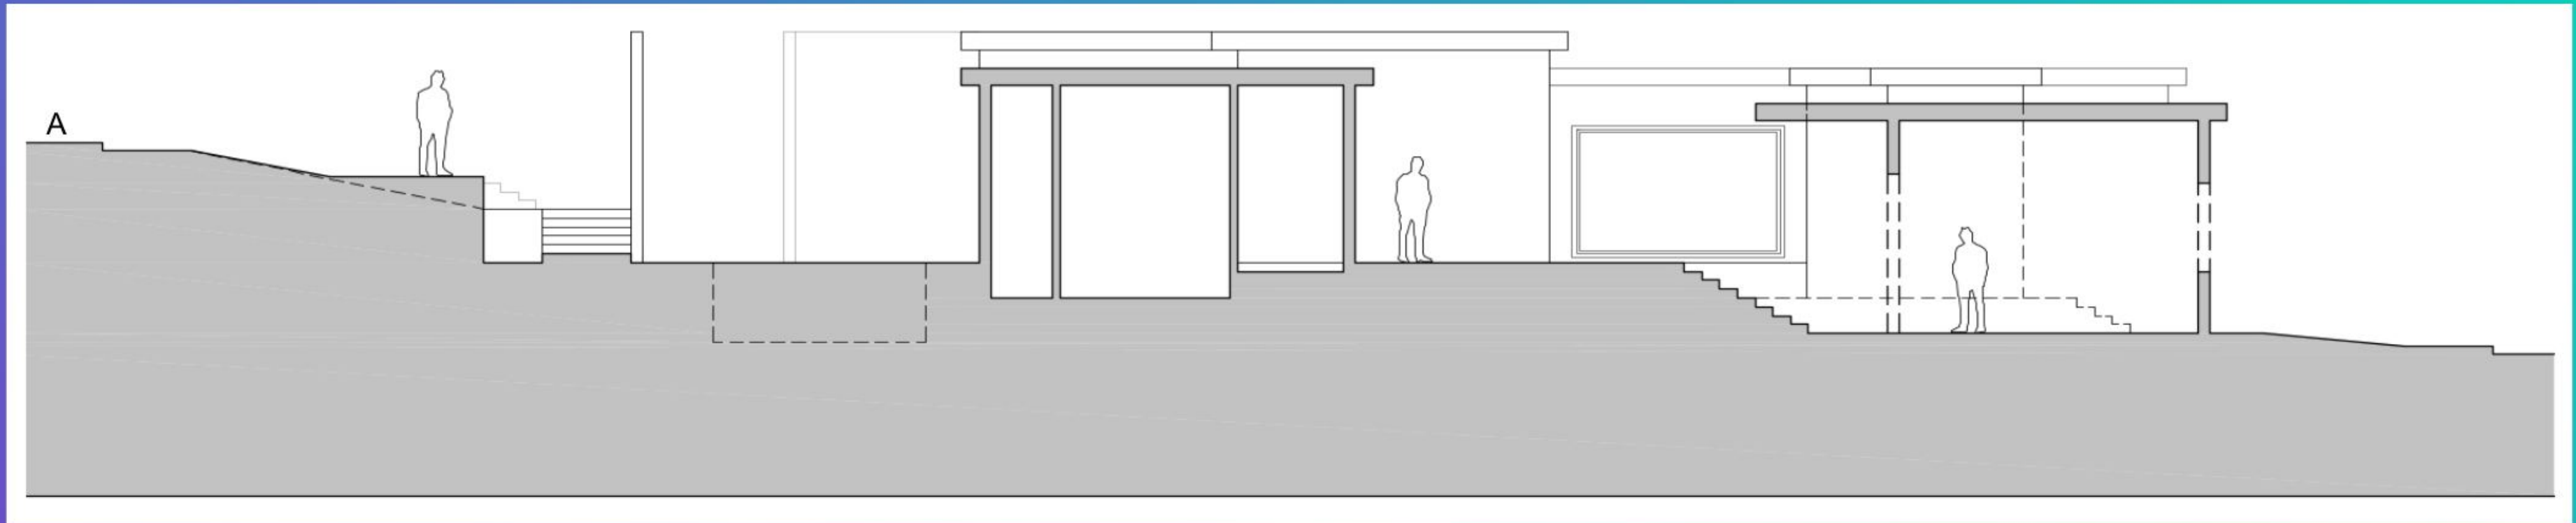




LONGITUDINAL SECTION & COURTYARD SECTION




ISOs



LANDSCAPE AND
STRUCTURE

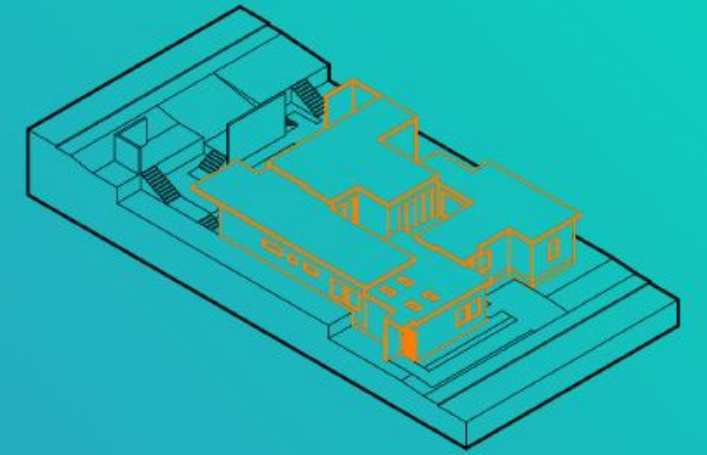


MASSING OF
HOUSING

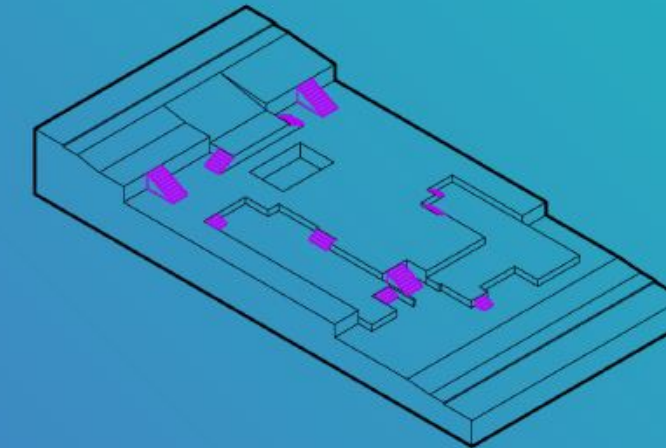


STAIRCASES IN
LANDSCAPE




GROUND
MANIPULATION


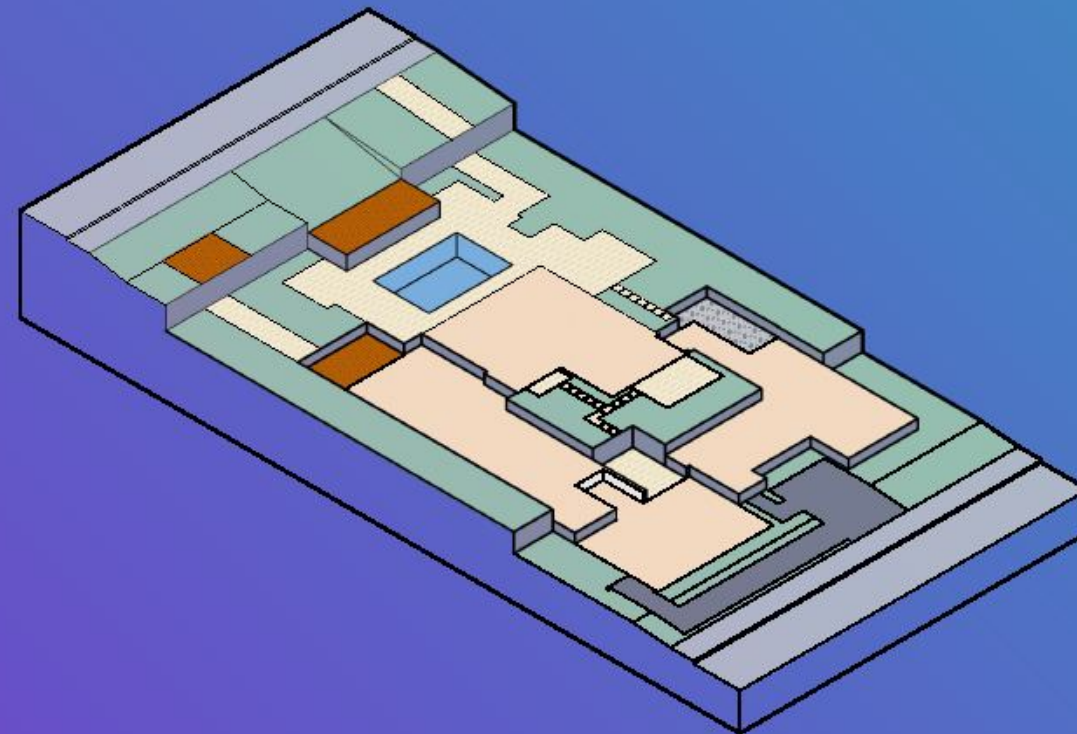


CIRCULATION


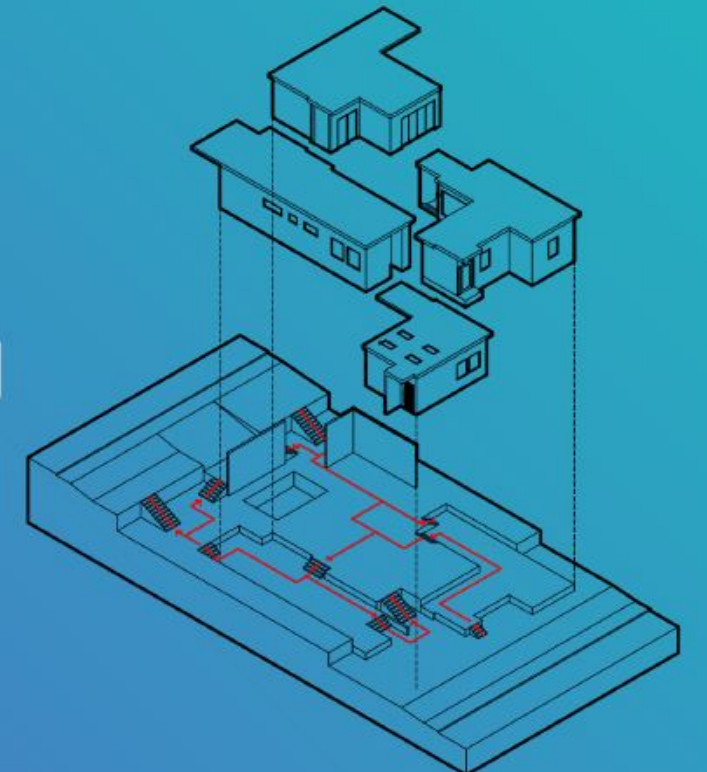


Carmen Herrera was a Cuban-born and raised American painter, born on May 31, 1915, and died on February 12, 2022. Known for her minimalist and abstract paintings, she moved to Paris as a teenager to study art, and attempted a career in Architecture, which did not come to fruition due to Cuba's unstable situation. She continued to pursue her studies in art in New York and Paris again. Her artistic identity was one of boldly colored and sharply defined geometric shape paintings. She made New York City her permanent home in 1954, where for years she only exhibited some of her art sporadically. It wasn't until 2004 (at the age of 89) that she sold her first painting. After being included in NYC's latincollector gallery, her art-world stock skyrocketed. Her works were acquired for permanent collections in several museums, and won accolades in London for several solo exhibitions.

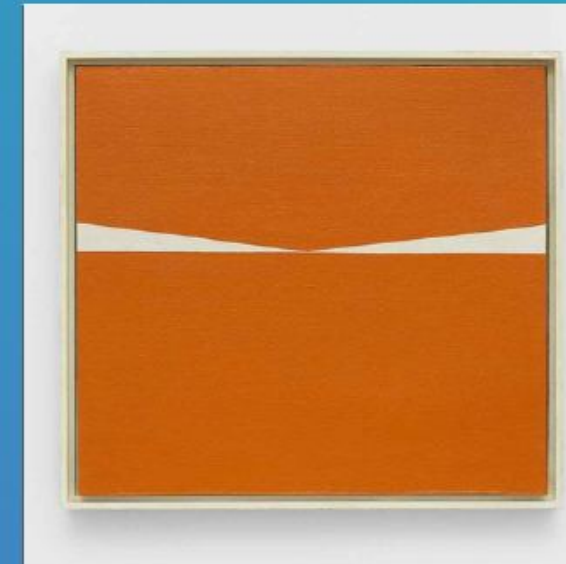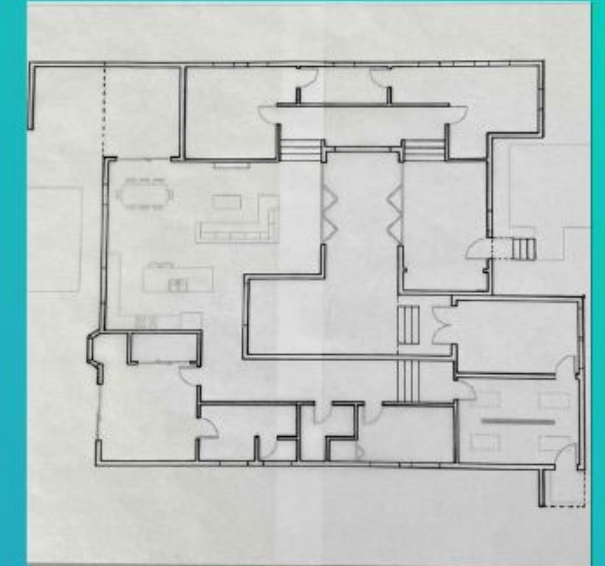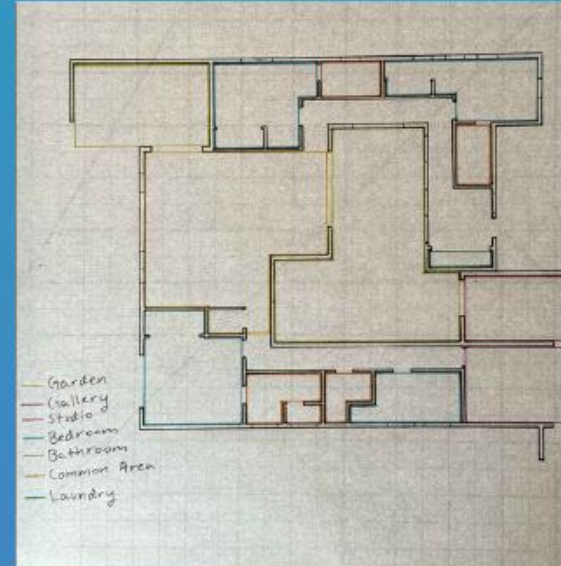


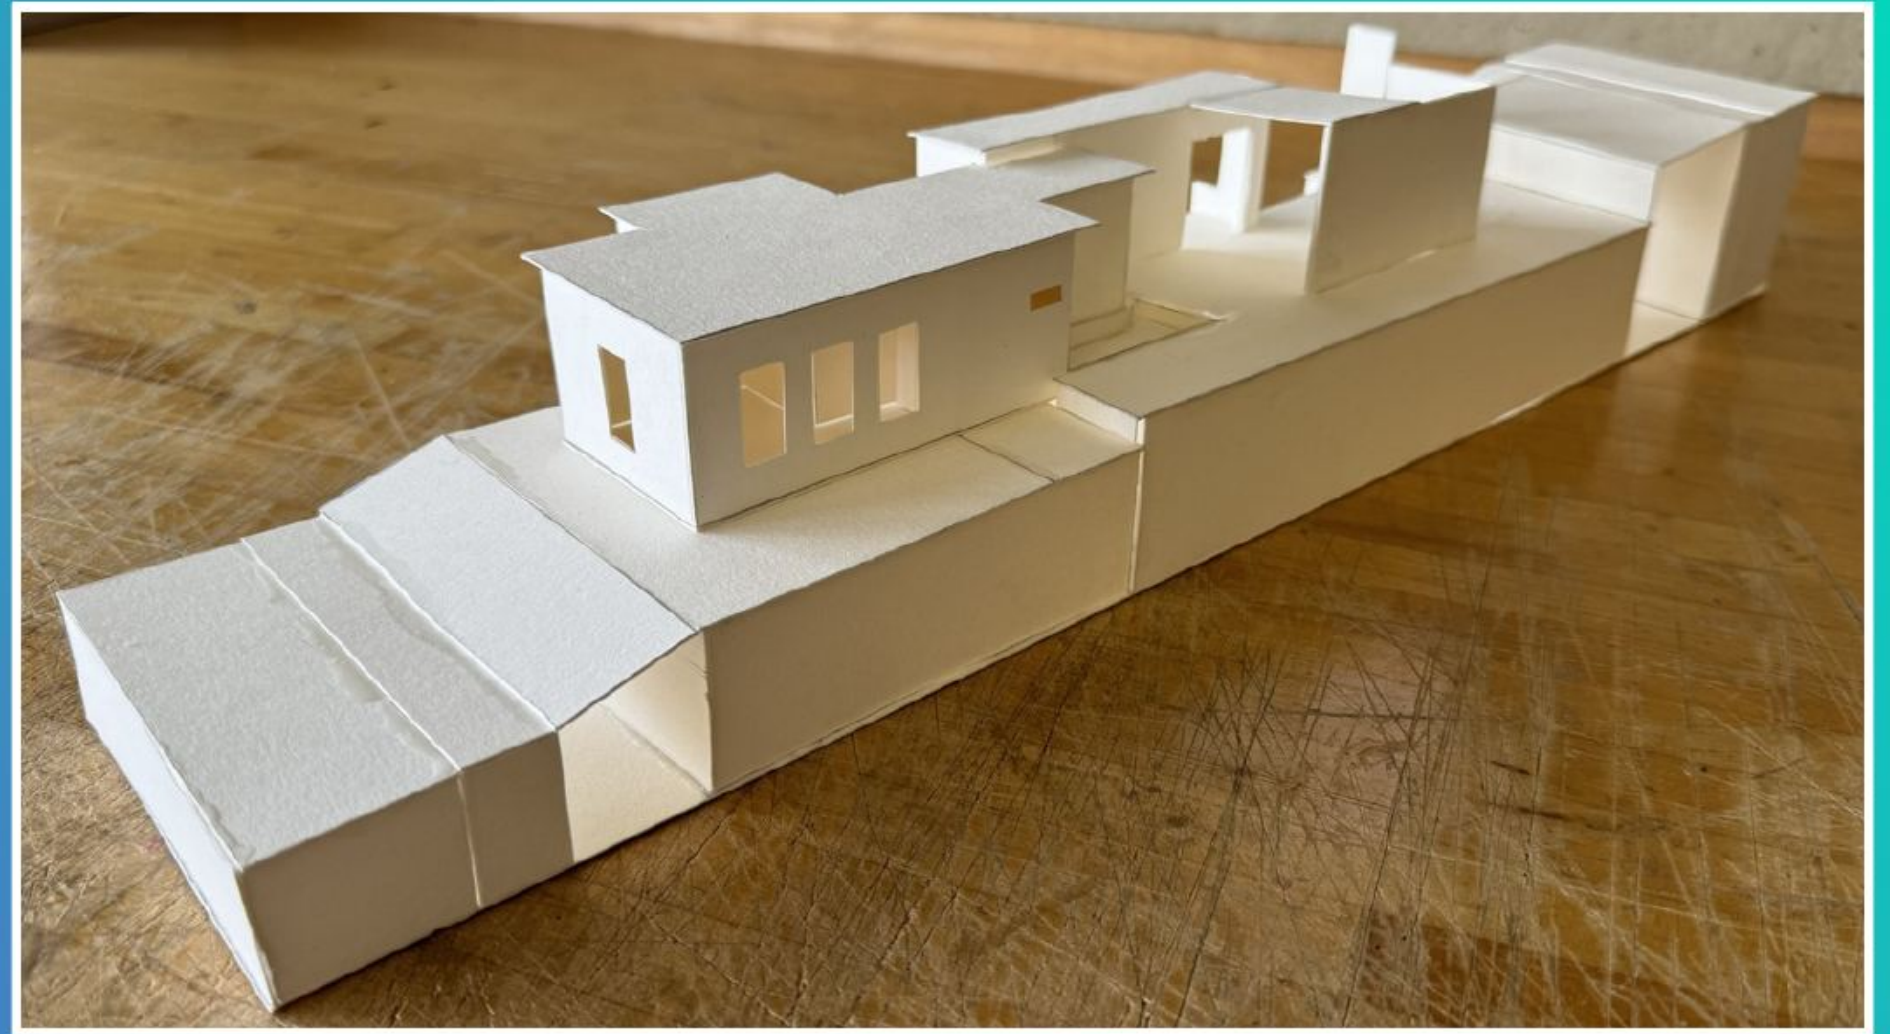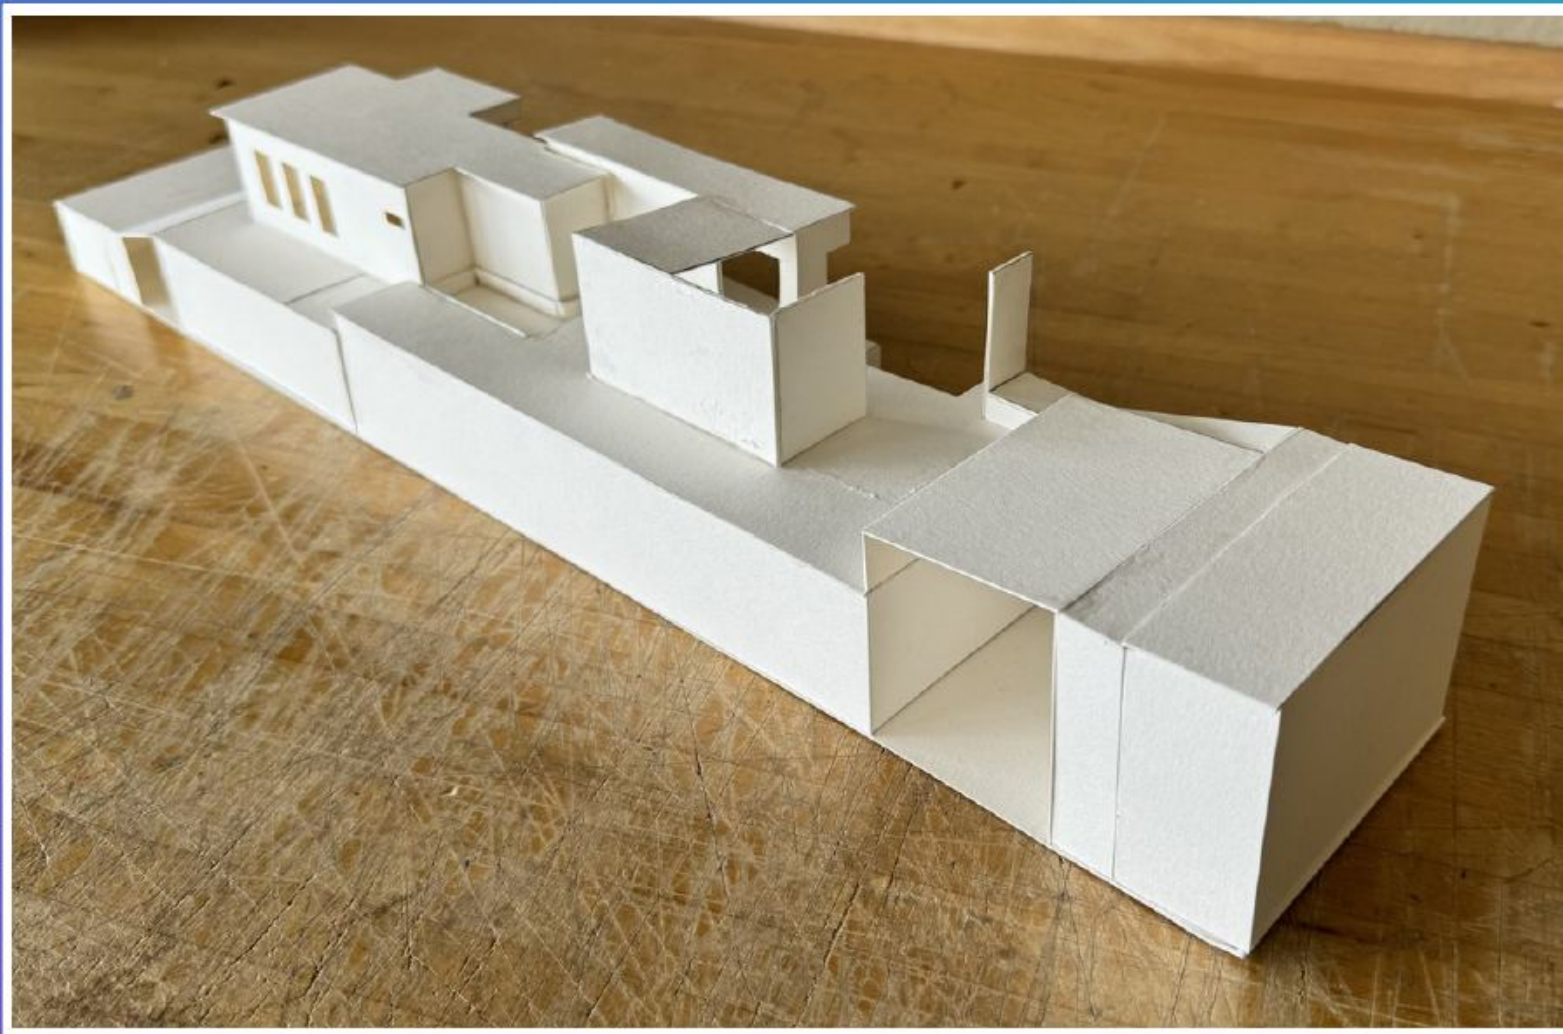

SECTION MODEL 1

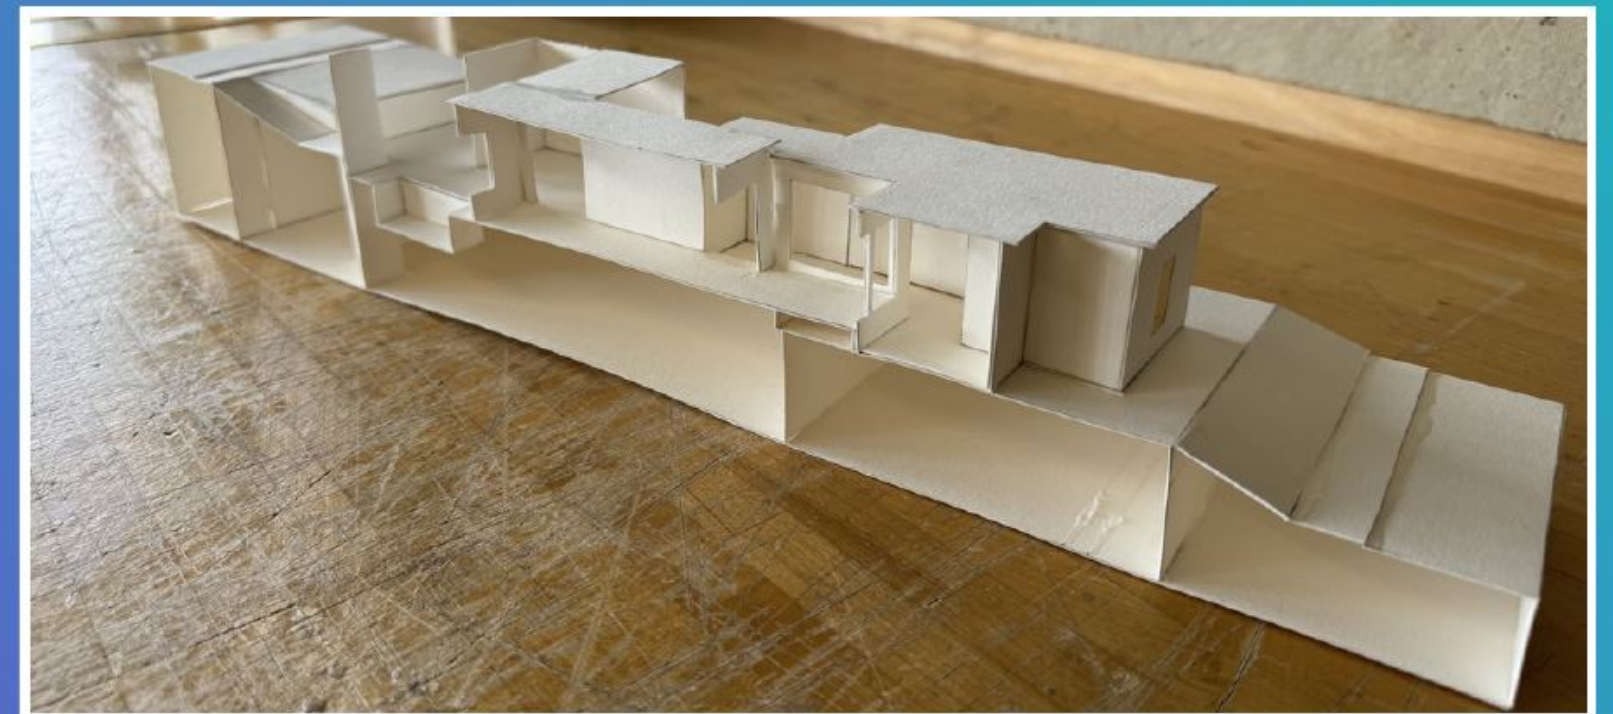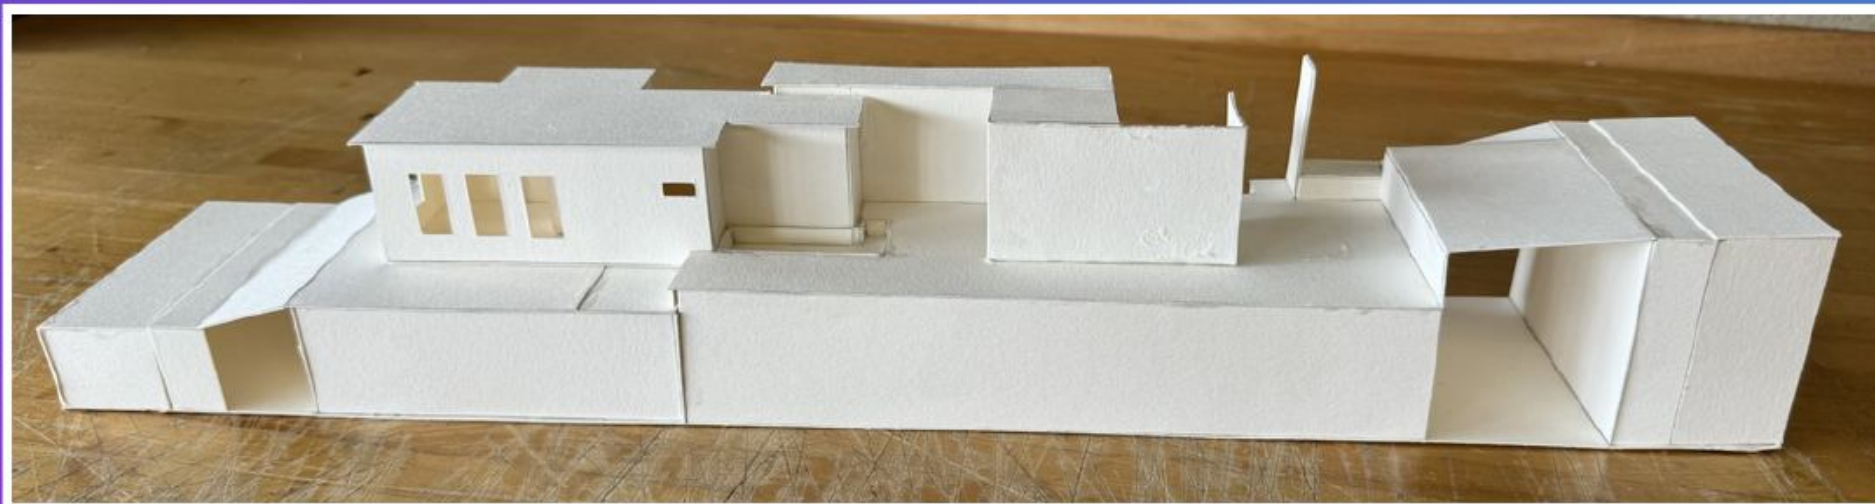

SECTION MODEL 2 & MASSING MODEL

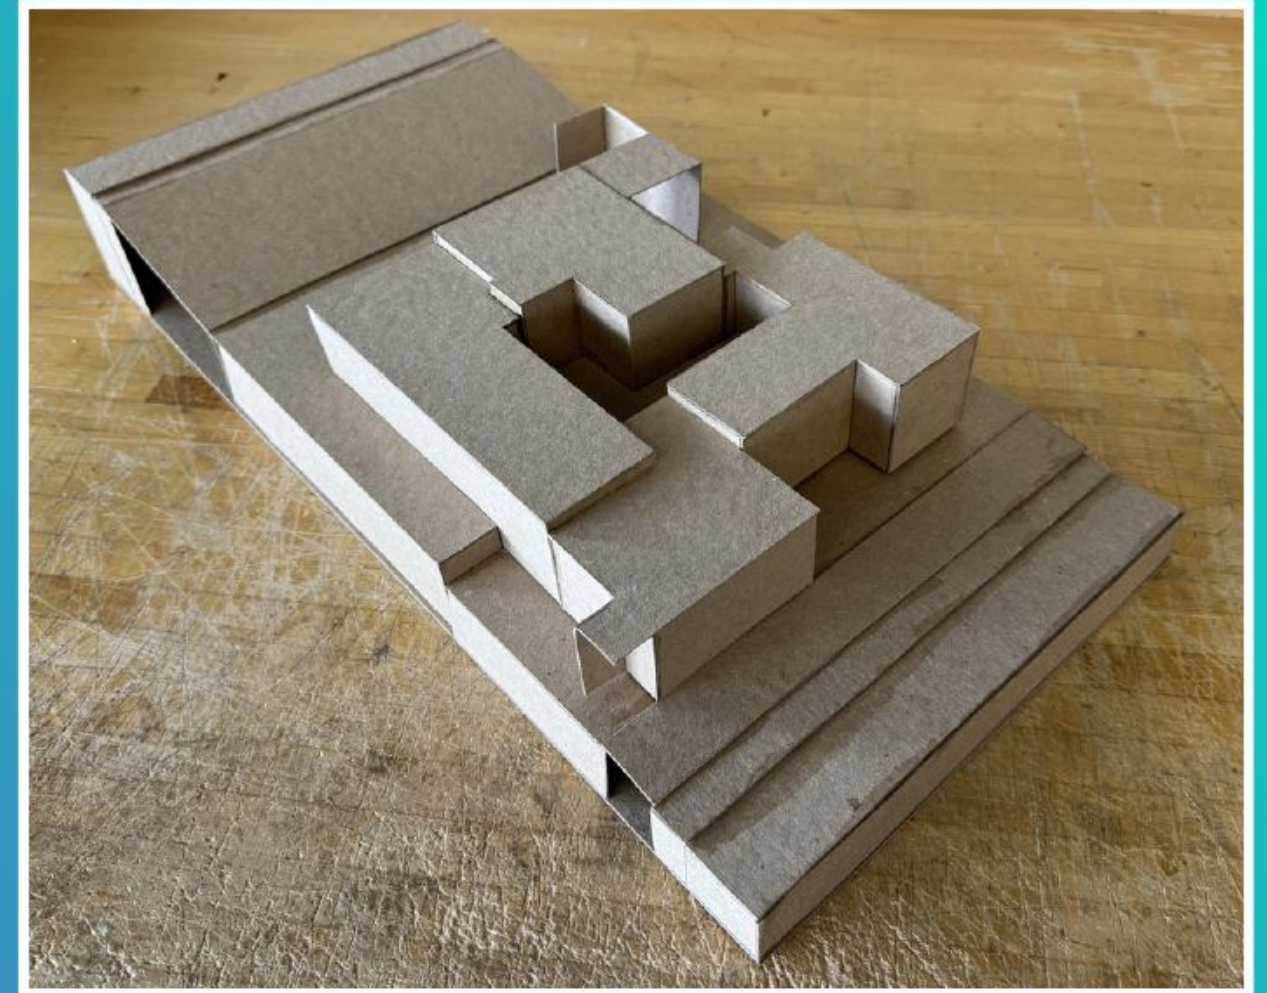




PROJECT - 04



FLORIDA ROOM AT HISS STUDIO AND RESIDENCE

The task was to design a Florida room between the Hiss Studio and Residence in Sarasota, Florida. This would serve as the place where the artist would conduct their work. It had to include a studio, a bathroom, and outdoor spaces. There were also limitations with the smaller lot size and with the shorter height limit.


SITE PLAN AND ELEVATION

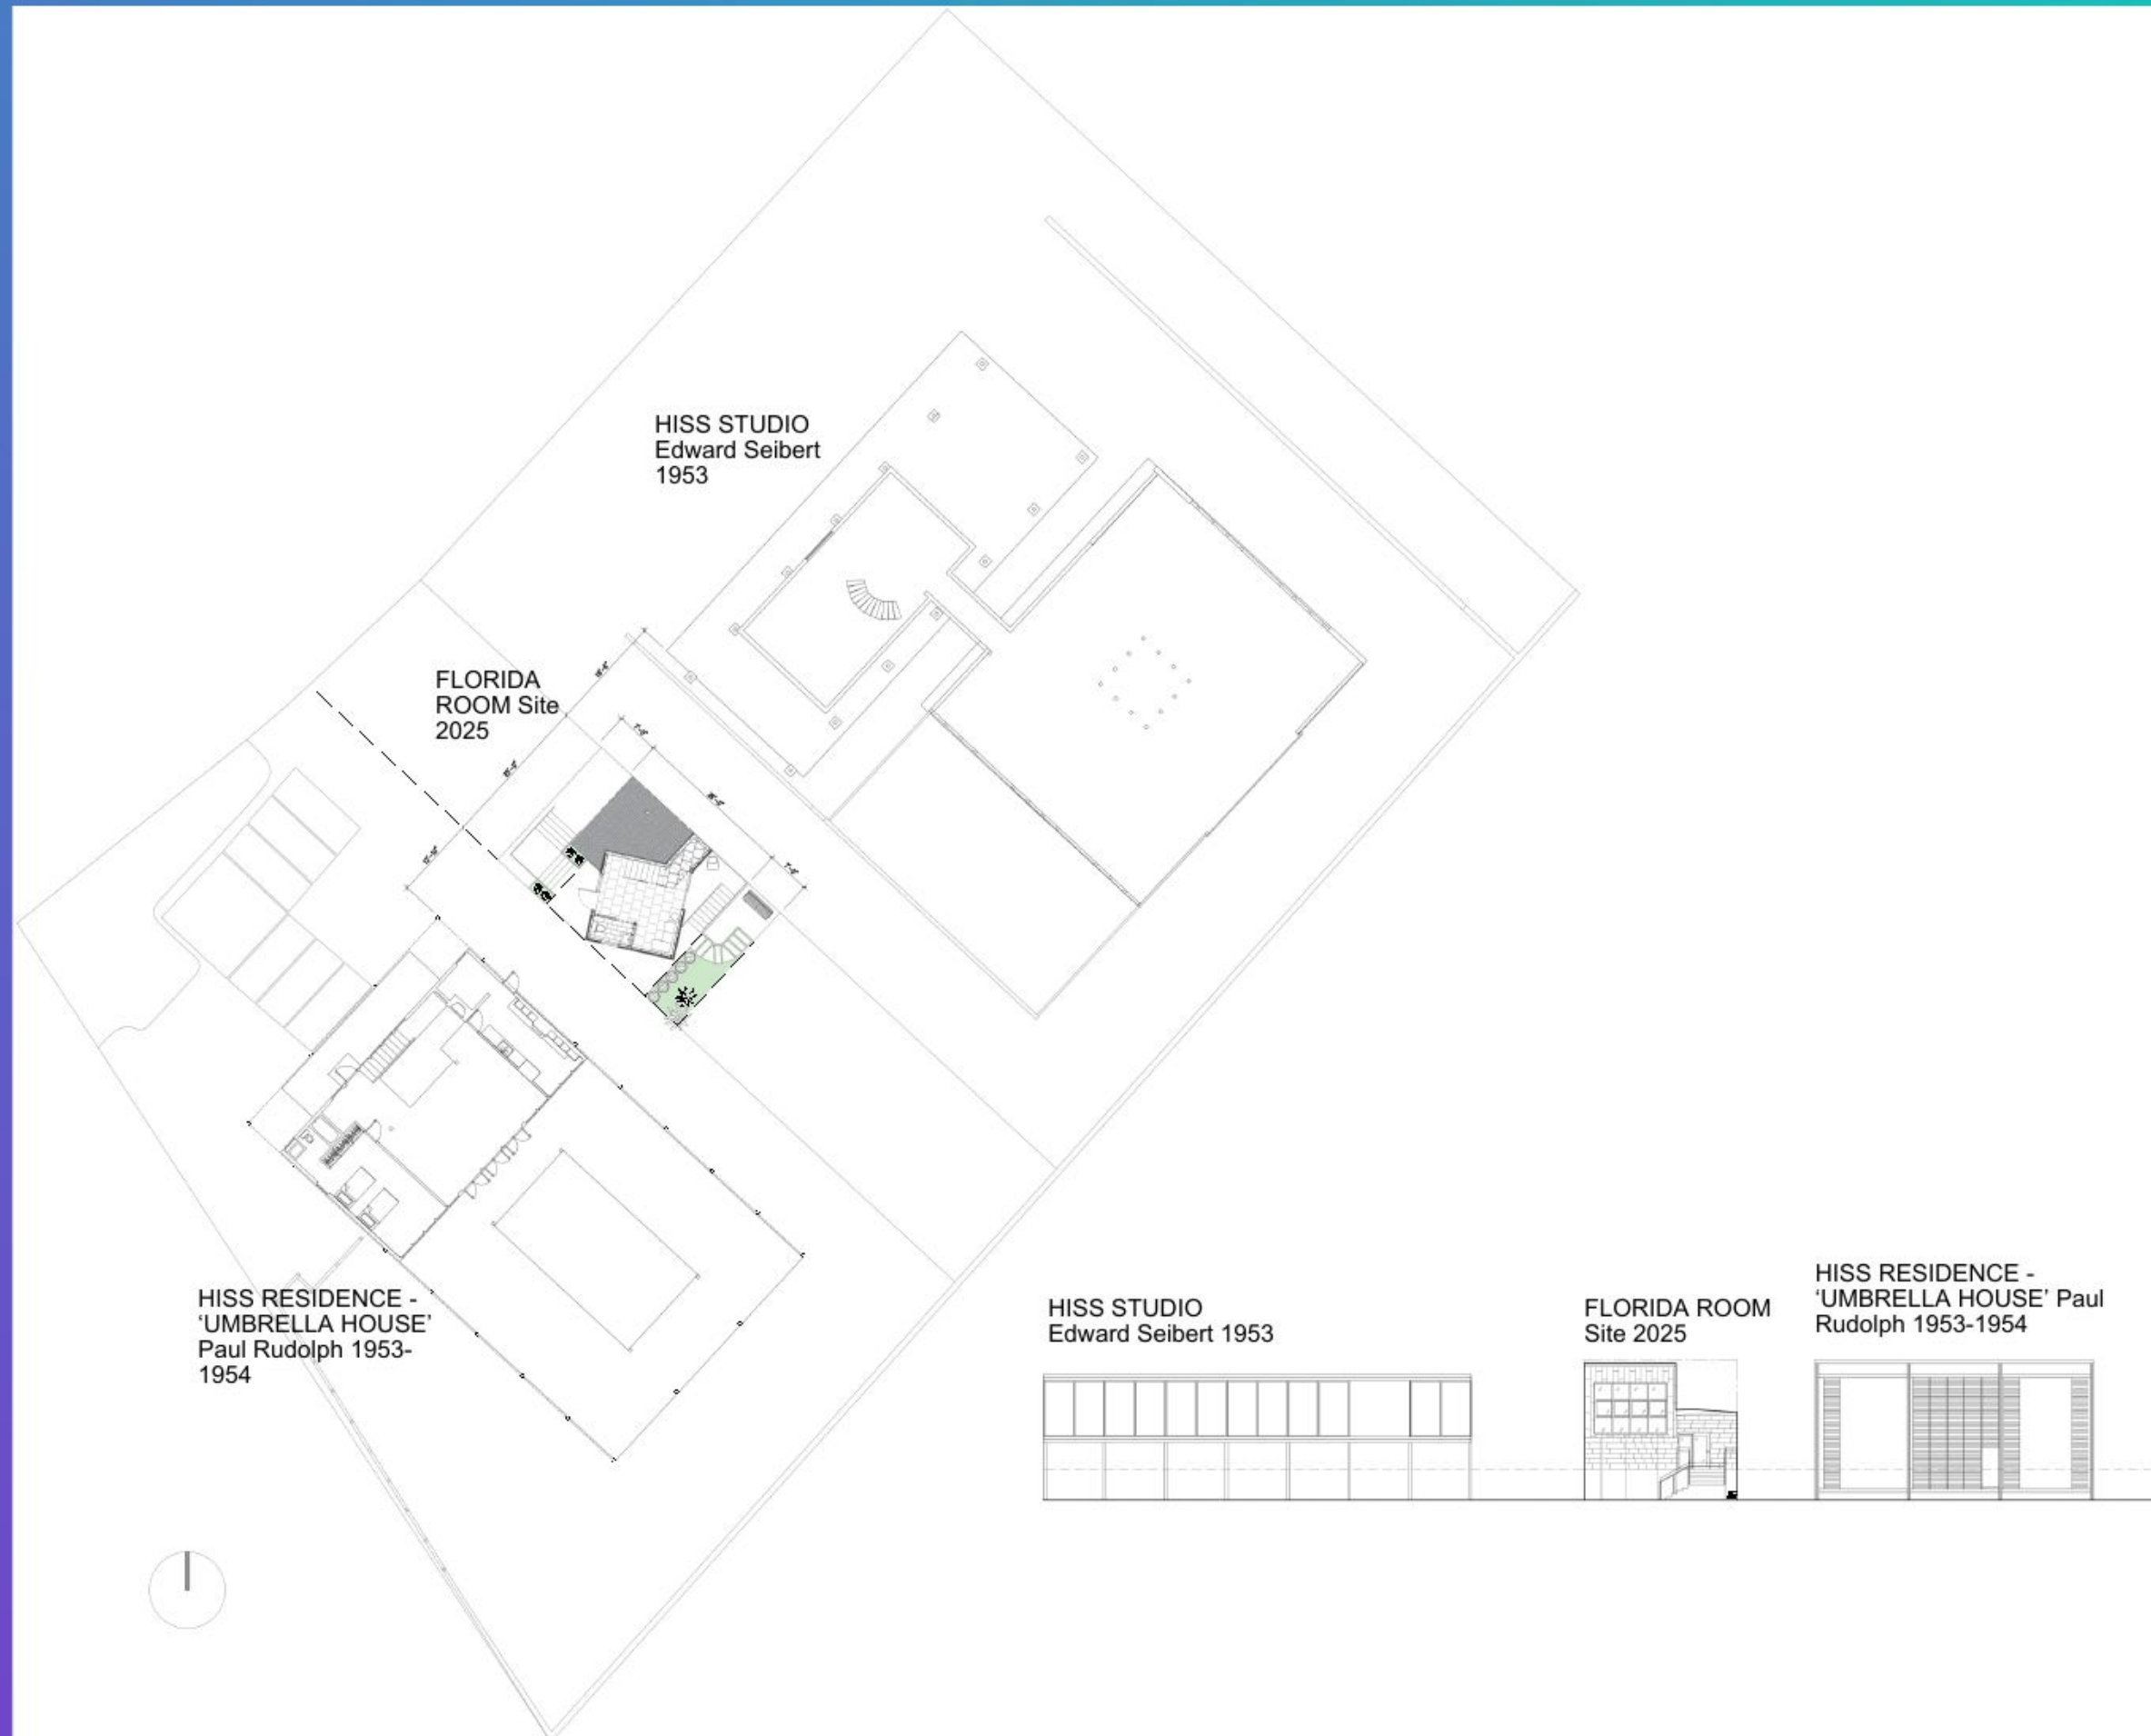


FLOORS 1 & 2 PLANS

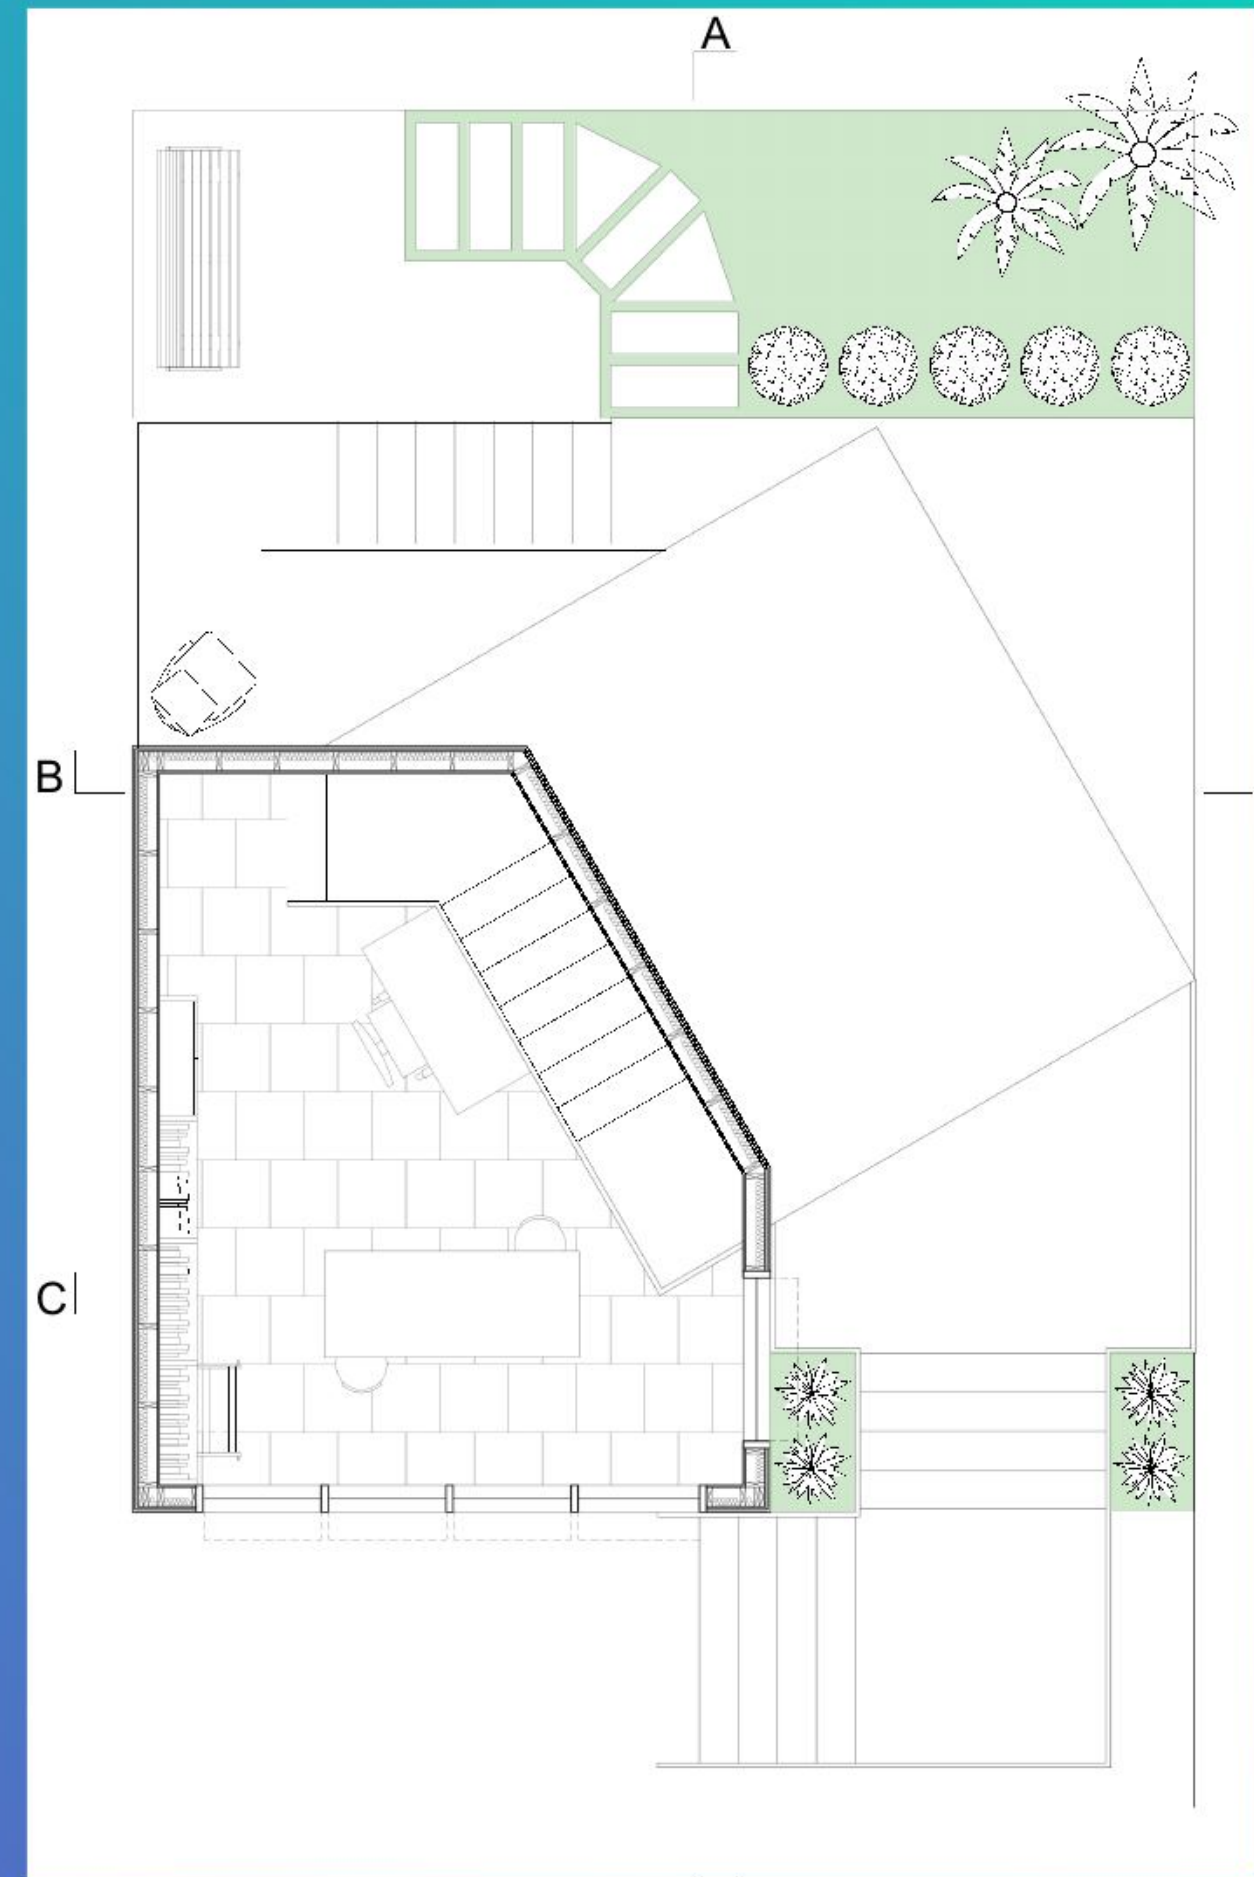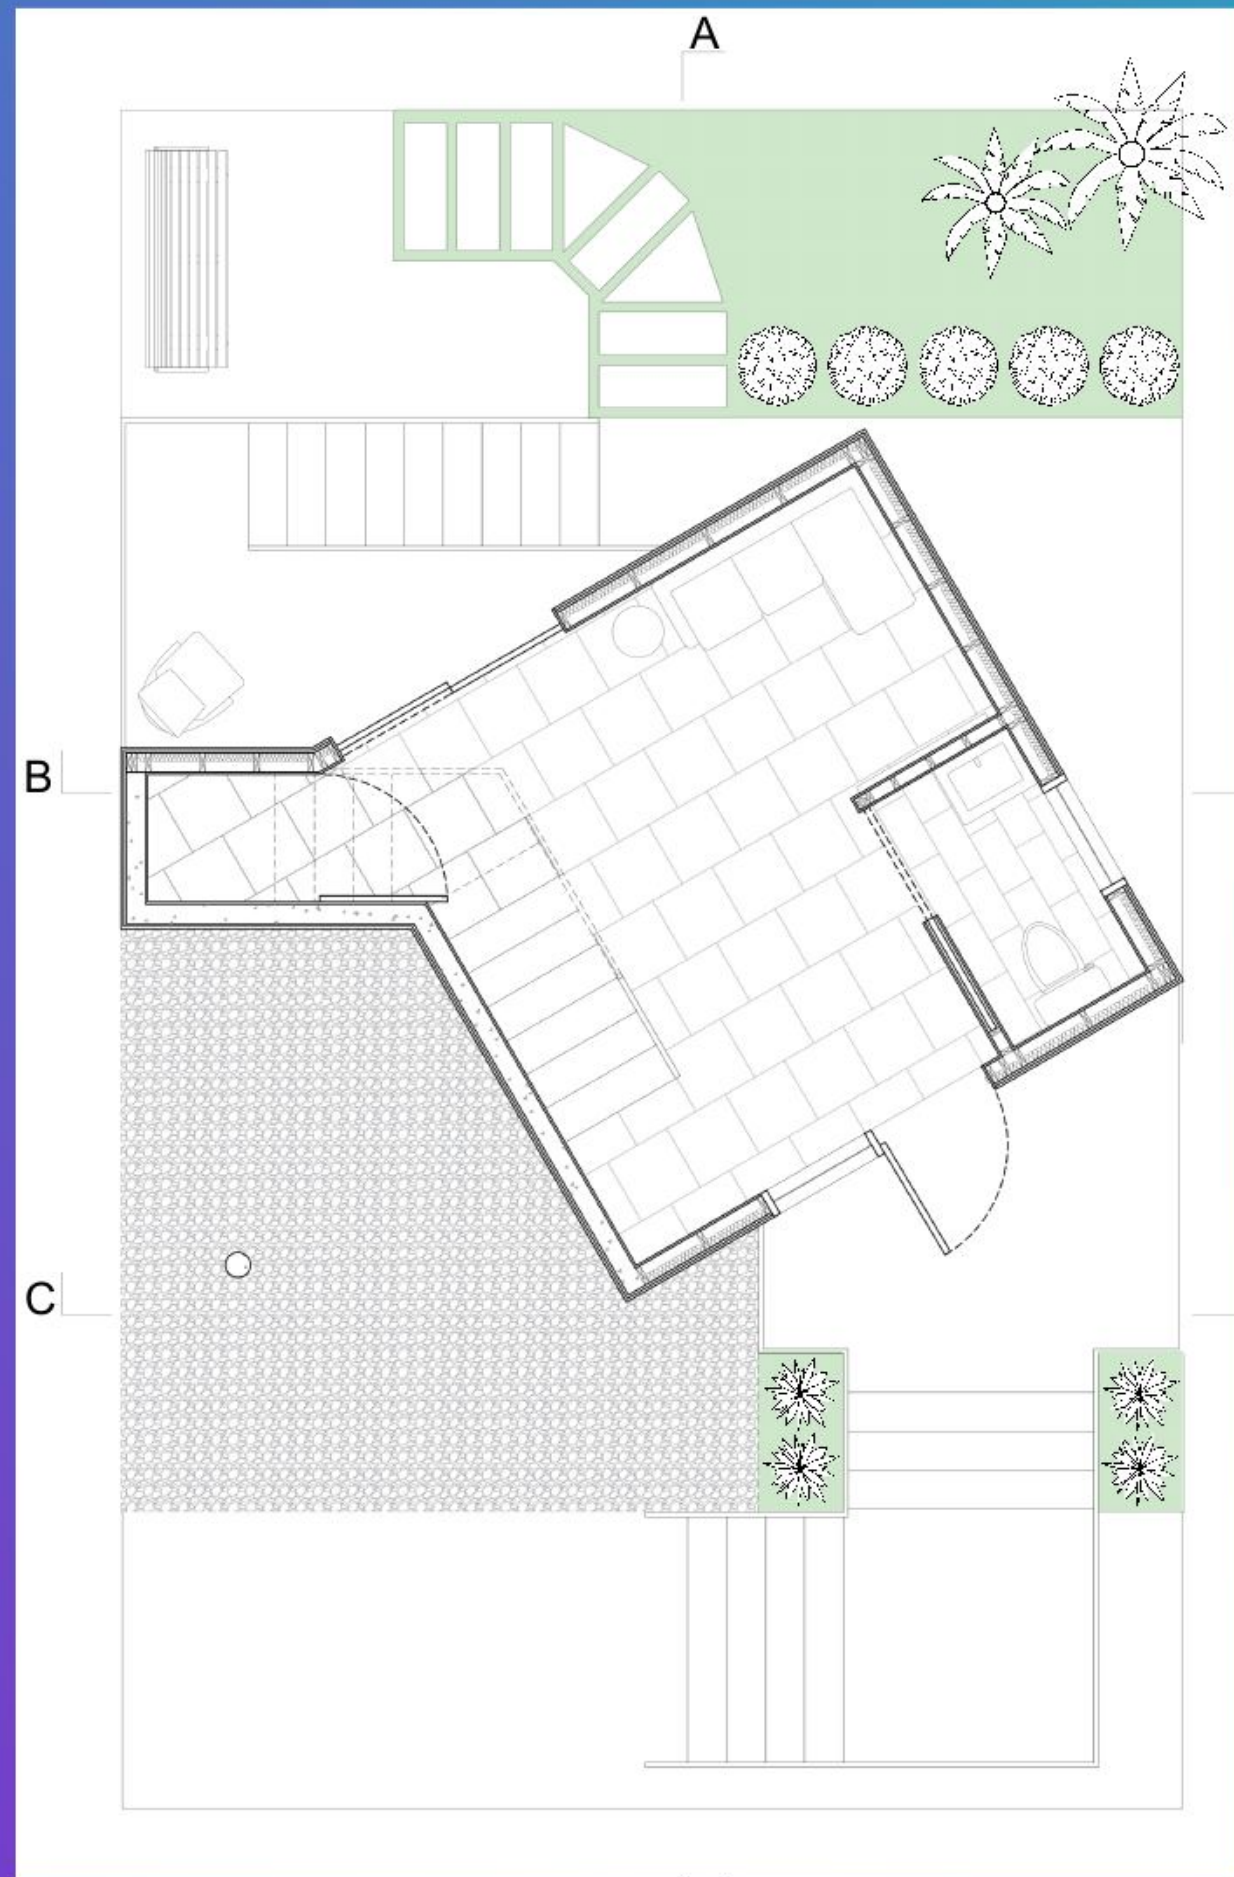


LONG SECTION THROUGH ROOM

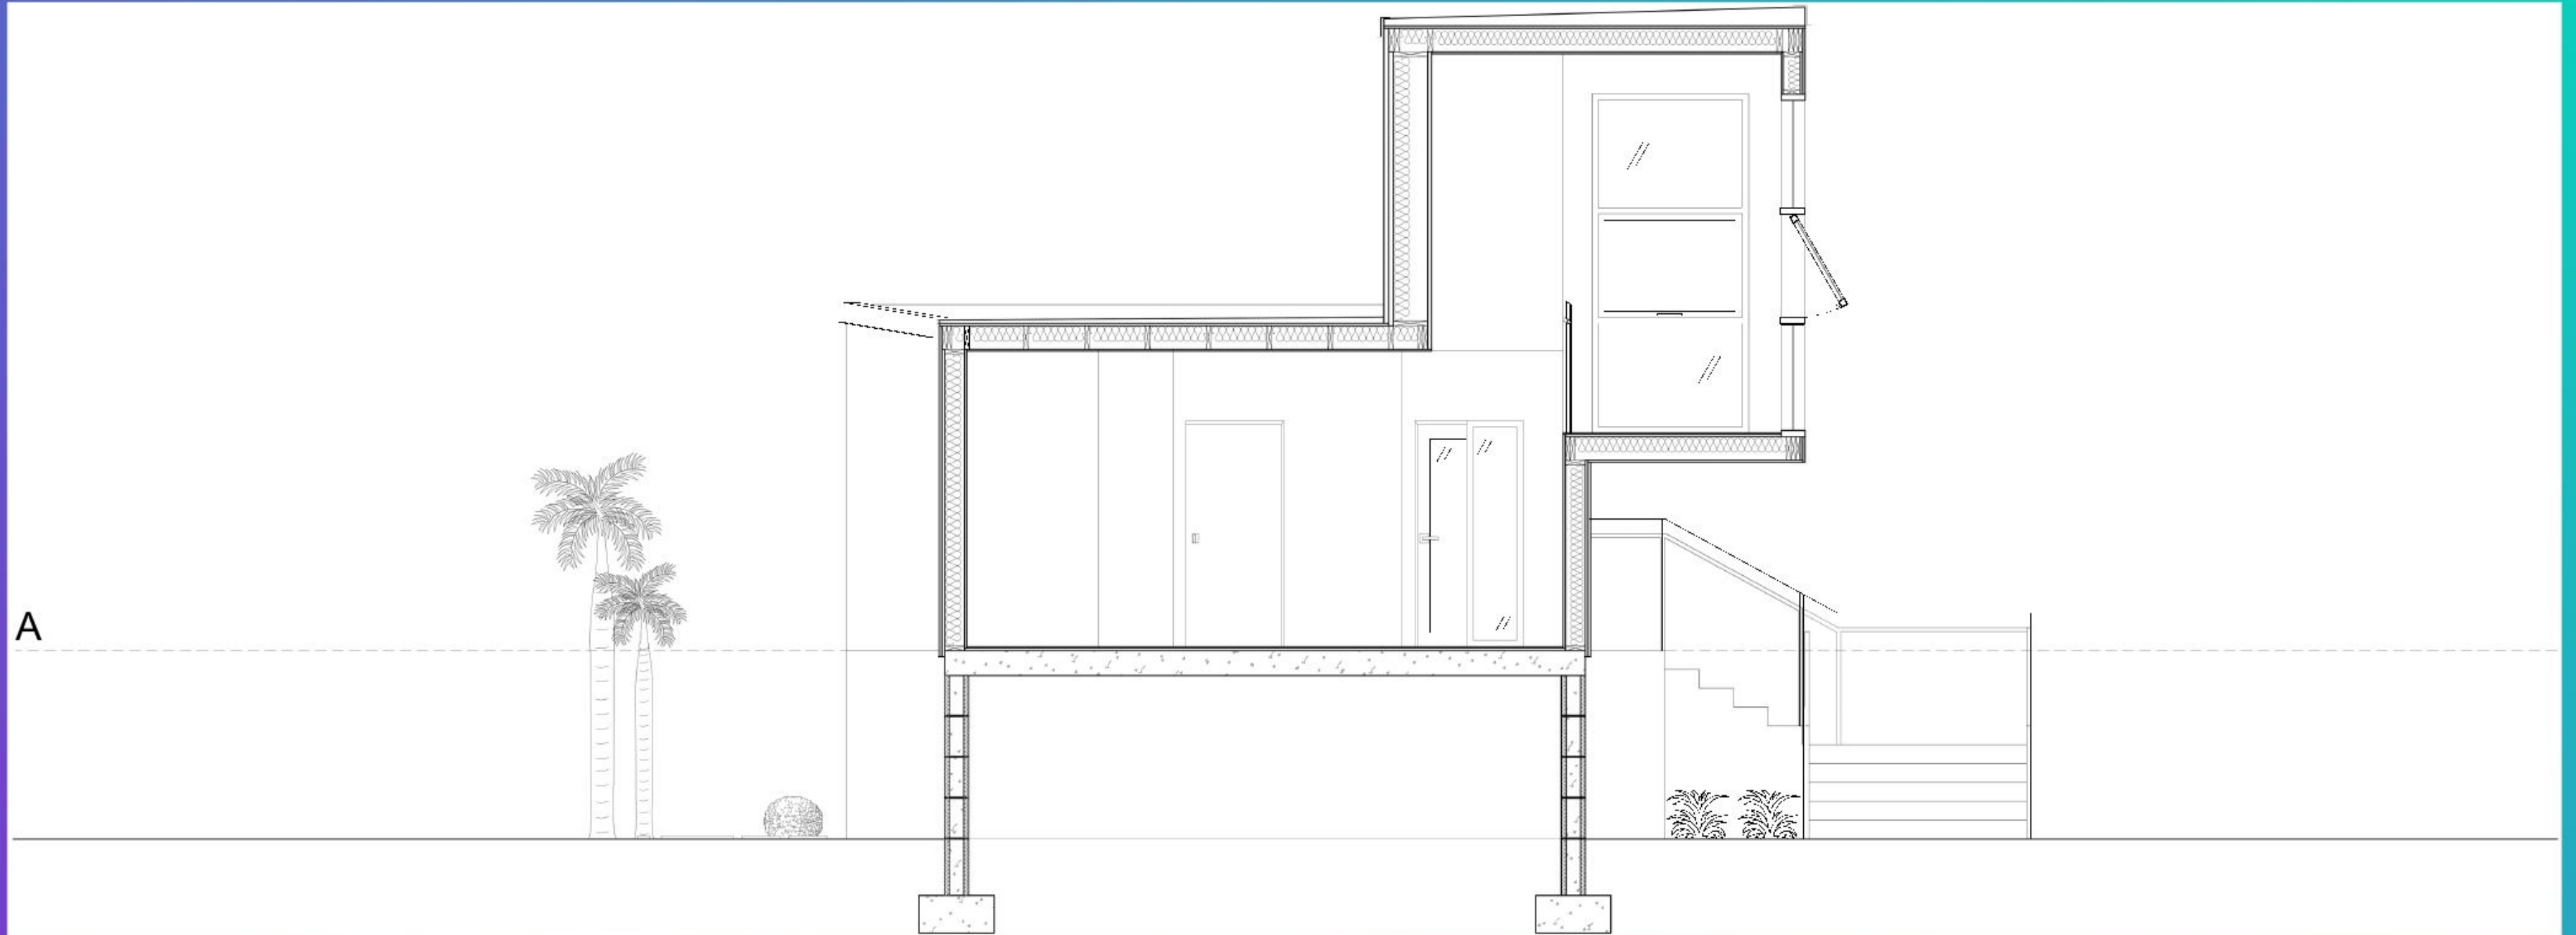



**ELEMENTS BIRD'S EYE
VIEW AXON 1: FRAME,
BATH, STAIR**

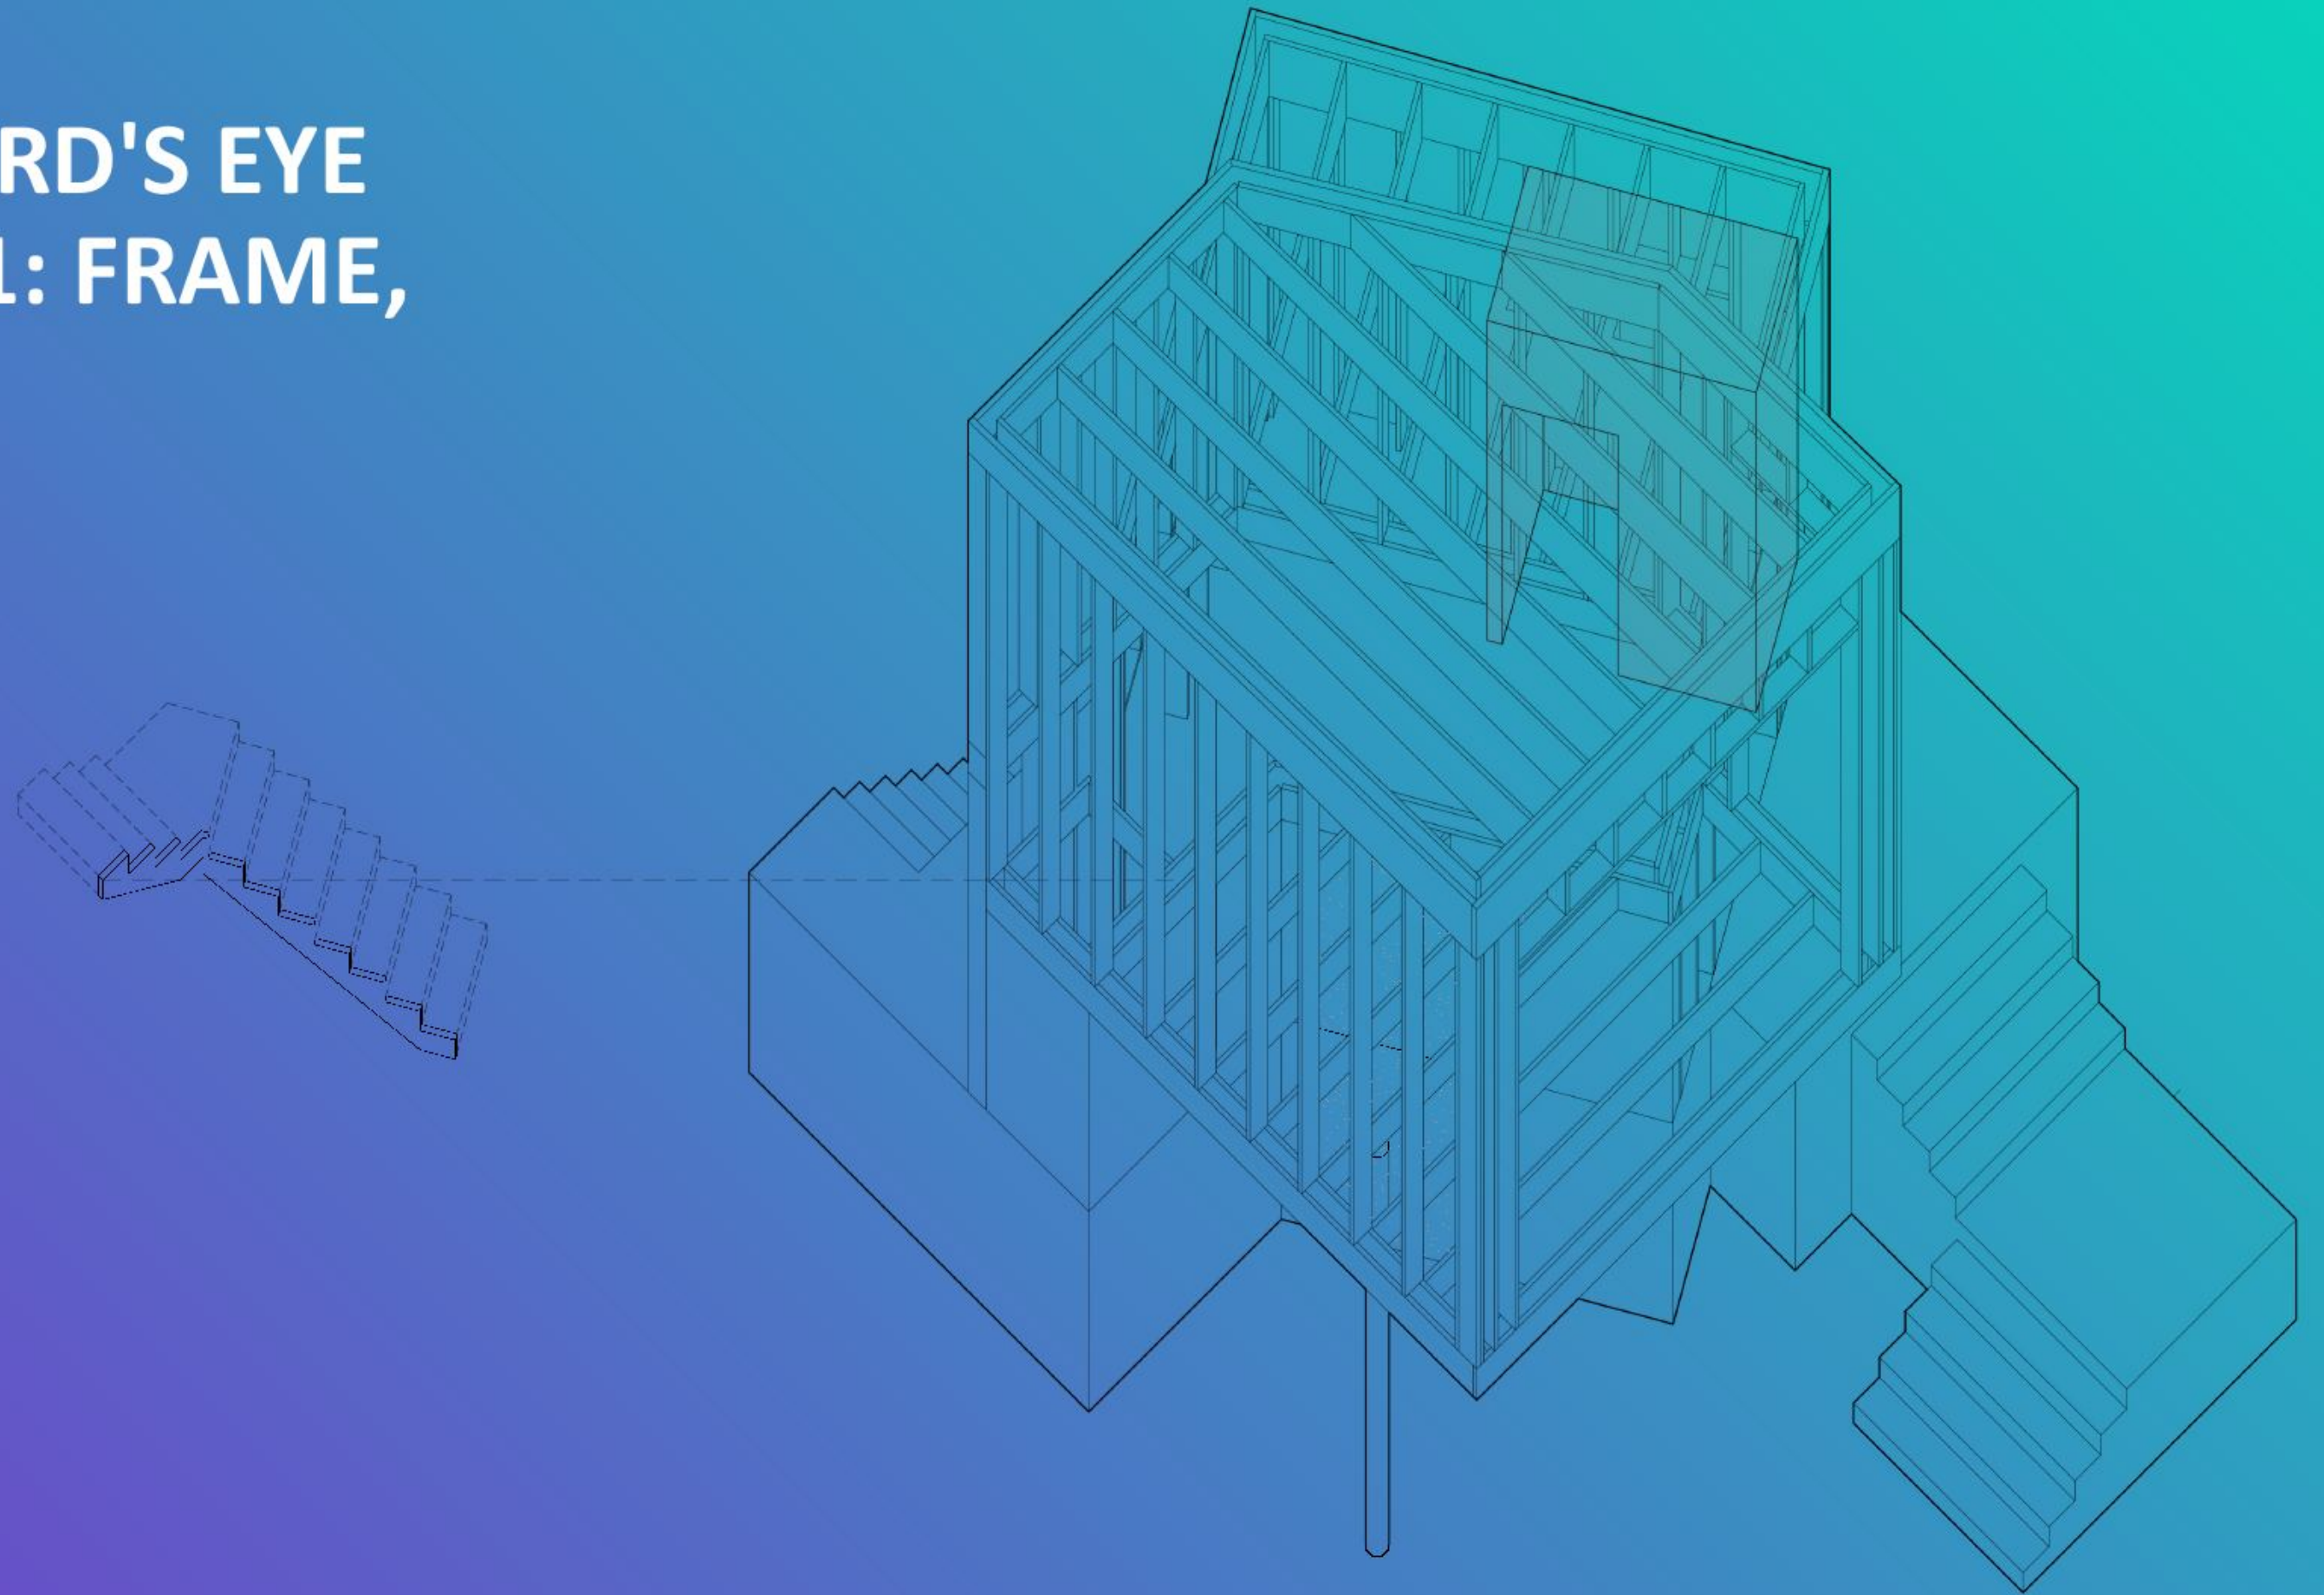


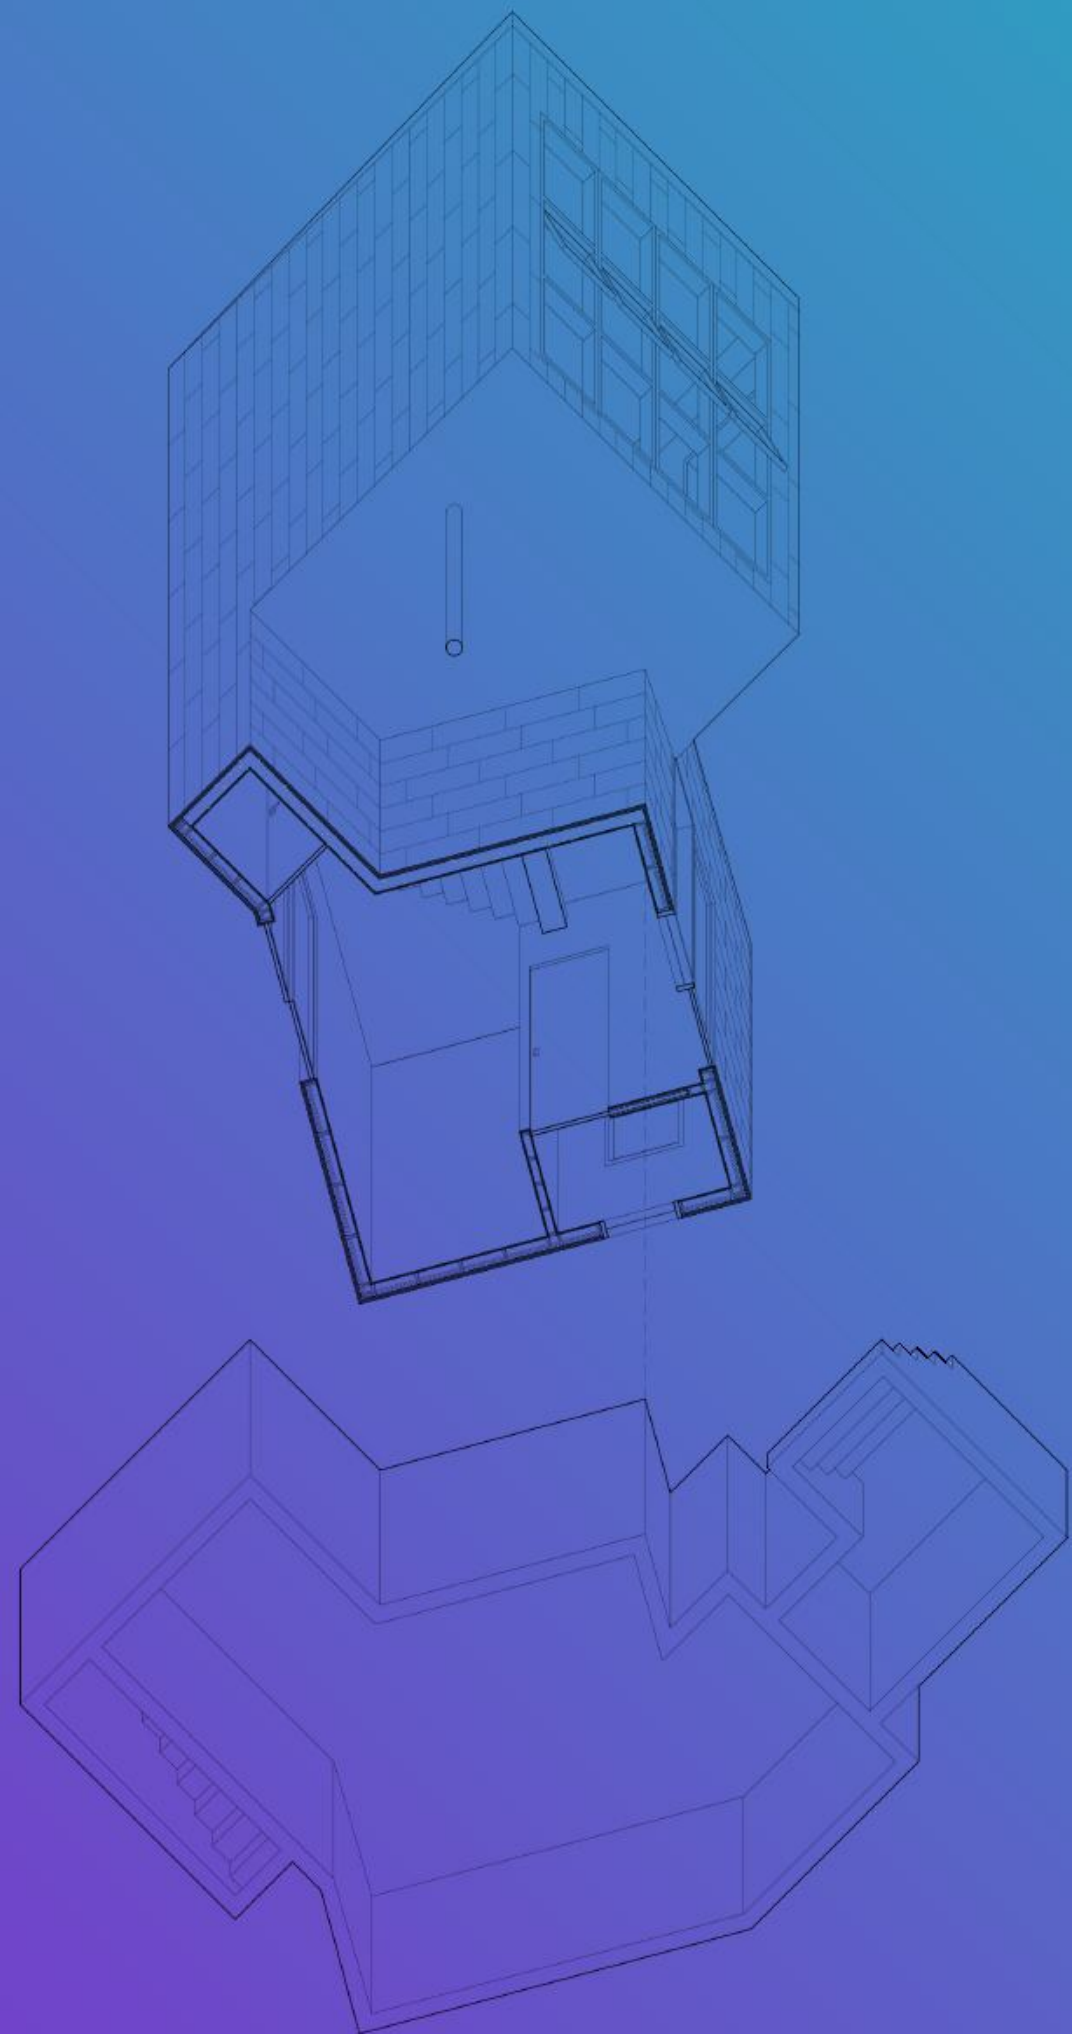


**ELEMENTS WORM'S
EYE VIEW AXON 2:
WALL, FLOOR, ROOF,
WINDOW, DOOR**

CORSS SECTIONS THROUGH ROOM AND PORCH

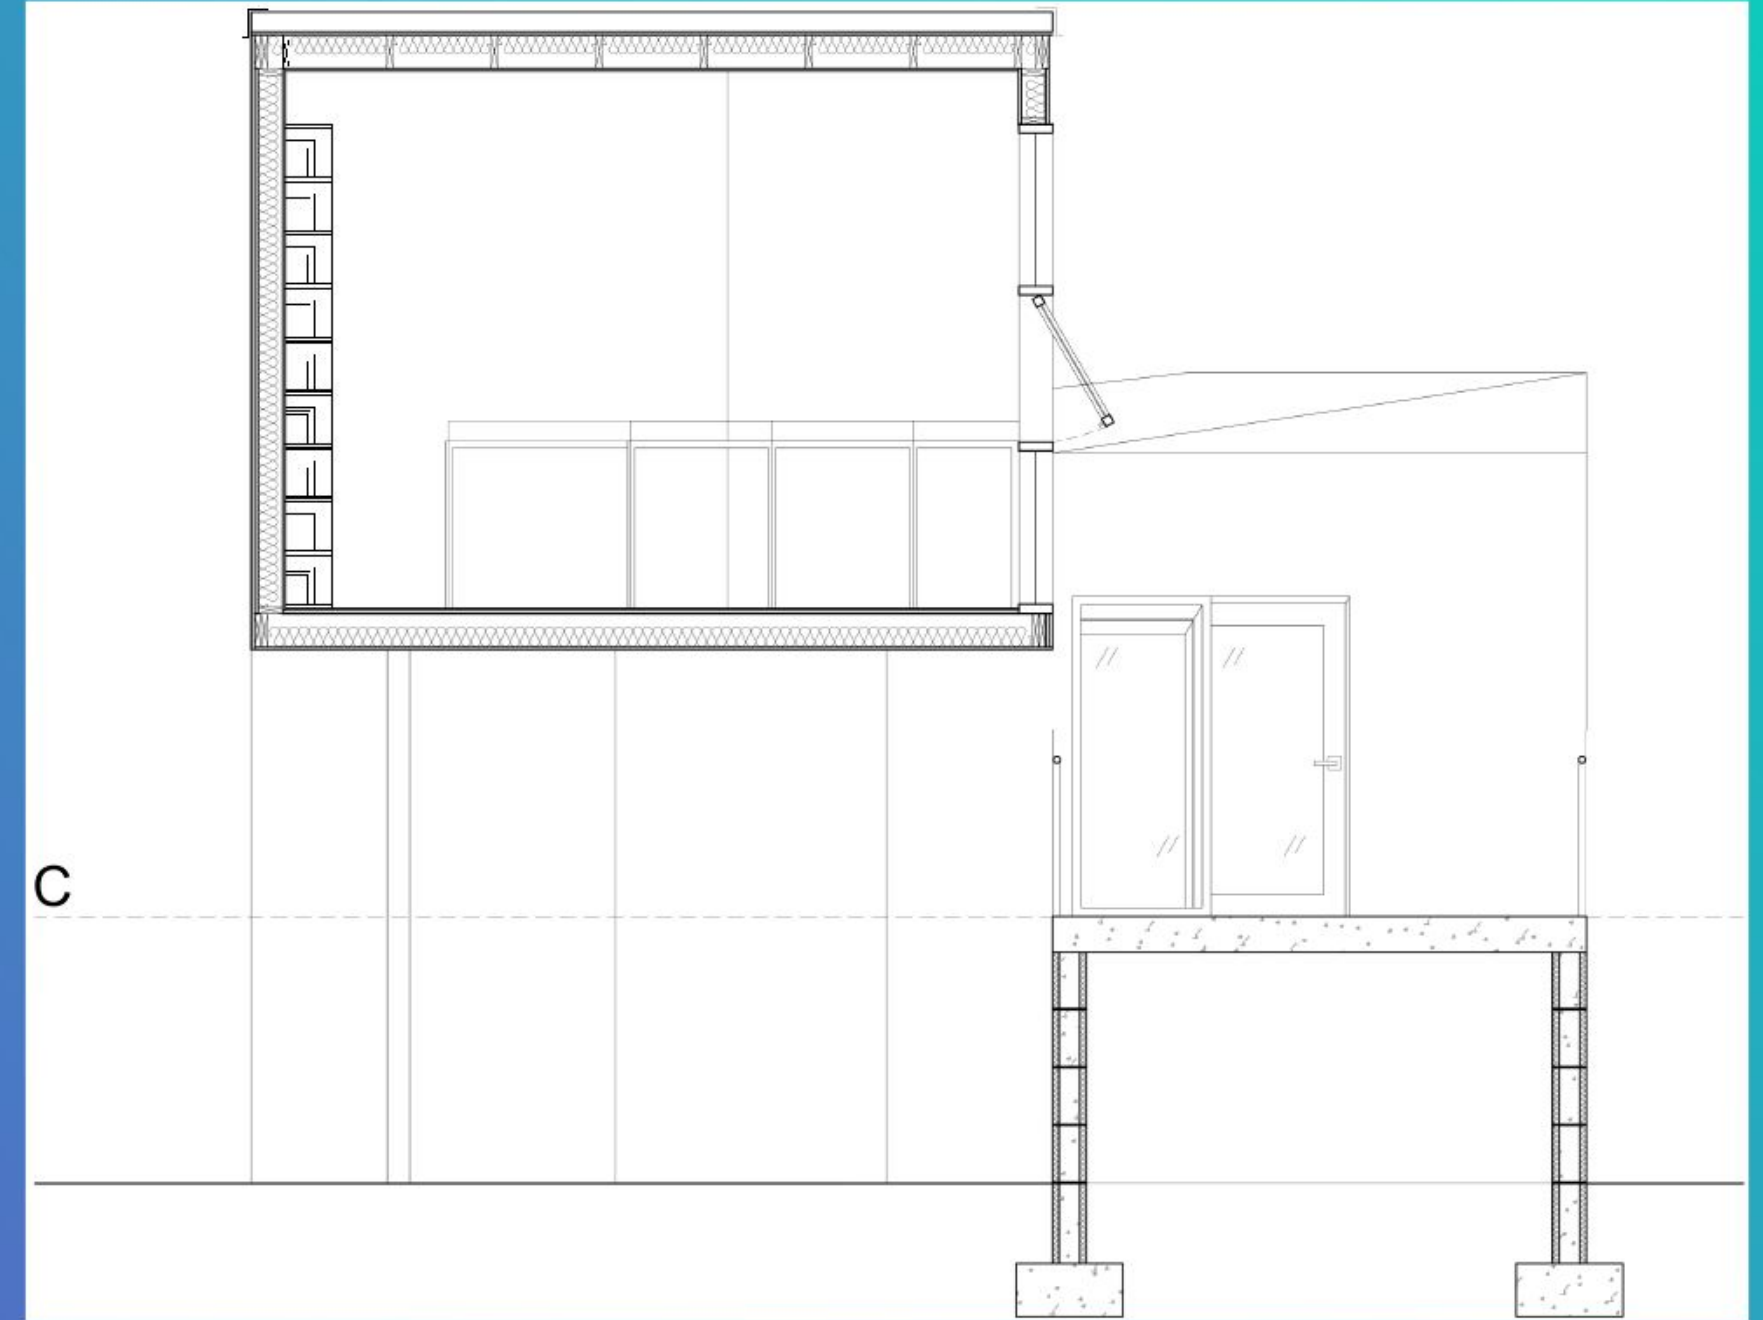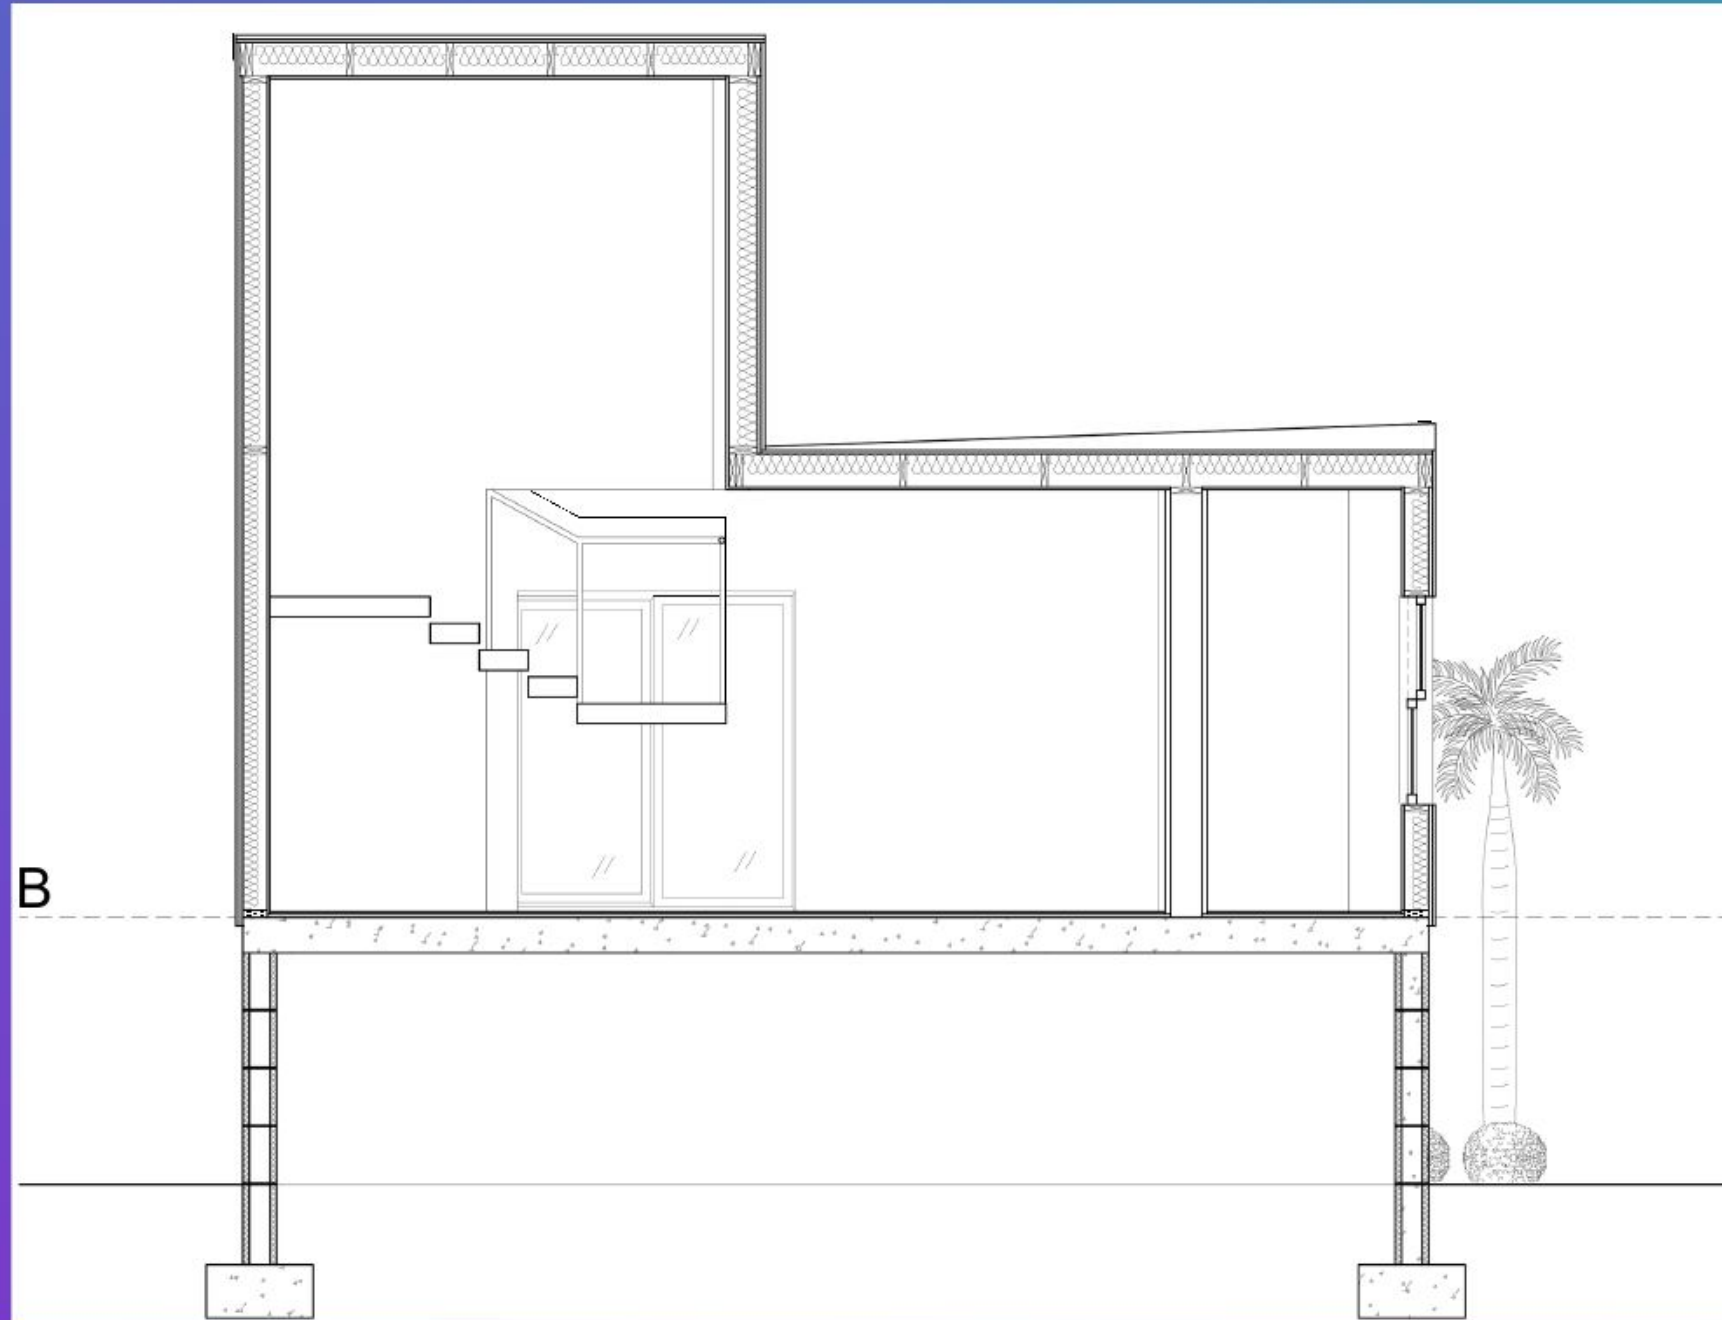

INITIAL DESIGN STRUCTURE MODEL

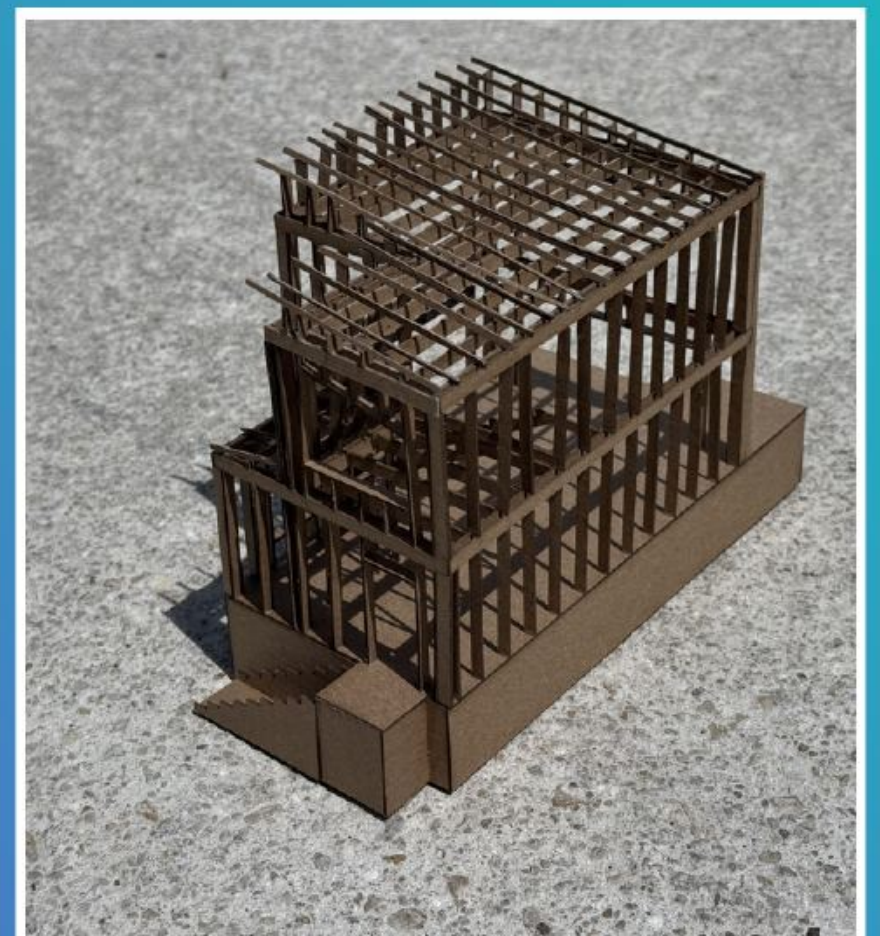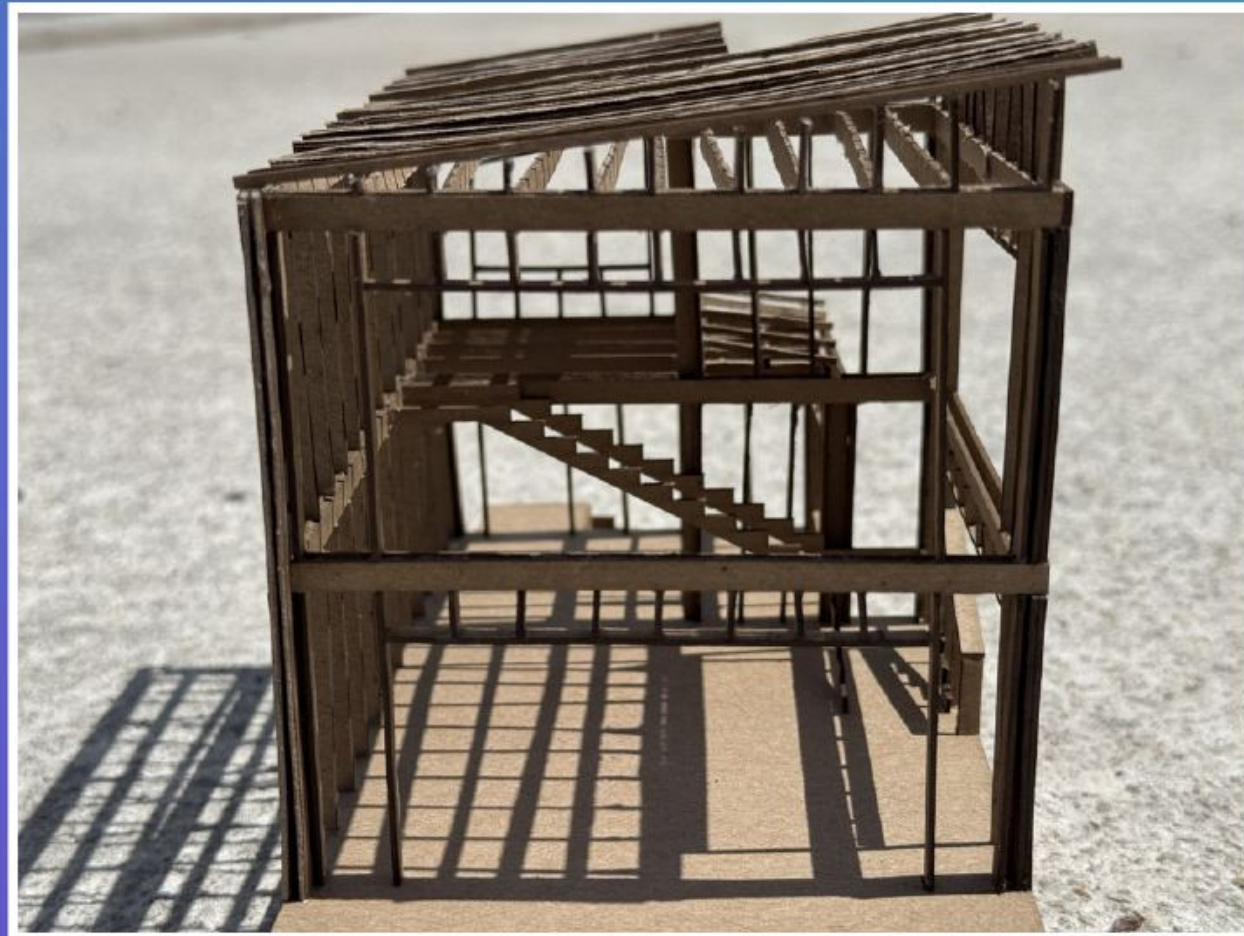



FINAL DESIGN STRUCTURE MODEL 1





FINAL DESIGN STRUCTURE MODEL 2



CONTACT ME



786-828-9949



emcuberos@hotmail.com



Miramar, FL



[https://www.linkedin.com/
in/emily-cuberos](https://www.linkedin.com/in/emily-cuberos)